



ID	DESCRIPTION	SIZE	REMARKS
IS	INSERT STIFFENER	4.6" x 4.6" x 96"	POST INSERT FOR (ALUMINUM OR STEEL) HEAVY WALL SUBSTITUTION
CF1	CONCRETE FOOTING	10"Ø x 28"	LINE POST: FOOTING (2,500 PSI)
CF2	CONCRETE FOOTING	12"Ø x 30"	HINGE POST: FOOTING (2,500 PSI)
CF3	CONCRETE FOOTING	12"Ø x 12"	DROP ROD: FOOTING (2,500 PSI WITH (RE) RECEIVER
DR	DROP ROD (LOCKABLE)	3/8"Ø x 24"	ROD WITH GUIDE, (4) SELF TAPPING #10 X 3/4" HEX HEAD SCREWS
GF	GATE FRAME	3.25"x3.25"x0.135"	FULLY MITERED & WELDED CORNERS (OPTIONAL- RIVETED)
GP	GATE POST	5" x 5" x 106"	0.250" WALL - HINGE SIDE ONLY
HI	HINGE	4" x 4"	SELF CLOSING, (4) SMS #10 X 3/4" HEX HEAD SCREWS
HR	HORIZONTAL RAIL	3.25"x3.25"x0.135"	OPTIONAL: 2" X 3.5"
LA	LATCH	4" x 4"	SELF-LATCHING, (4) SELF TAPPING #10 X 3/4" HEX HEAD SCREWS
LP	LINE POST	5" x 5"	STANDARD WALL= 0.135", HEAVY WALL= 0.250"
PIA	PICKET	7/8" X 6"	-
PIB	PICKET	1" x 1"	REQUIRED FOR EXECUTIVE SHADOWBOX STYLE
RE	RECEIVER	1/2" X 6"	STEEL, GALVANIZED PIPE

POOL CODE DESIGN NOTES: (FBC 454.2.17)


- A. **GATES:** All gates shall open outward, be 48" high and have no opening more than 1/2" within 18" of the latch. Shall be self-closing allowing the latch to fully engage securing the gate leaf.
- B. **RAILS:** Horizontal rails are to be spaced so that the top of rails shall exceed 45". Bottom rail shall be maximum 2" above grade. This will result in horizontal rails that are **NOT** evenly spaced.
- C. **PICKETS:** The typical **GAP SPACING** shall be 1-3/4 inches or less on the public side. This may change the PIB picket size to 1" x 3".
- D. **HARDWARE:**
- LATCHES:** Shall be a minimum of 54" above finished floor, lockable and self-latching.
- DROP RODS:** Shall be lockable on the inactive leaf.

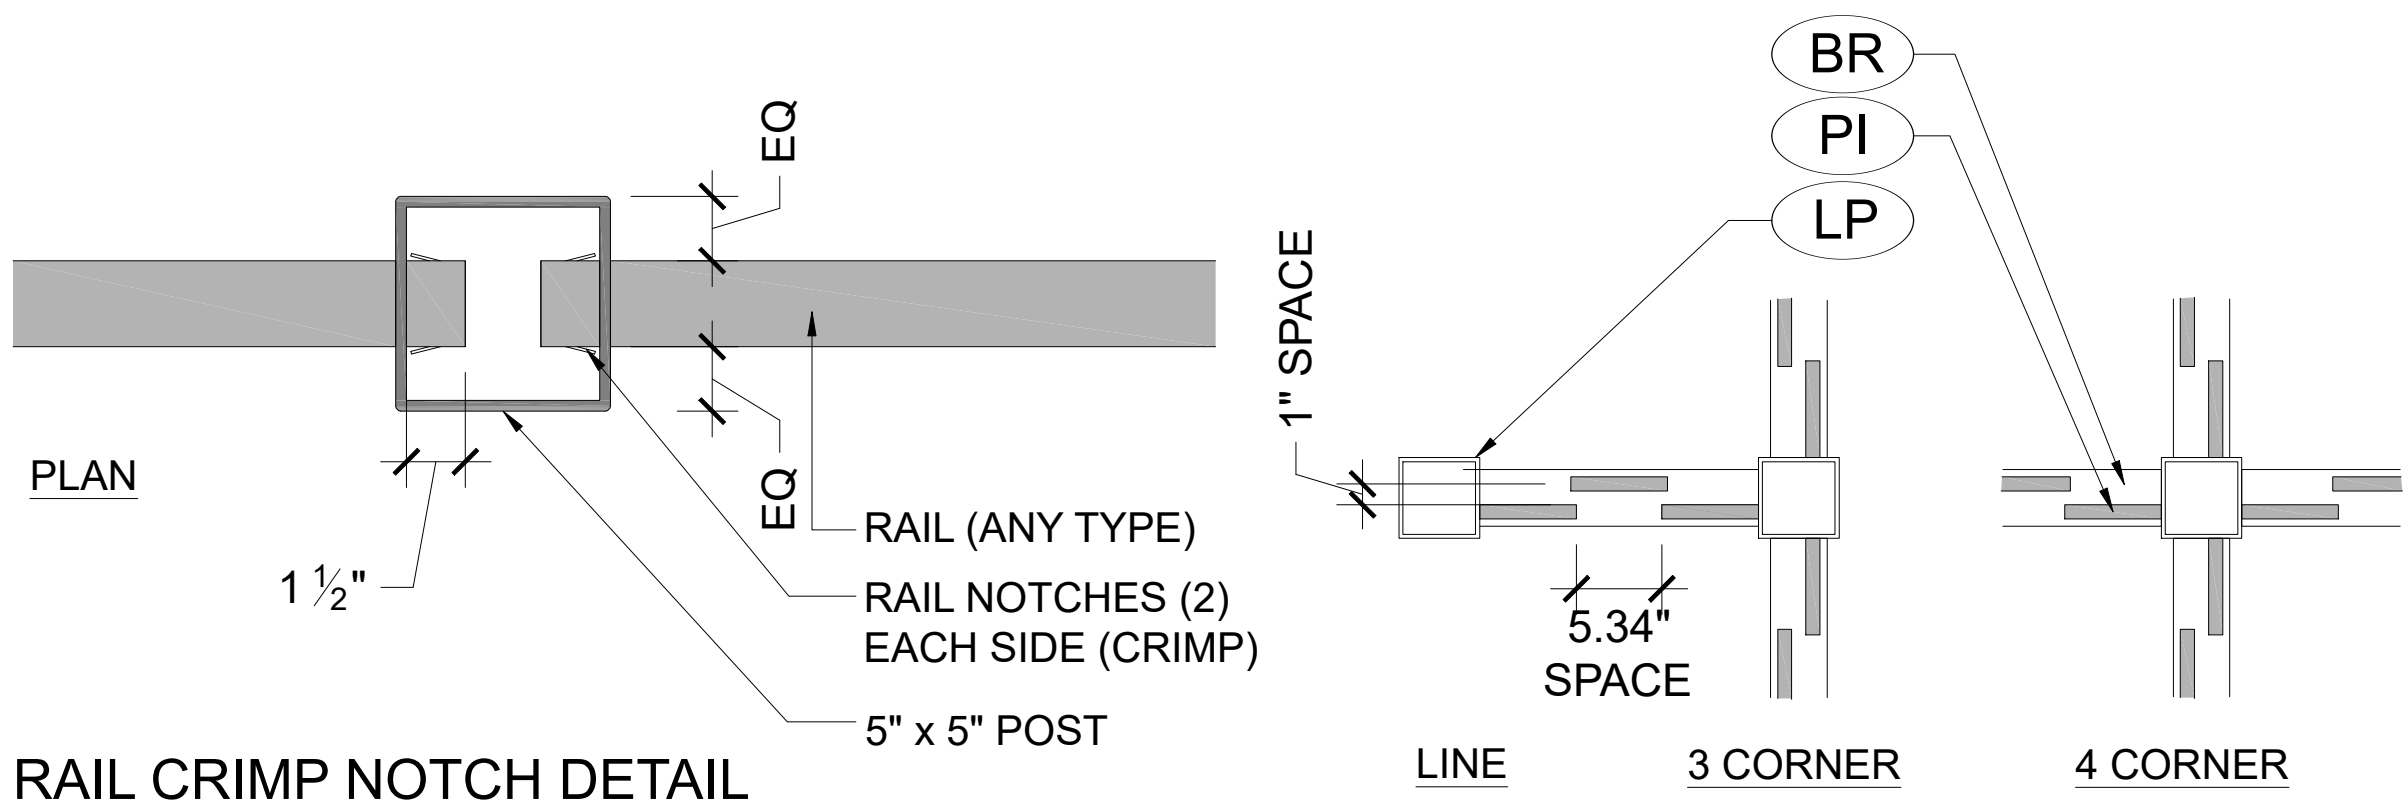


POOL CODE COMPLIANT !! Can be used around pools but must adhere to the GAP SPACING Required by the POOL CODE REQUIREMENTS!

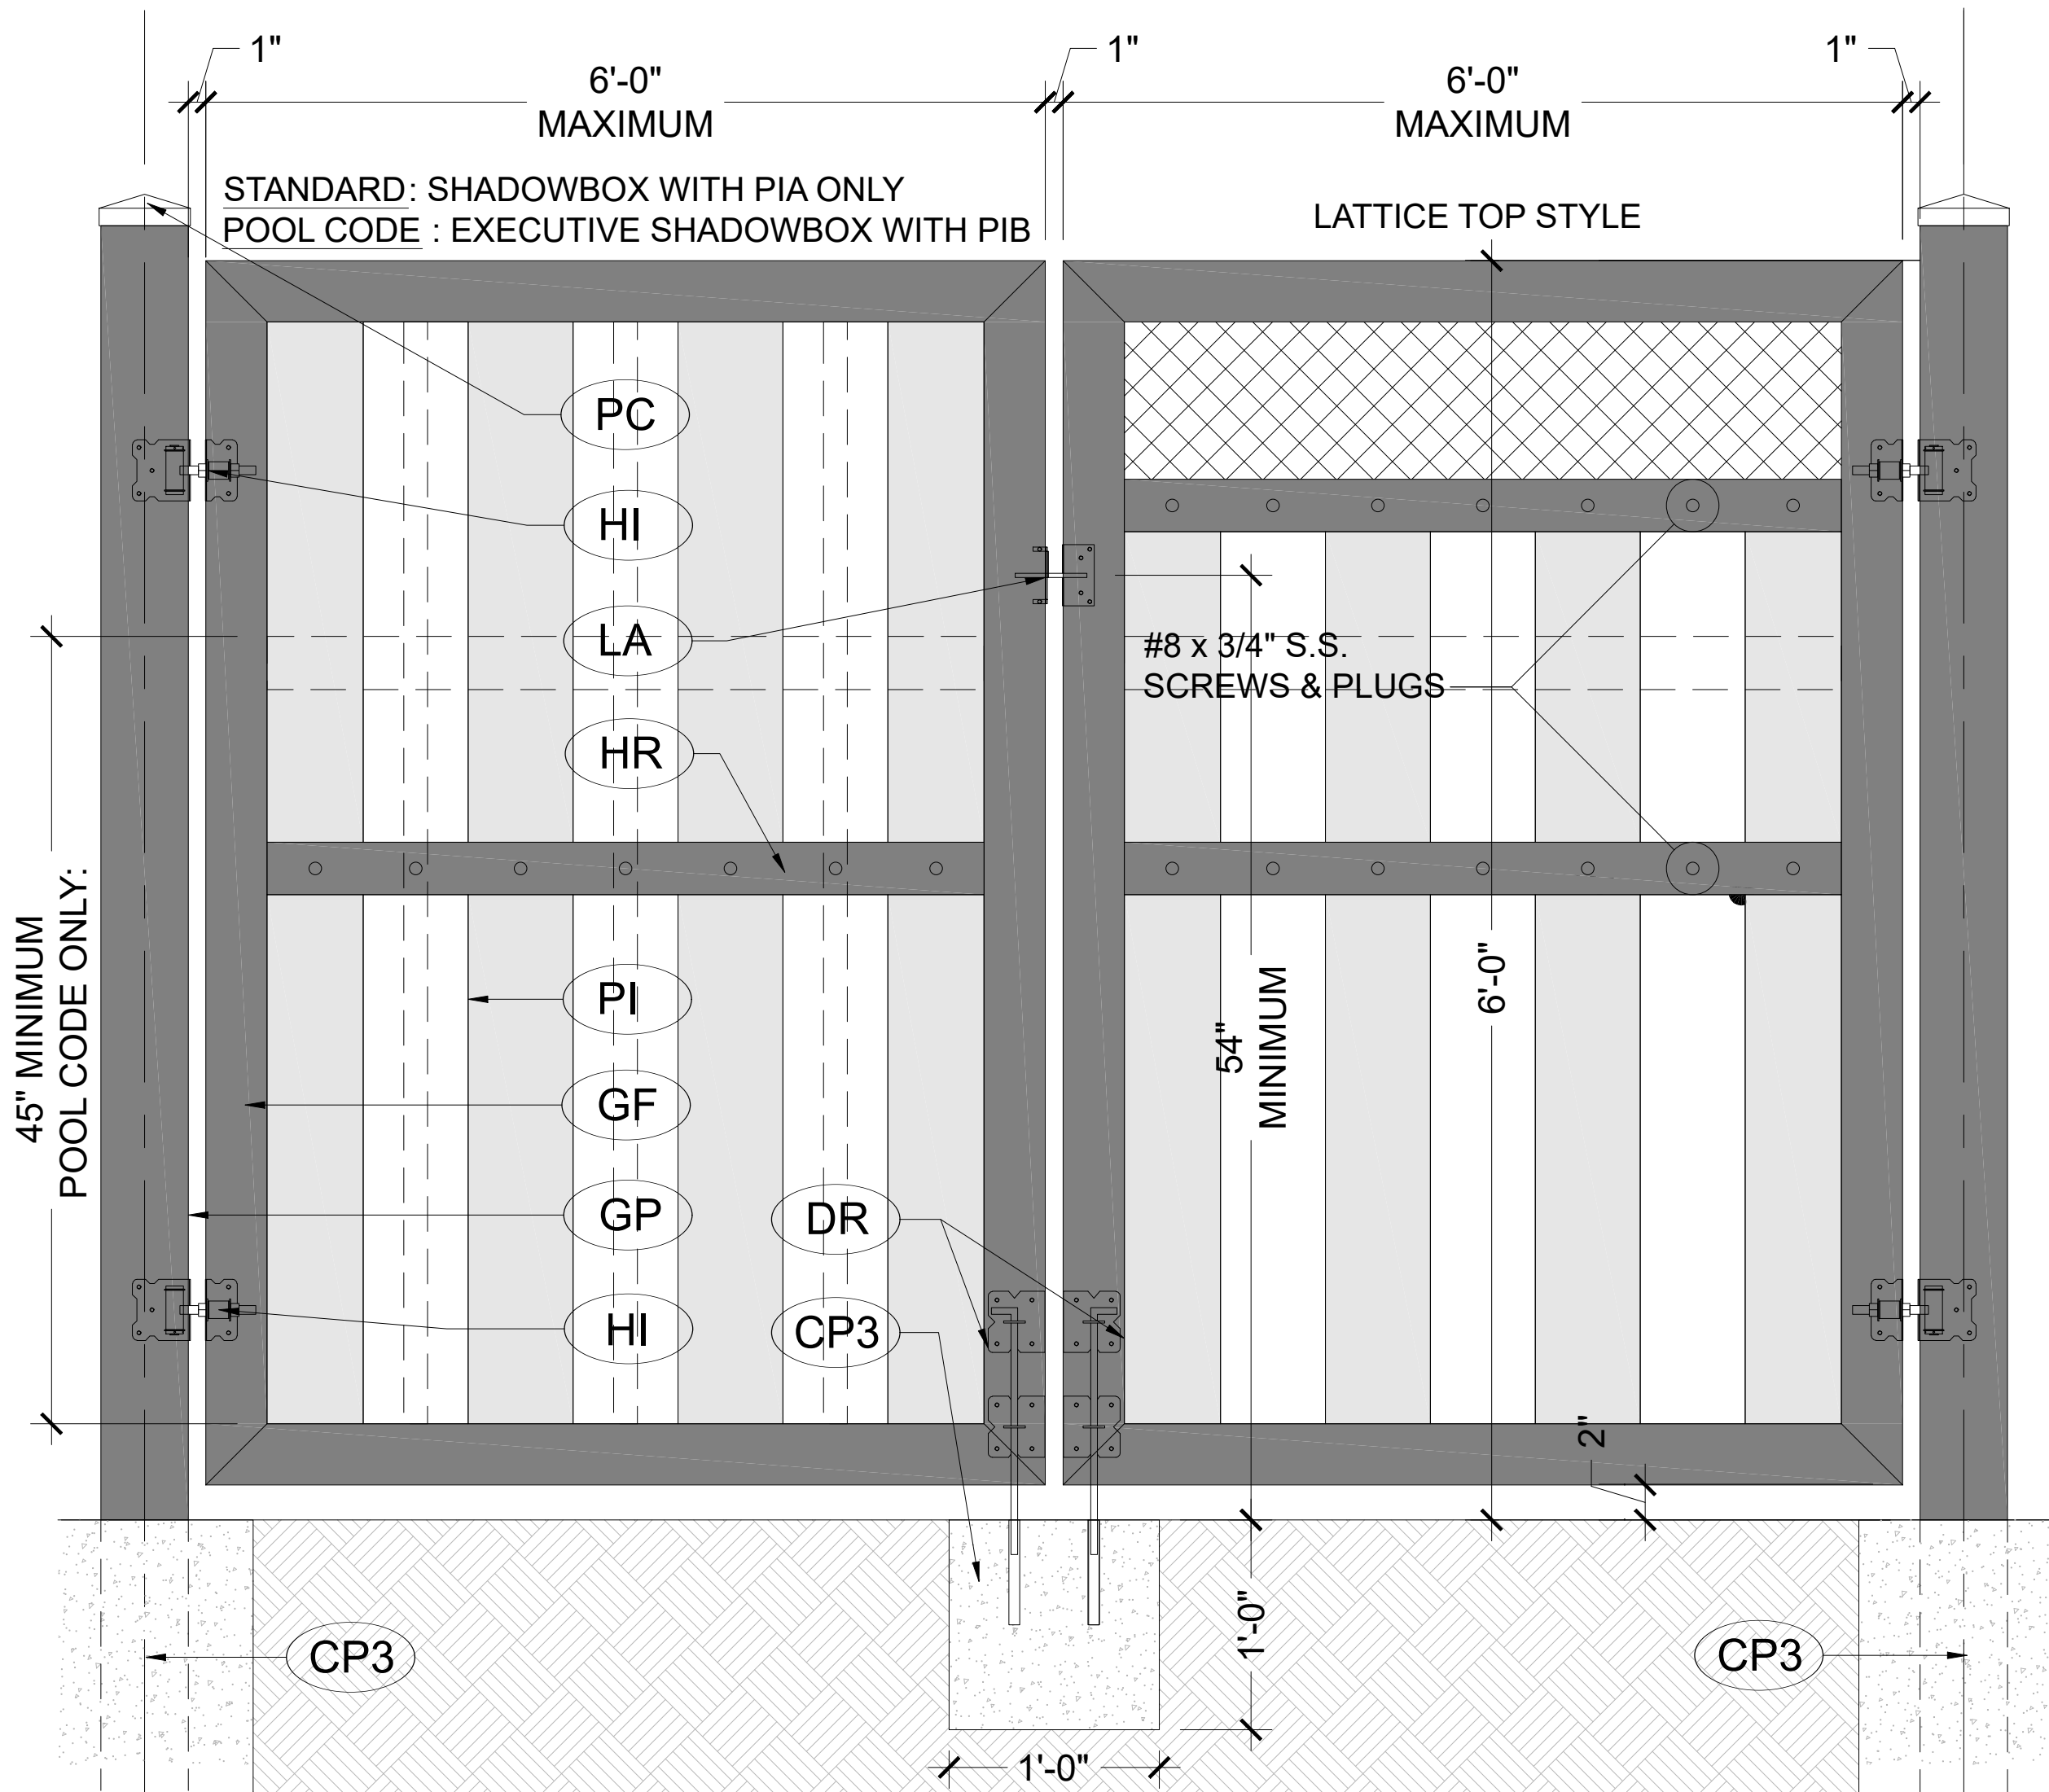

3 DOUBLE SWING GATE DETAILS
SCALE: 1/2"=1'-0"

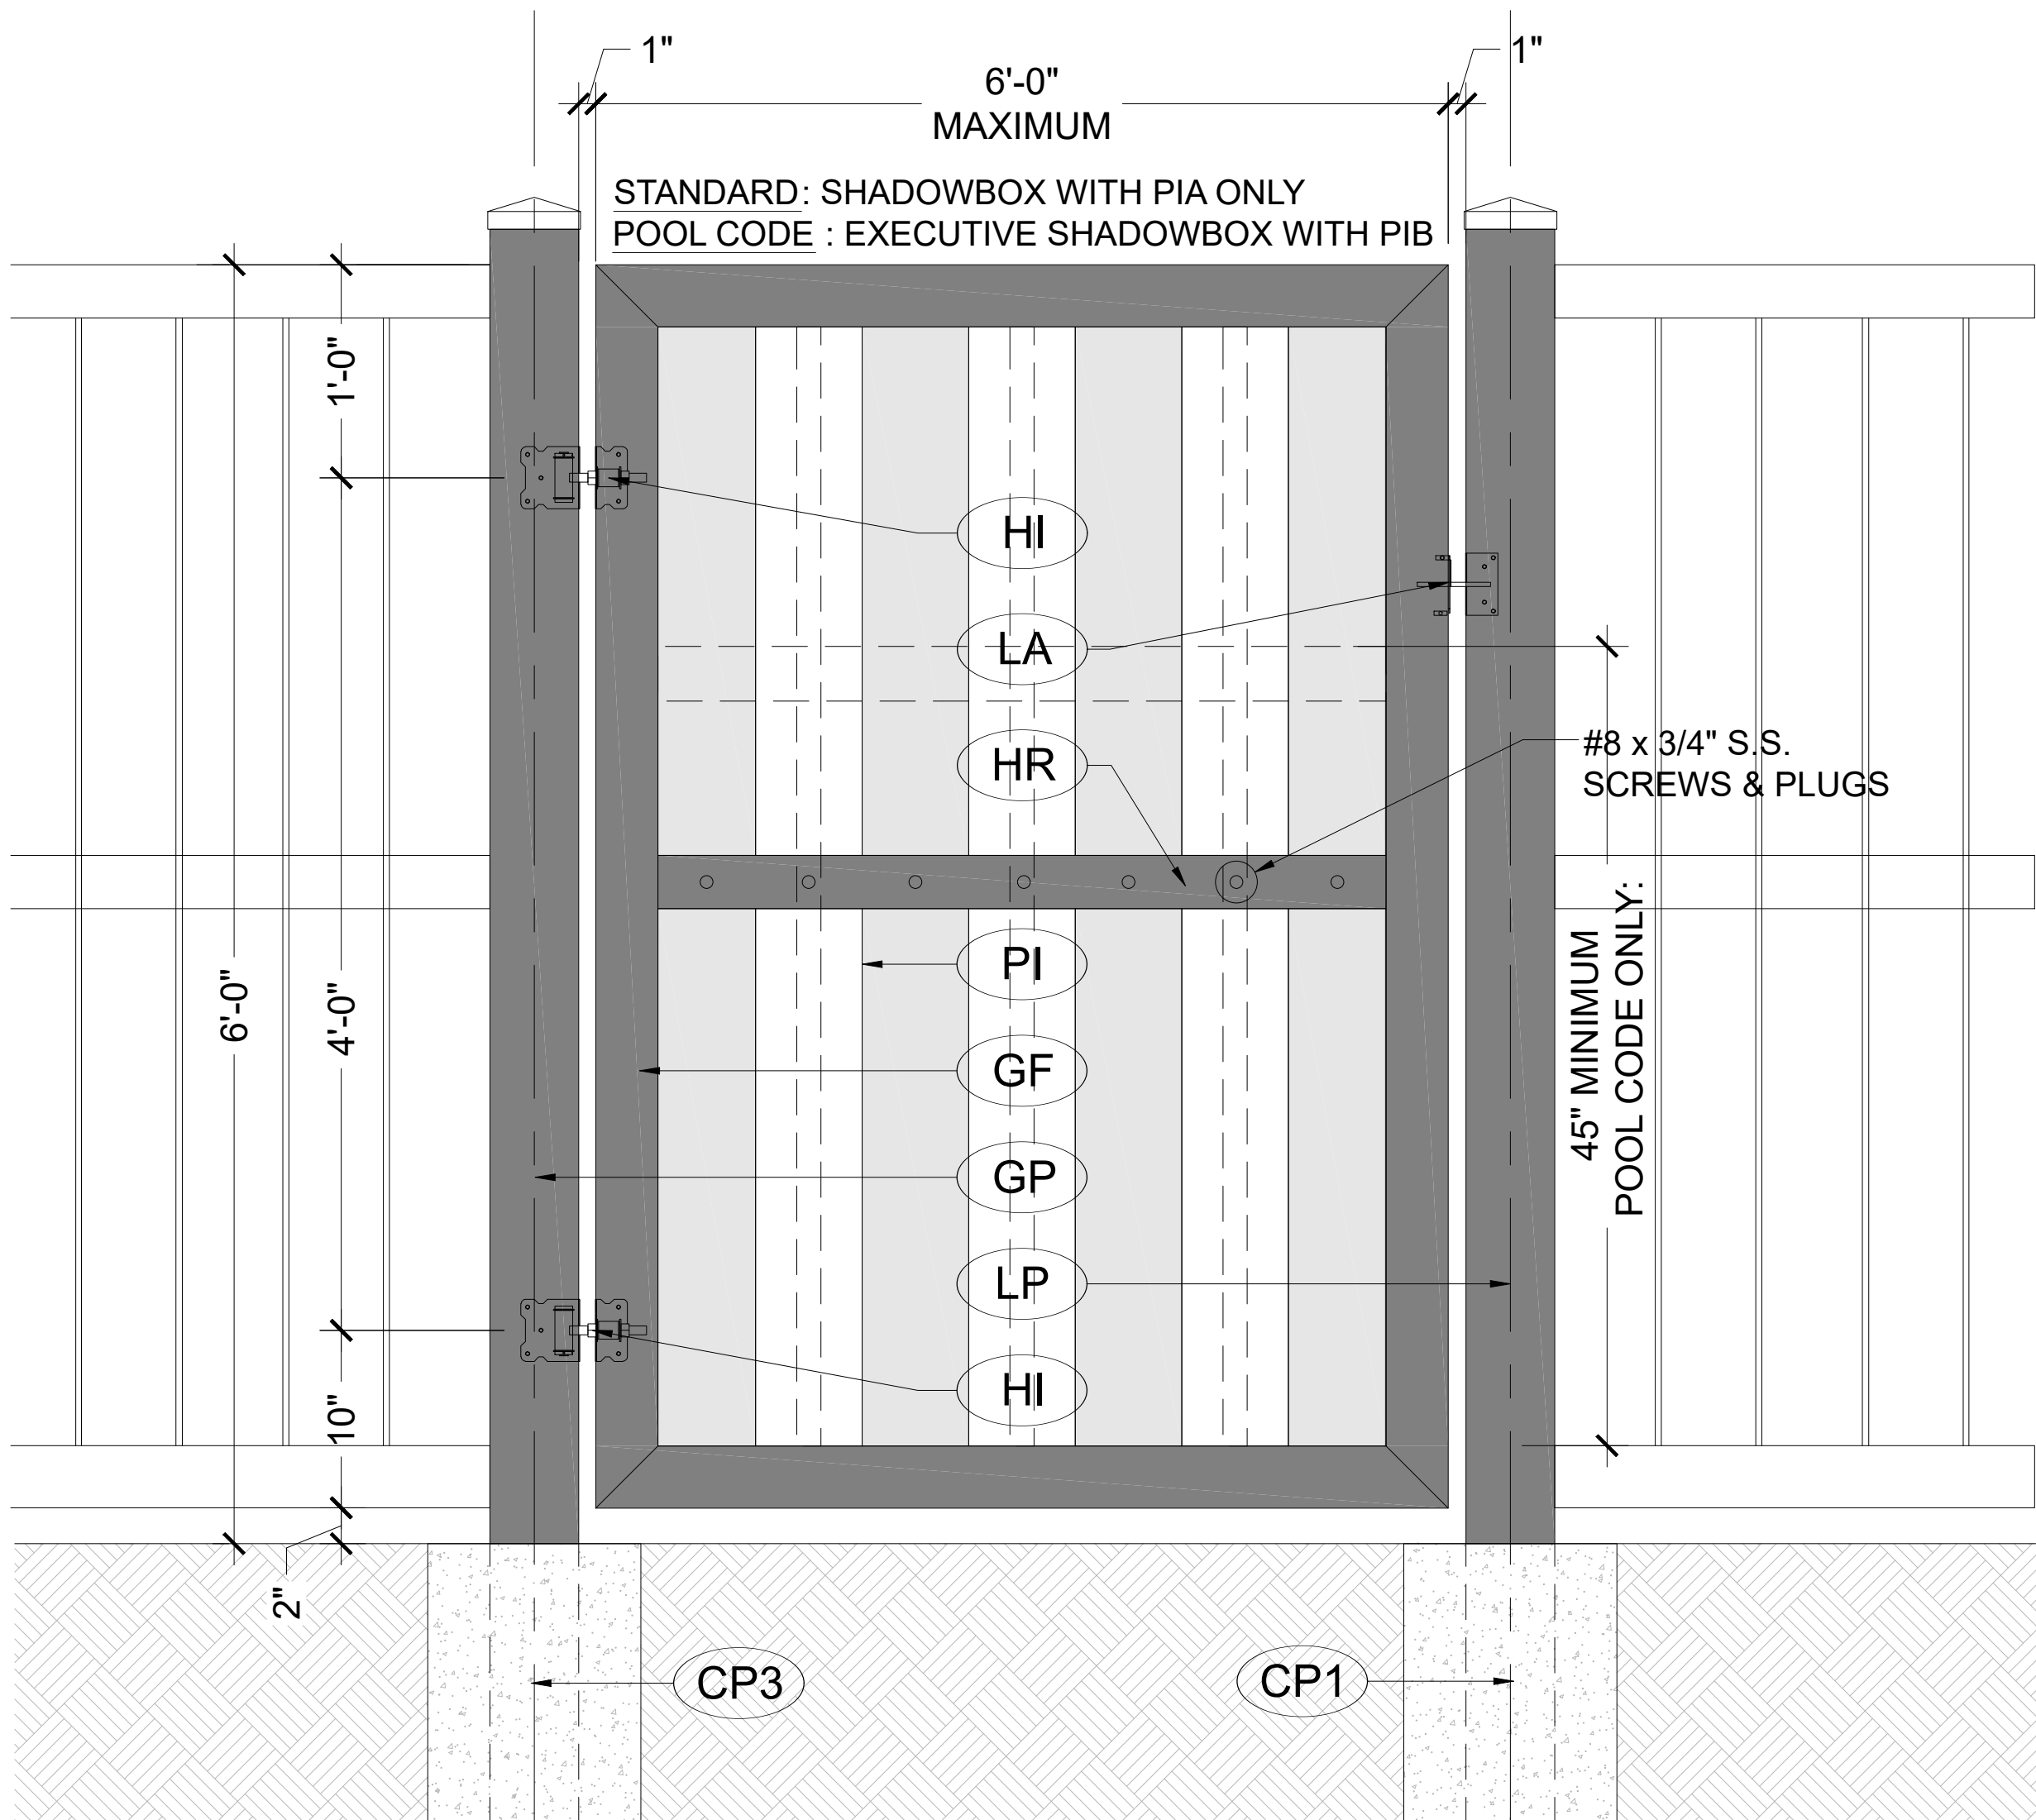

2 SINGLE SWING GATE DETAILS
SCALE: 1/2"=1'-0"

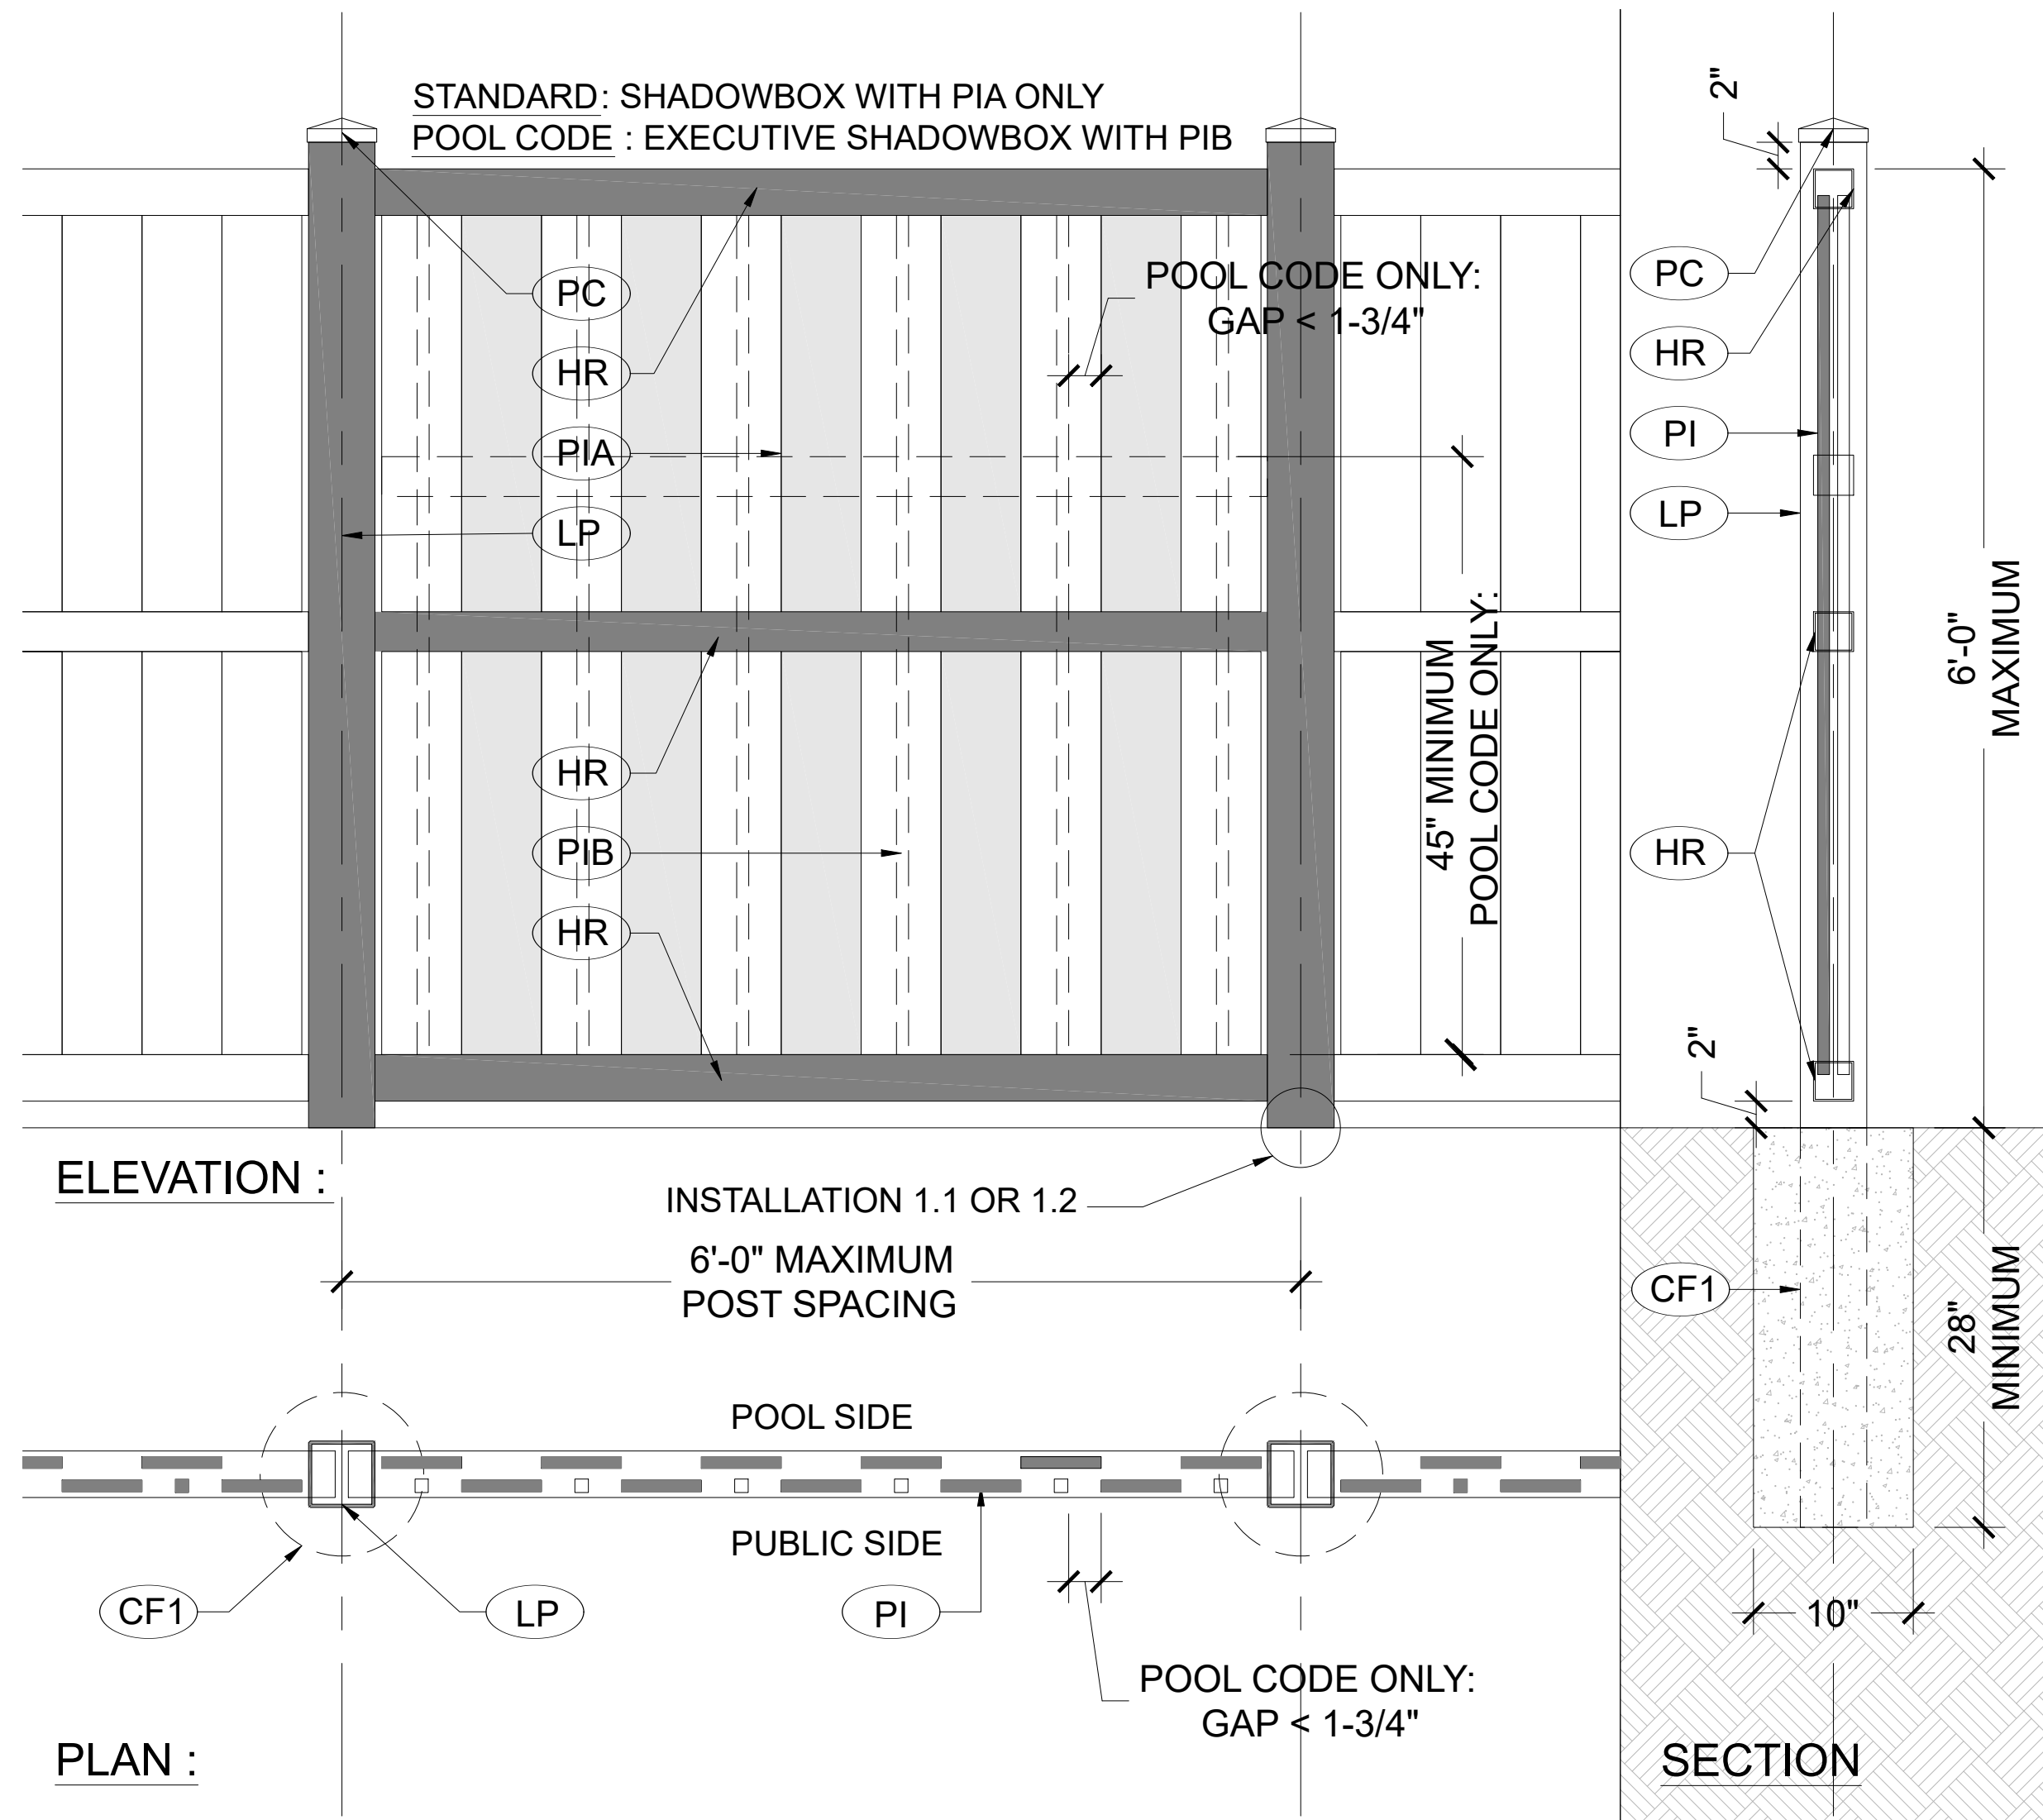

1 FENCING DETAILS
SCALE: 3/8"=1'-0"