



ID	DESCRIPTION	SIZE	REMARKS
CF1	CONCRETE FOOTING	10"Ø x 24"	LINE POST: FOOTING (3,000 PSI MINIMUM)
CF2	CONCRETE FOOTING	12"Ø x 30"	HINGE POST: FOOTING (3,000 PSI MINIMUM)
CF3	CONCRETE FOOTING	12"Ø x 12"	DROP ROD: FOOTING (3,000 PSI MINIMUM) WITH 3/4"Ø GALV. PIPE
DR	DROP ROD	3/8"Ø x 24"	STANDARD DROP BOLT (LOCKABLE)
GF	GATE FRAME	2" x 2" x 0.125"	ALL CORNERS FULLY WELDED
GP	GATE POST	4" x 4" x 90"	0.25" GA.
HI	HINGE	N/A	STANDARD 4" SELF-CLOSING HINGES
HR	HORIZONTAL RAIL	1.6" x 2.6" x 0.06"	PICKETS MAY BE THRU OR STOP@ RAIL
LA	LATCH	N/A	STANDARD SELF-LOCKING LATCH
LP	LINE POST	2.5"x 2.5" x 90"	0.188" GA.
PI	PICKET	1" x 1" x 0.044"	-
TR	TOP RAIL	1.6" x 2.6" x 0.06"	-
WC	WALL CLIP	1-3/8" x 1-1/4"	-

POOL CODE COMPLIANT !! Can be used around pools but must adhere to the
HEIGHT & GAP SPACING Required by the POOL CODE REQUIREMENTS!

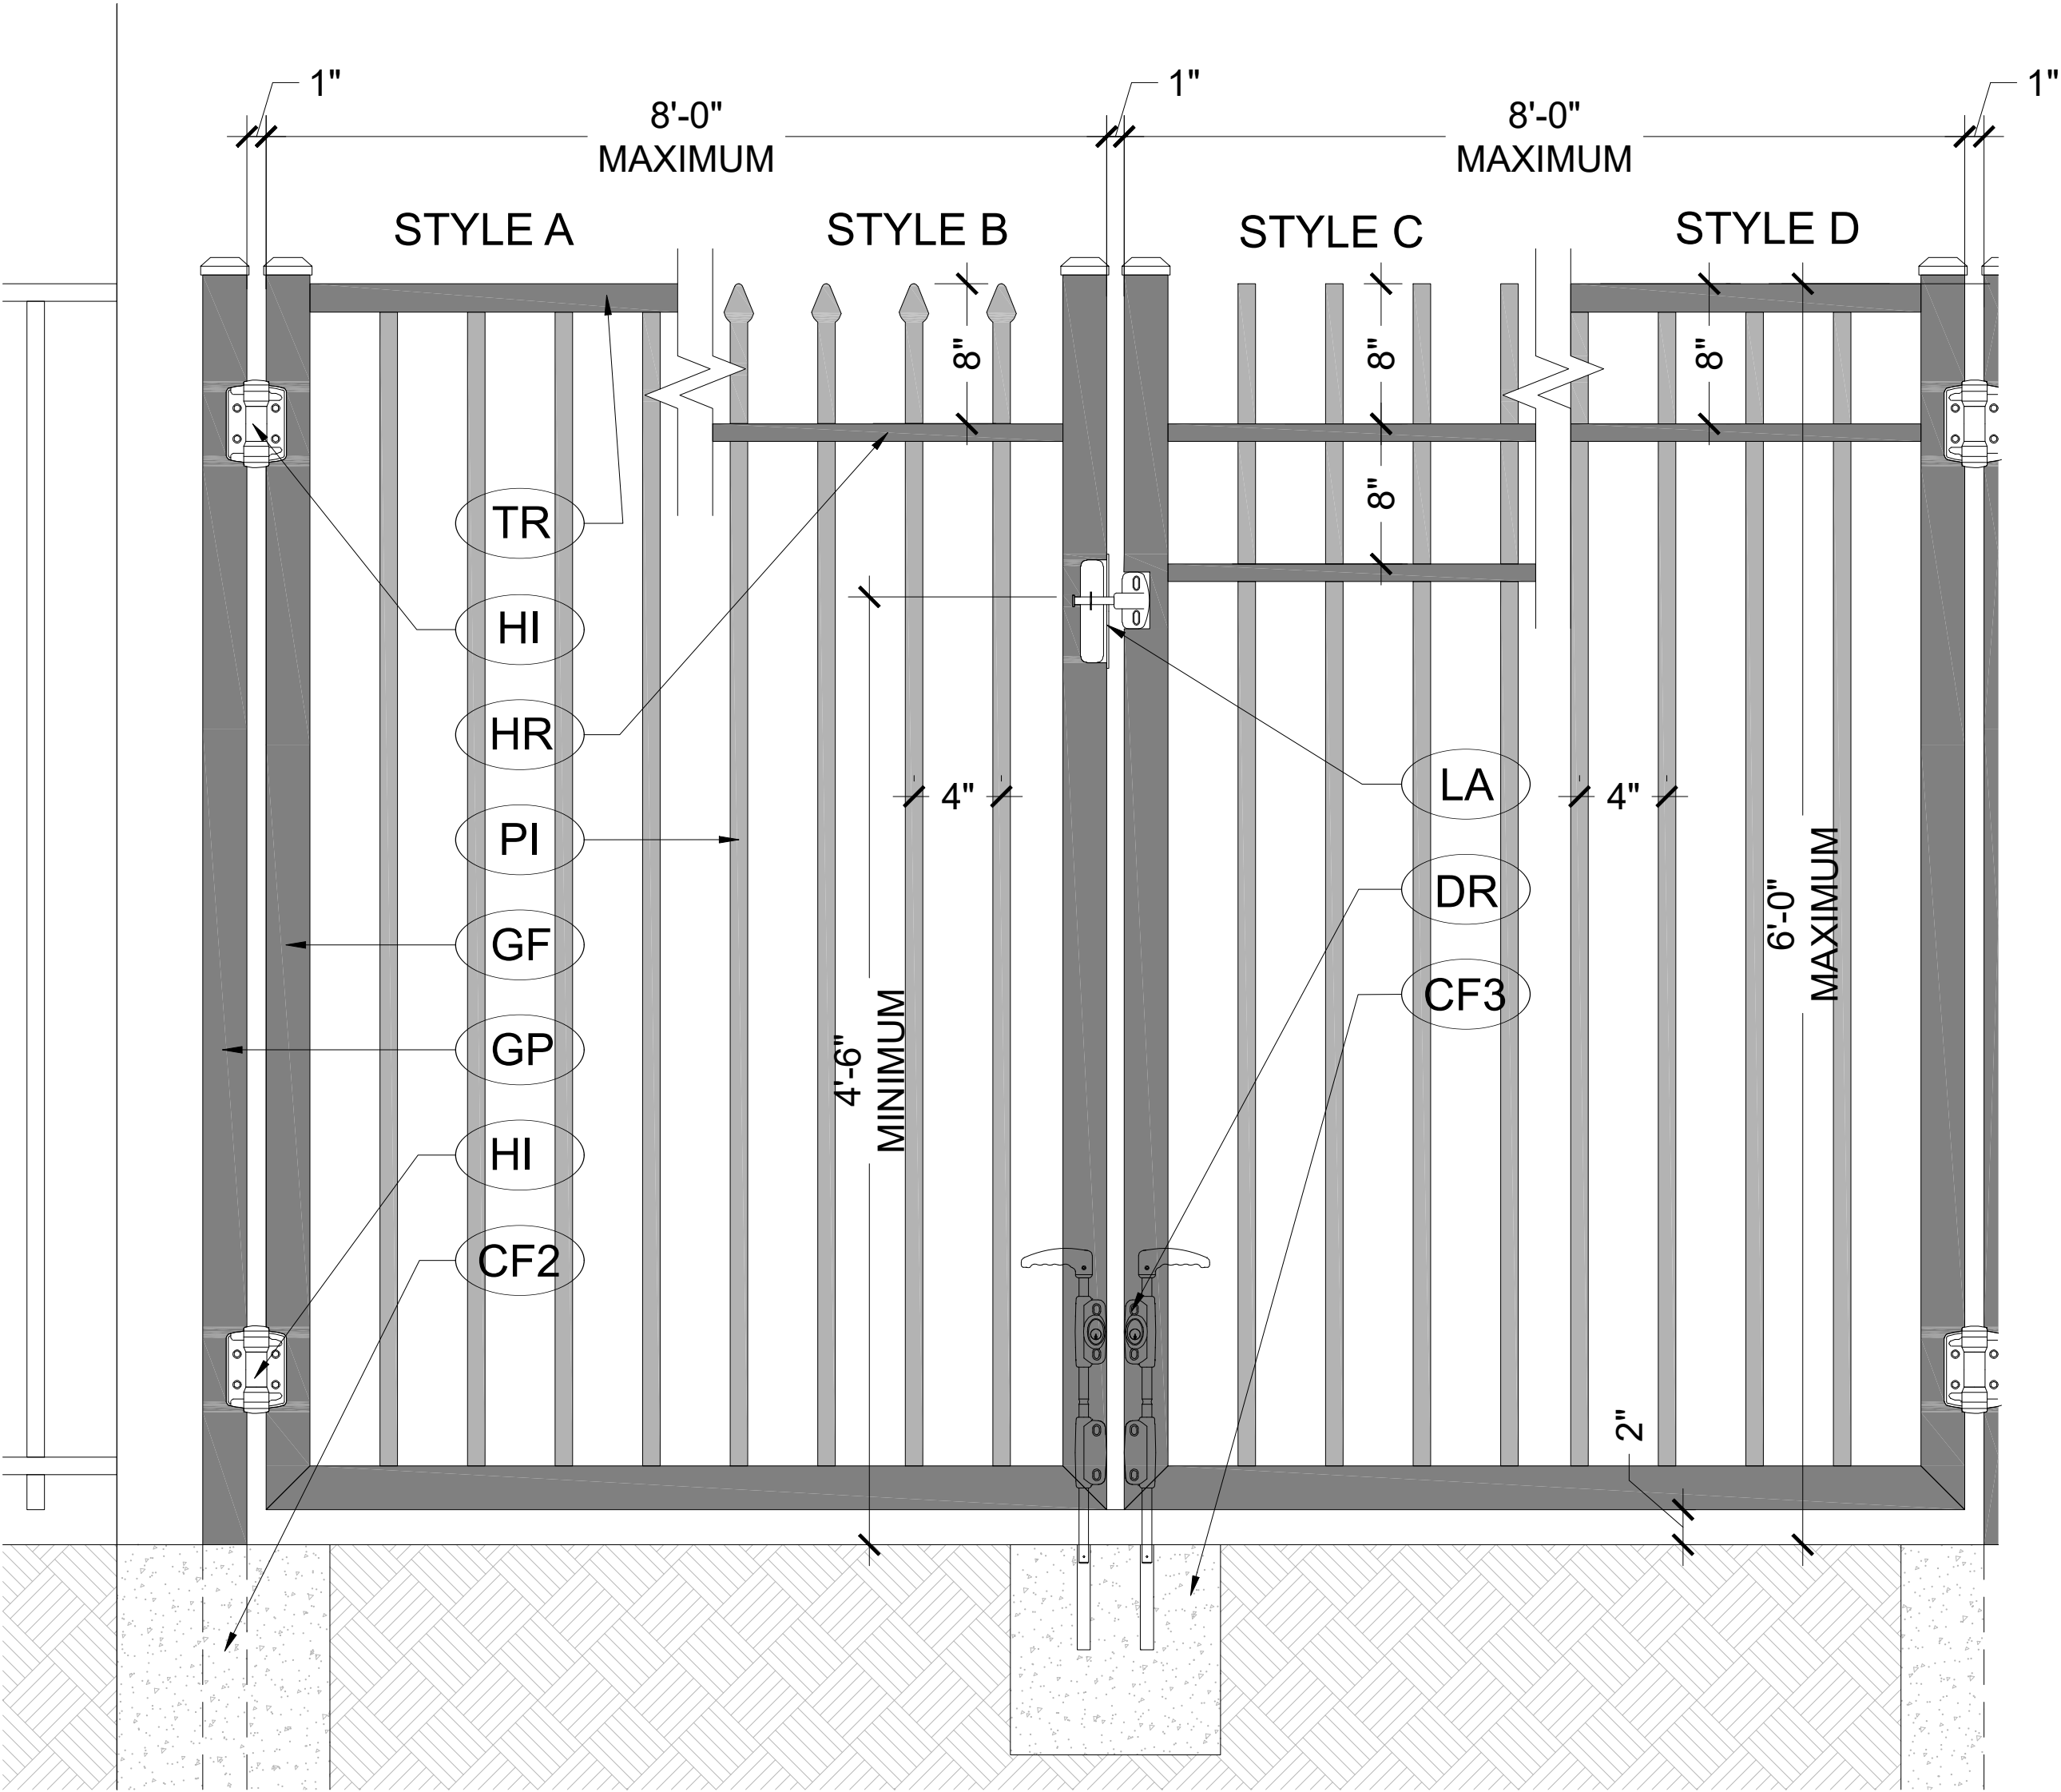


3 DOUBLE SWING GATE DETAILS

SCALE: 1/2"=1'-0"

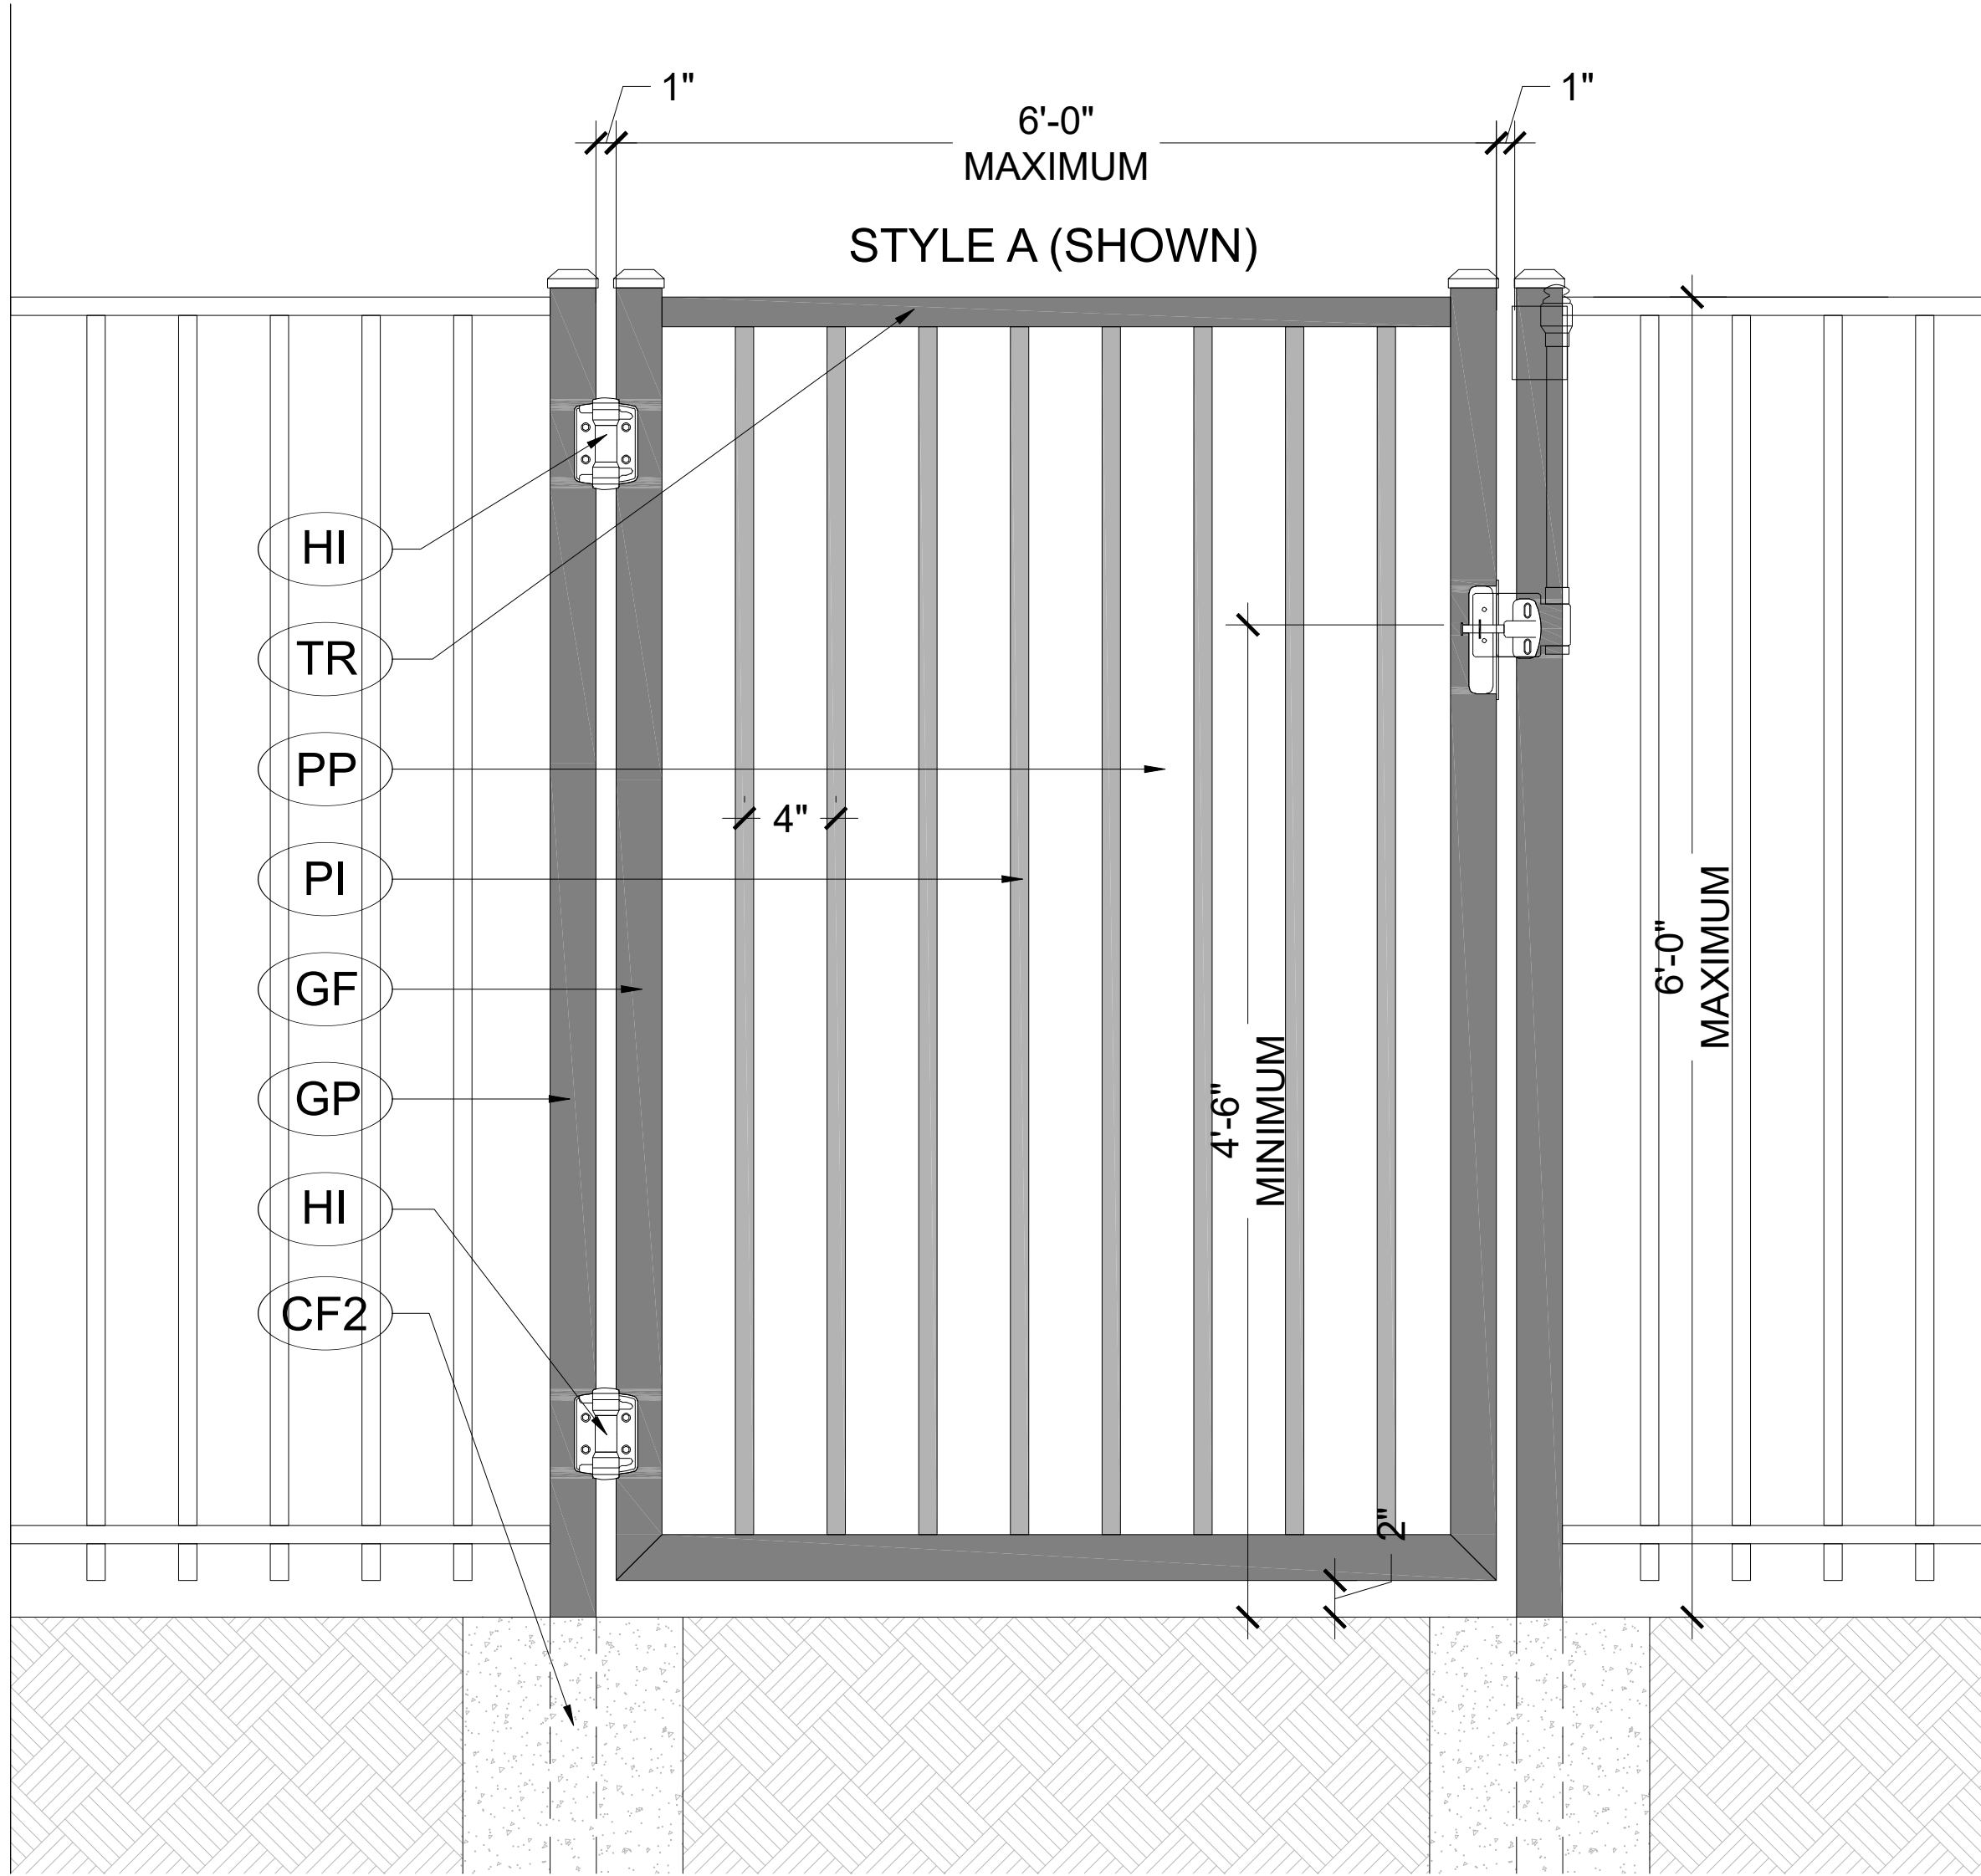

2 SINGLE SWING GATE DETAILS

SCALE: 1/2"=1'-0"

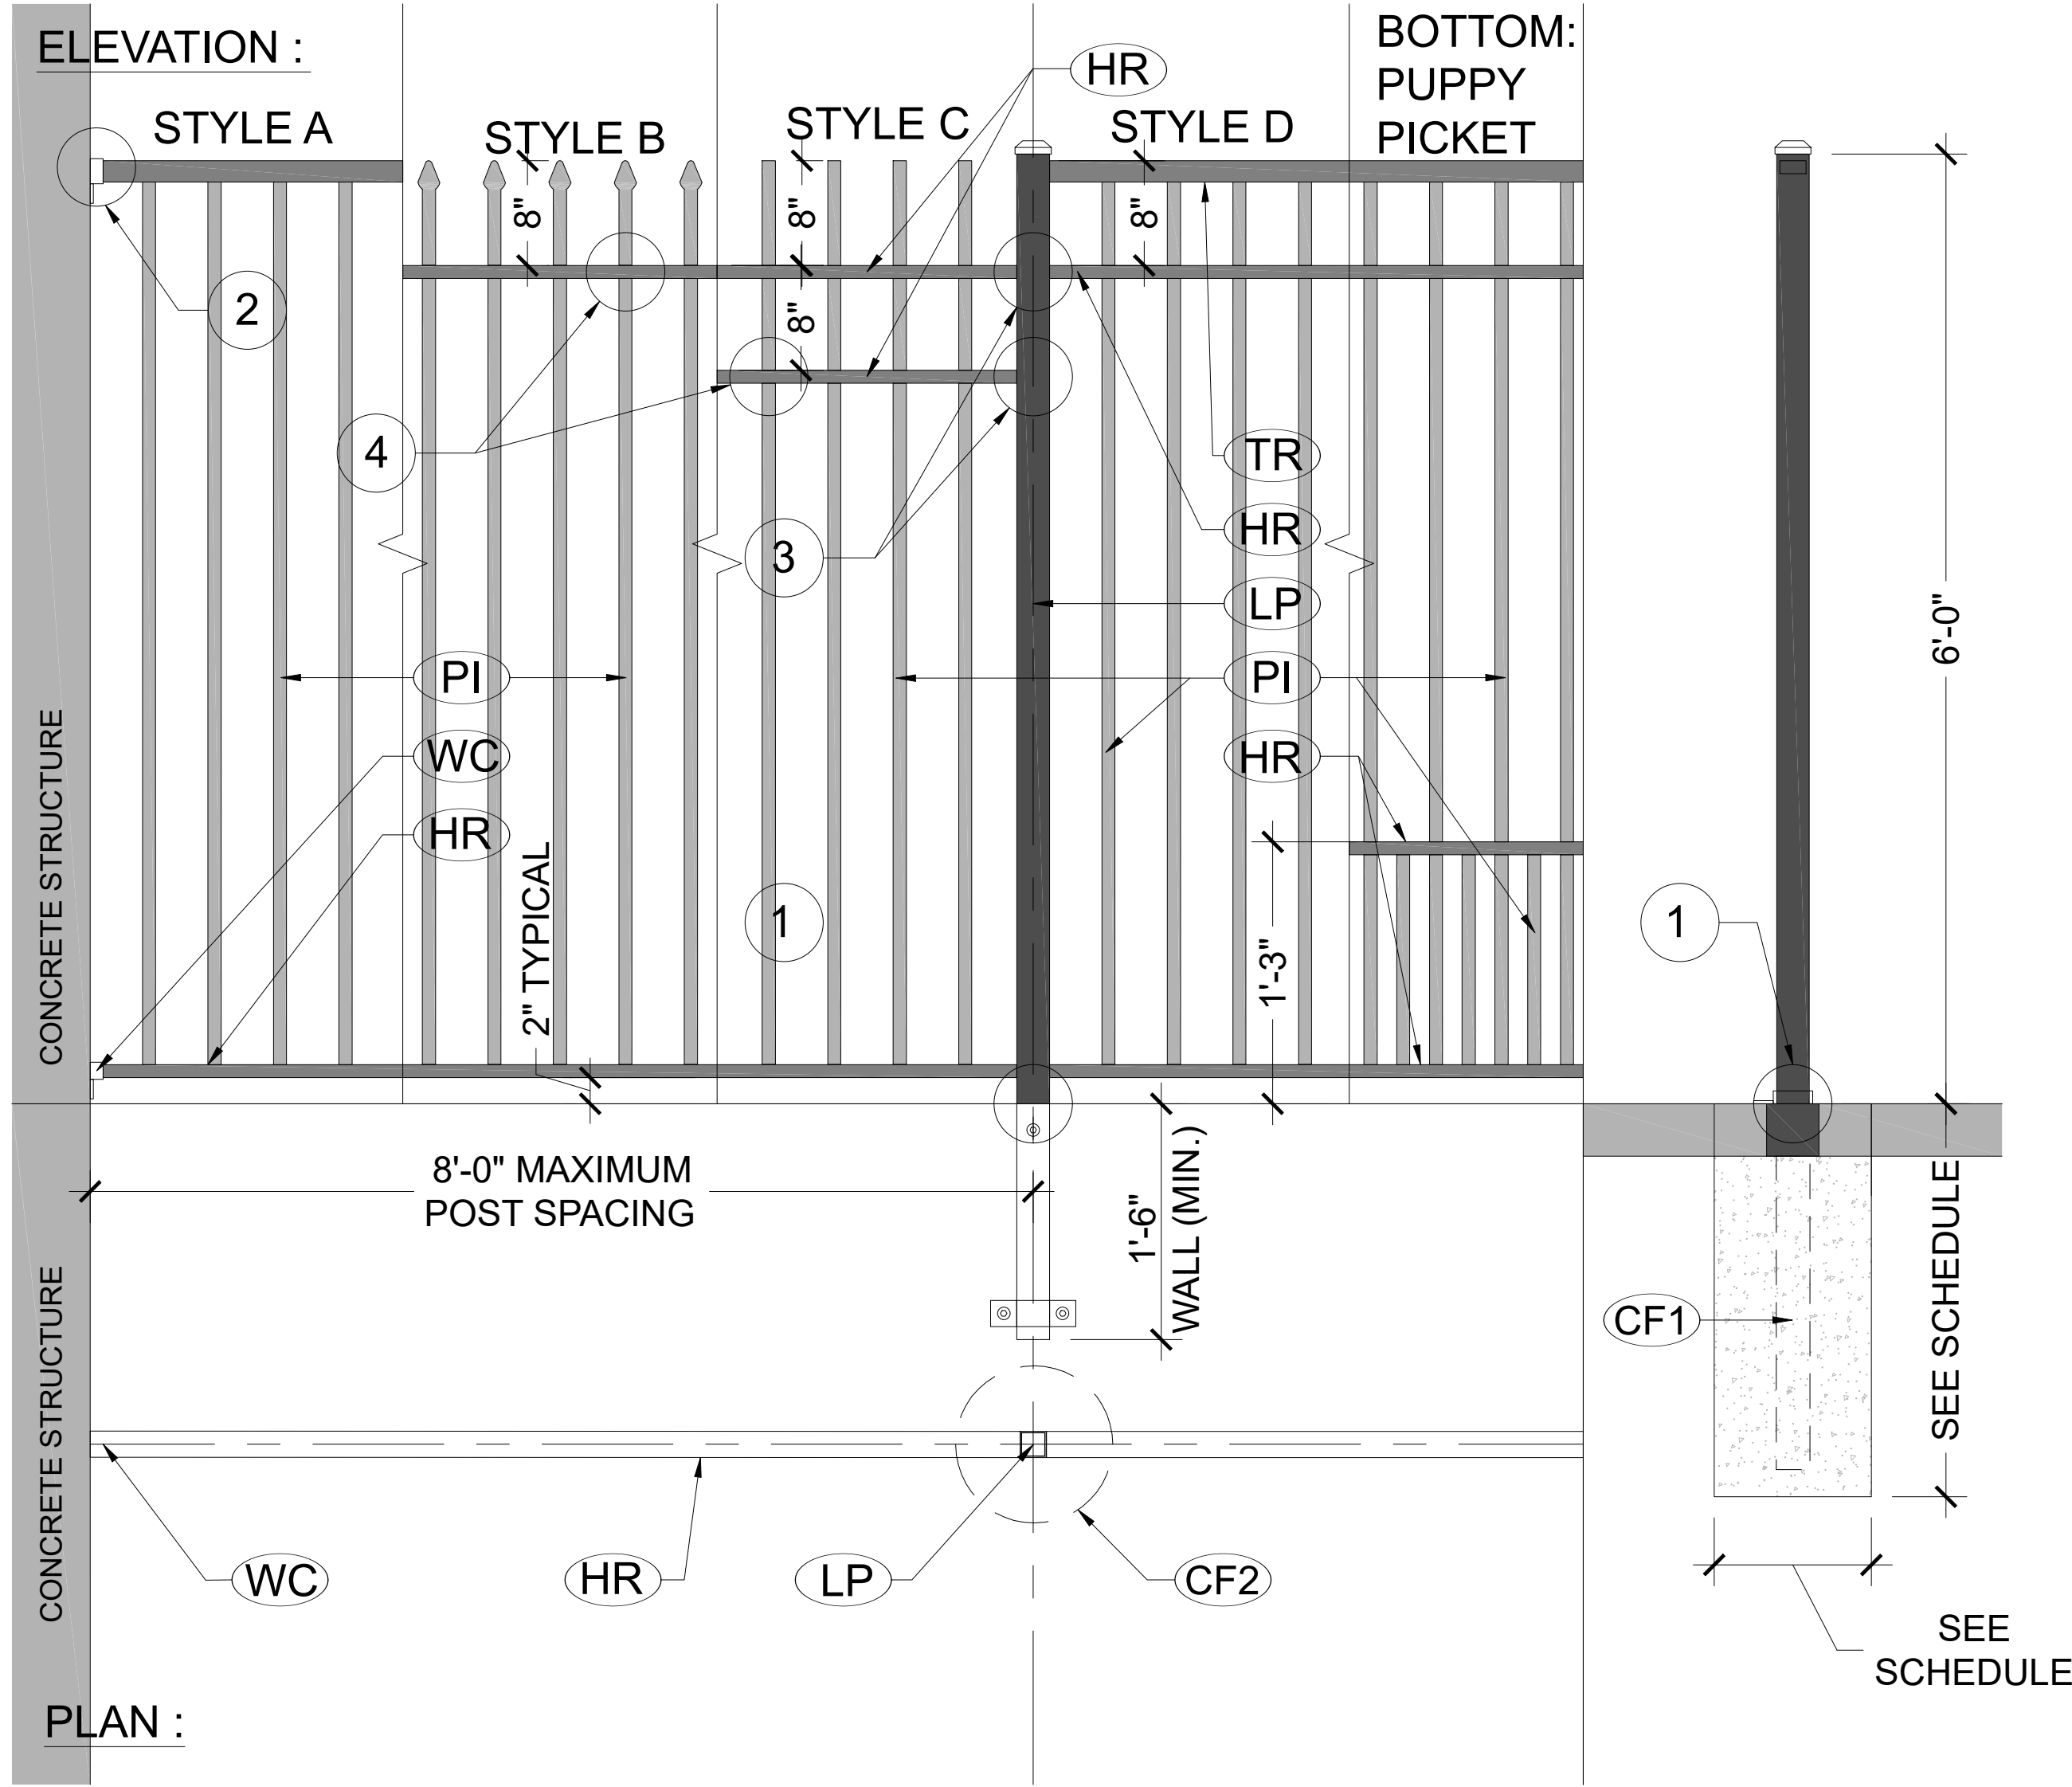

1 FENCING DETAILS

SCALE: 3/8"=1'-0"