



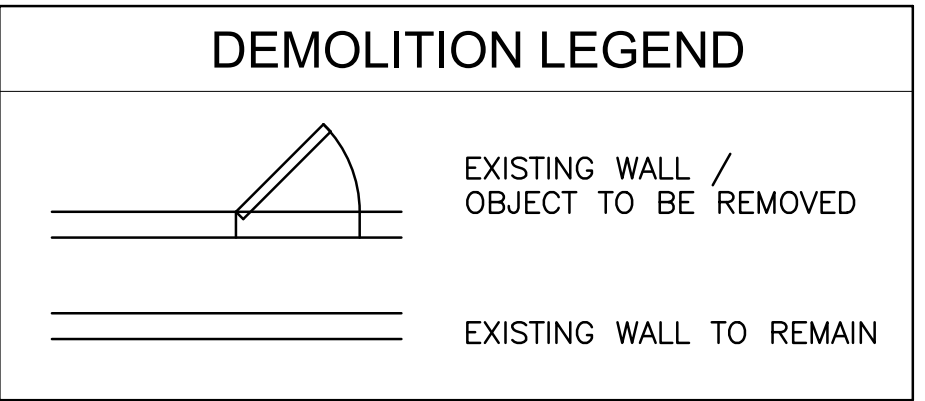

1


WINDOW SCHEDULE				
#	WIDTH	HEIGHT	DESCRIPTION	MANUFACTURER
1	3'-0"	2'-0"	NEW HORIZONTAL SLIDER	TBD BY OWNER
2	3'-0"	6'-0"	SINGLE HUNG	TBD BY OWNER
3	3'-0"	4'-0"	SINGLE HUNG	TBD BY OWNER
4	6'-0"	4'-0"	NEW HORIZONTAL SLIDER	TBD BY OWNER
5	2'-6"	4'-0"	SINGLE HUNG	TBD BY OWNER
6	4'-8"	4'-0"	NEW HORIZONTAL SLIDER	TBD BY OWNER
NOTES: 1. ALL GLAZING IN HAZARDOUS LOCATIONS DEFINED IN F.B.C. CHAPTER 24, SECTION 2406 SAFETY GLAZING INCLUDING SHOWER ENCLOSURES, WINDOWS, ETC. SHALL COMPLY WITH THE REQUIREMENTS OF THE SECTION. 2. NOT USED. 3. ALL NEW WINDOWS SHALL BE IMPACT RESISTANT. 4. CONTRACTOR SHALL VERIFY ALL WINDOW SIZES AND JAMB THICKNESS PRIOR TO ORDERING. 5. ALL OPERABLE WINDOWS SHALL HAVE SCREENS. 6. ALL WINDOWS DESIGNATED AS EGRESS SHALL MEET THE REQUIREMENTS OF F.B.C. PER SECTION R310. 7. WINDOW AND DOOR PERMIT UNDER SEPARATE PERMIT. CONTRACTOR TO PROVIDE NOAS AND WIND LOAD PRESSURES				

DOOR SCHEDULE				
#	WIDTH	HEIGHT	DESCRIPTION	MANUFACTURER
1	3'-0"	6'-8"	SOLID CORE EXTERIOR DOOR	TBD BY OWNER
2	2'-6"	6'-8"	SOLID CORE EXTERIOR DOOR	TBD BY OWNER
3	5'-0"	6'-8"	SLIDING GLASS DOOR	TBD BY OWNER
4	9'-0"	8'-0"	SLIDING GLASS DOOR	TBD BY OWNER
5	3'-6"	8'-0"	SOLID CORE EXTERIOR DOOR WITH SIDE LITES	TBD BY OWNER
6	3'-6"	6'-8"	SOLID CORE EXTERIOR DOOR WITH SIDE LITES	TBD BY OWNER
NOTES: 1. JAMB DEPTH SHALL BE VERIFIED IN FIELD. 2. NOT USED. 3. ALL DOORS TO EXTERIOR SHALL HAVE WEATHERSTIPPING, THRESHOLD AND SCREENS. 4. ALL GLAZING IN HAZARDOUS LOCATIONS DEFINED IN F.B.C. CHAPTER 24, SECTION 2406 SAFETY GLAZING INCLUDING SHOWER ENCLOSURES, WINDOWS, ETC. SHALL COMPLY WITH REQUIREMENTS OF THE SECTION. 5. ALL NEW EXTERIOR DOOR SHALL BE IMPACT RESISTANT. 6. WINDOW AND DOOR PERMIT UNDER SEPARATE PERMIT. CONTRACTOR TO PROVIDE NOAS AND WIND LOAD PRESSURES.				

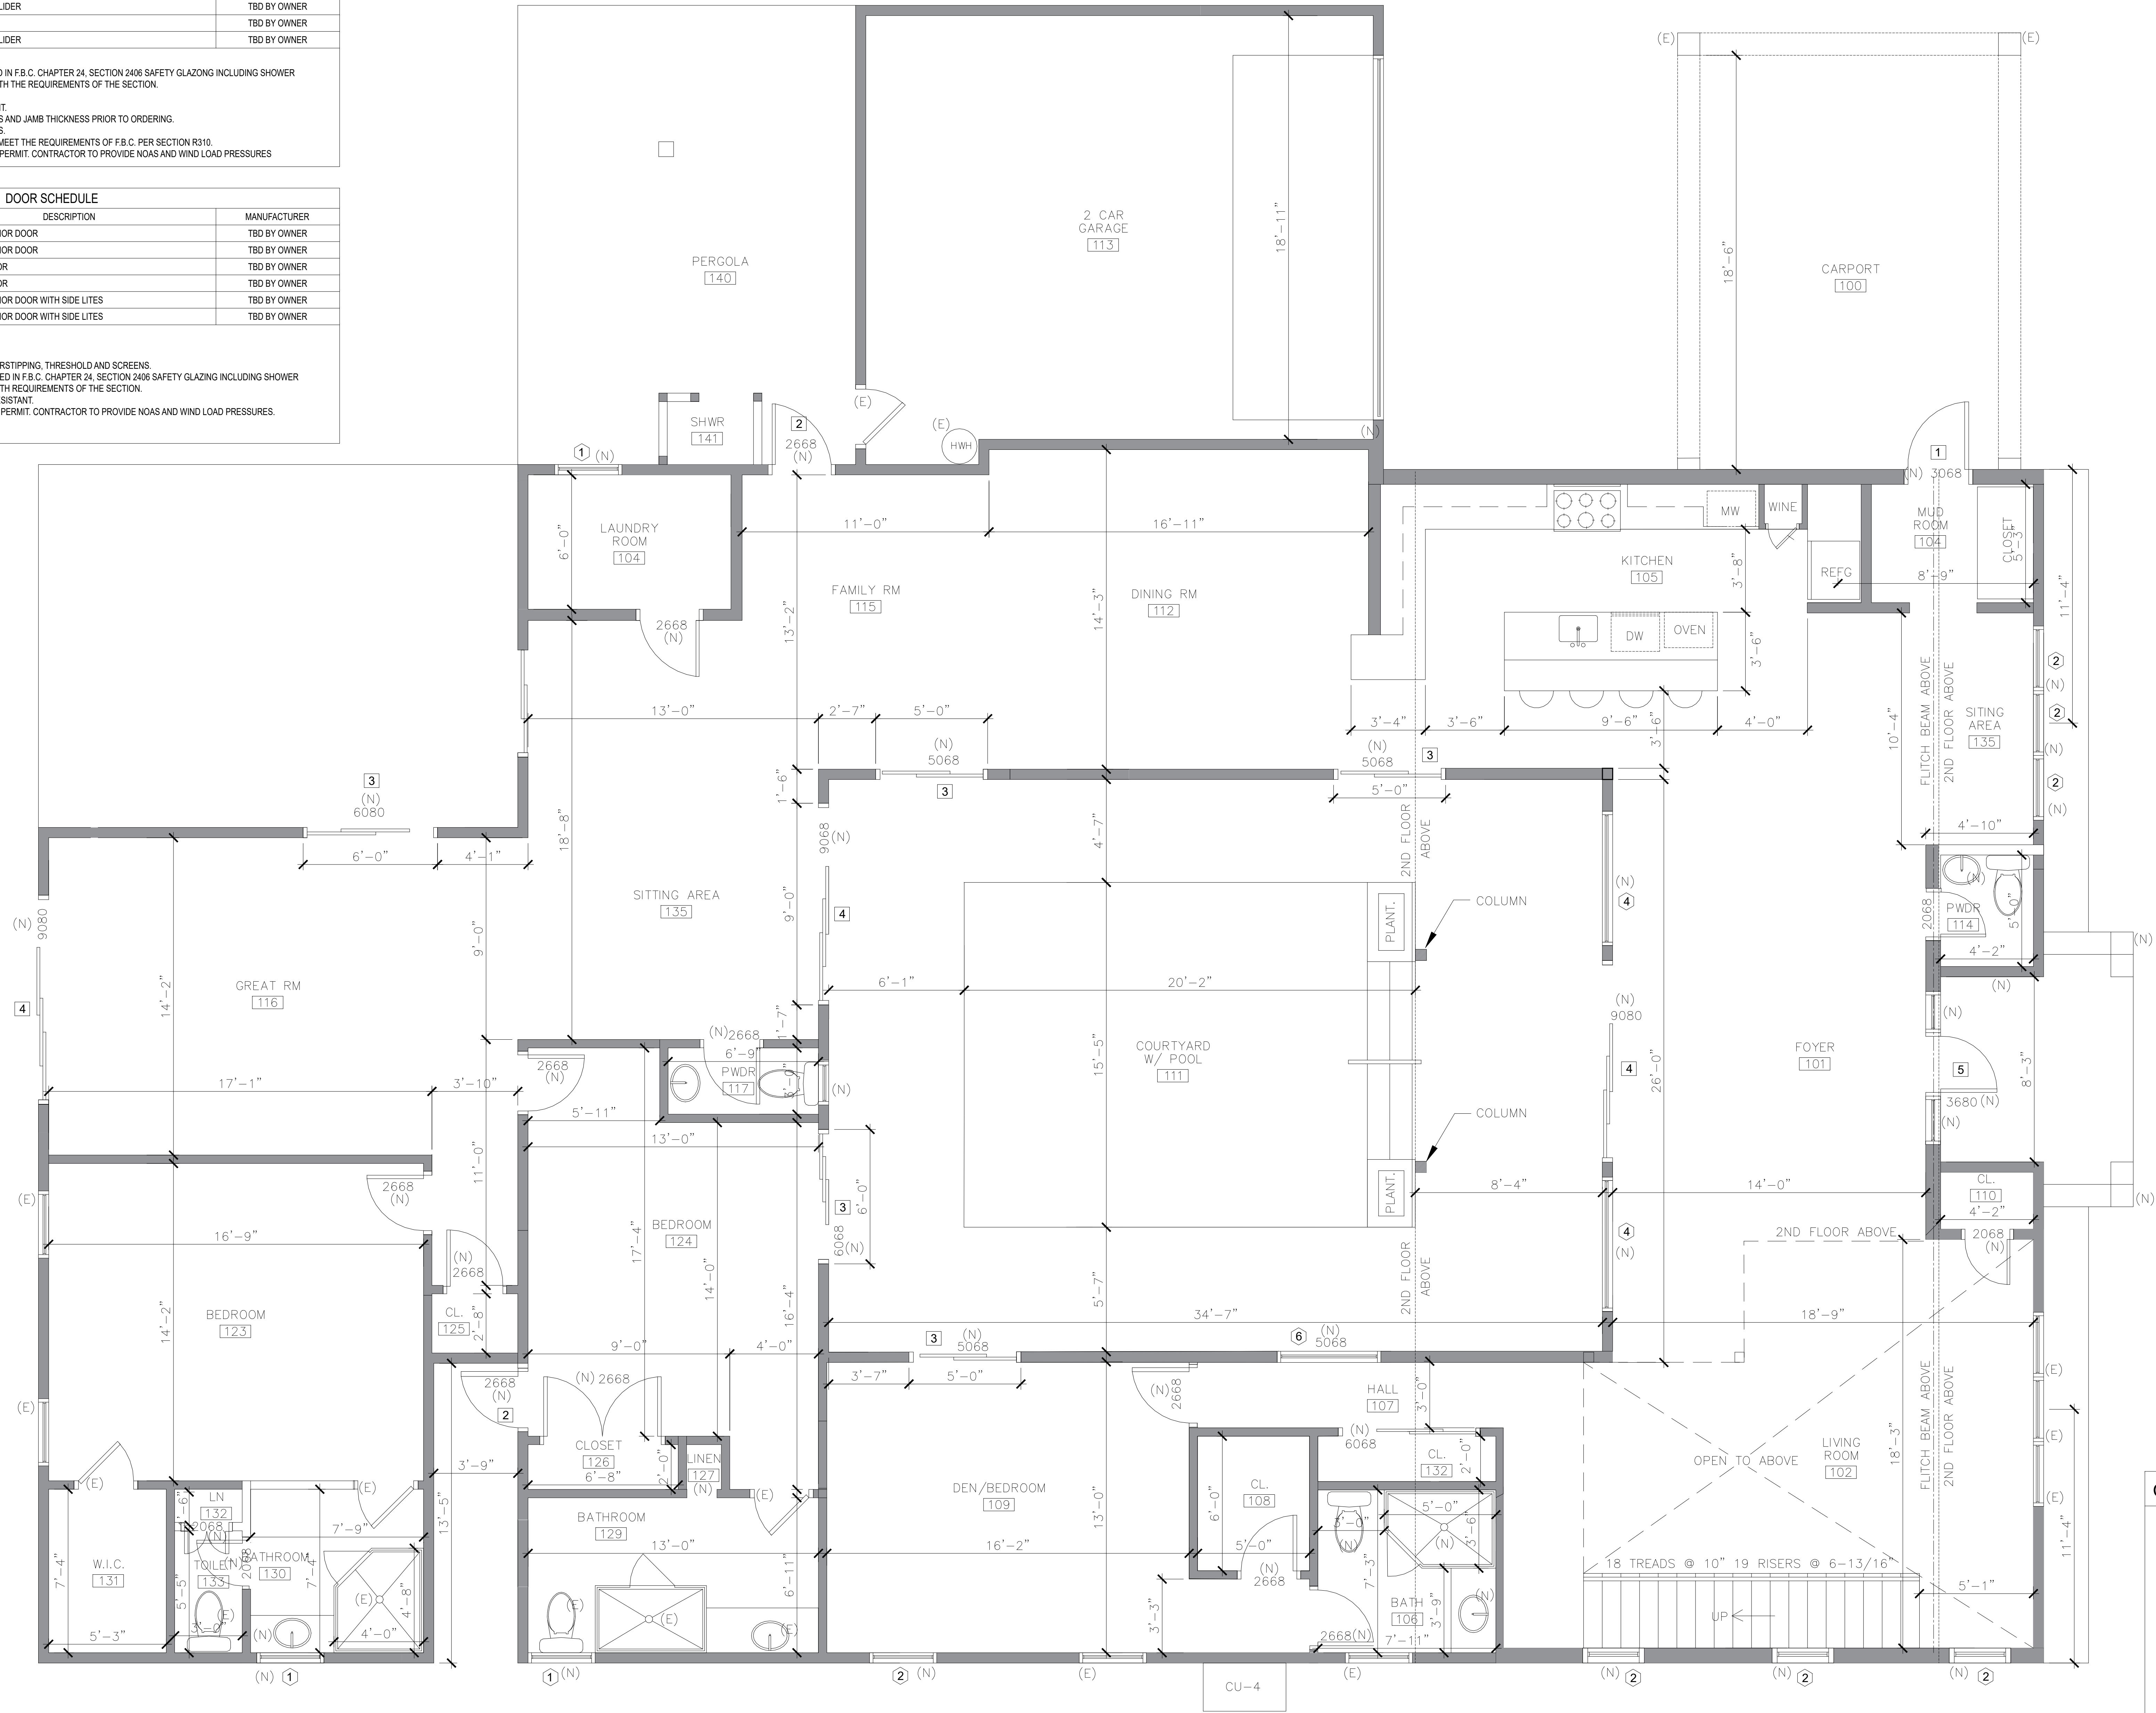


CONSTRUCTION LEGEND	
	EXISTING DOOR TO REMAIN
	NEW INTERIOR DOOR U.O.N.
	EXISTING WALL TO REMAIN
	NEW WALL: 2x4 WD STUDS @ 16" O.C. & 1/2" TYPE-X GYP. BD. BOTH SIDES
	NEW 3500 PSI 8X16 CMU WALL W/ #5 BARS @ 48" OC IN FULLY MORTARED CELLS
	SIZE OF DOOR/WINDOW (XXXXX)

1 PROPOSED FIRST FLOOR PLAN
1/4" = 1'-0"

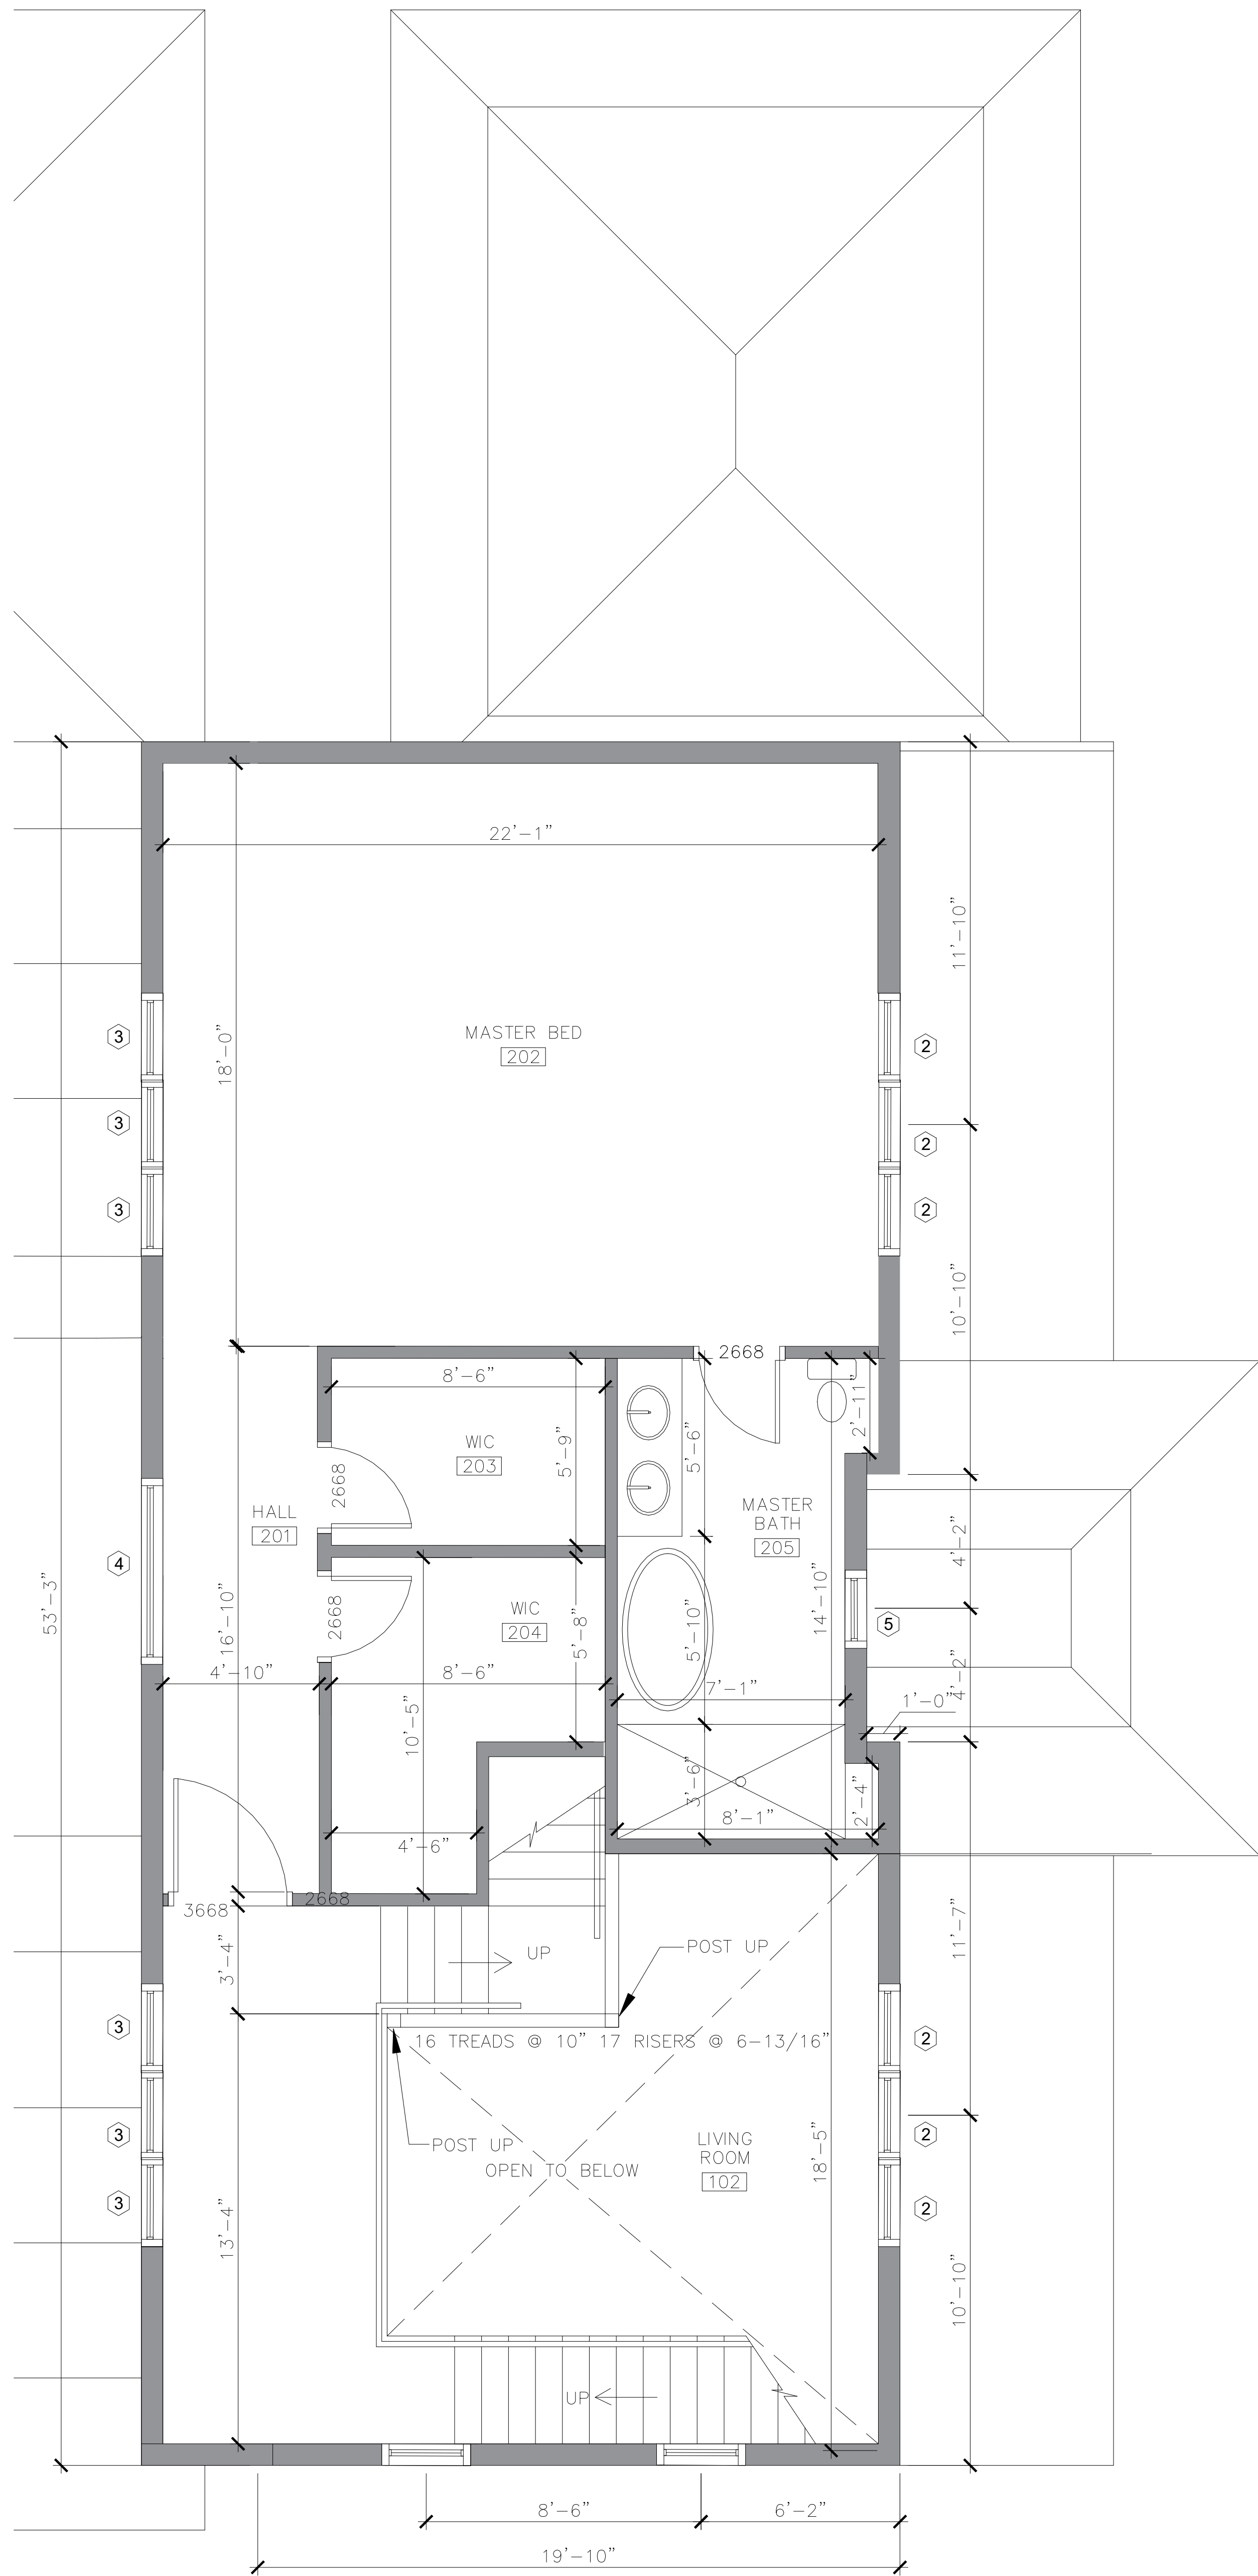


1 PROPOSED SECOND FLOOR PLAN
1/4" = 1'-0"

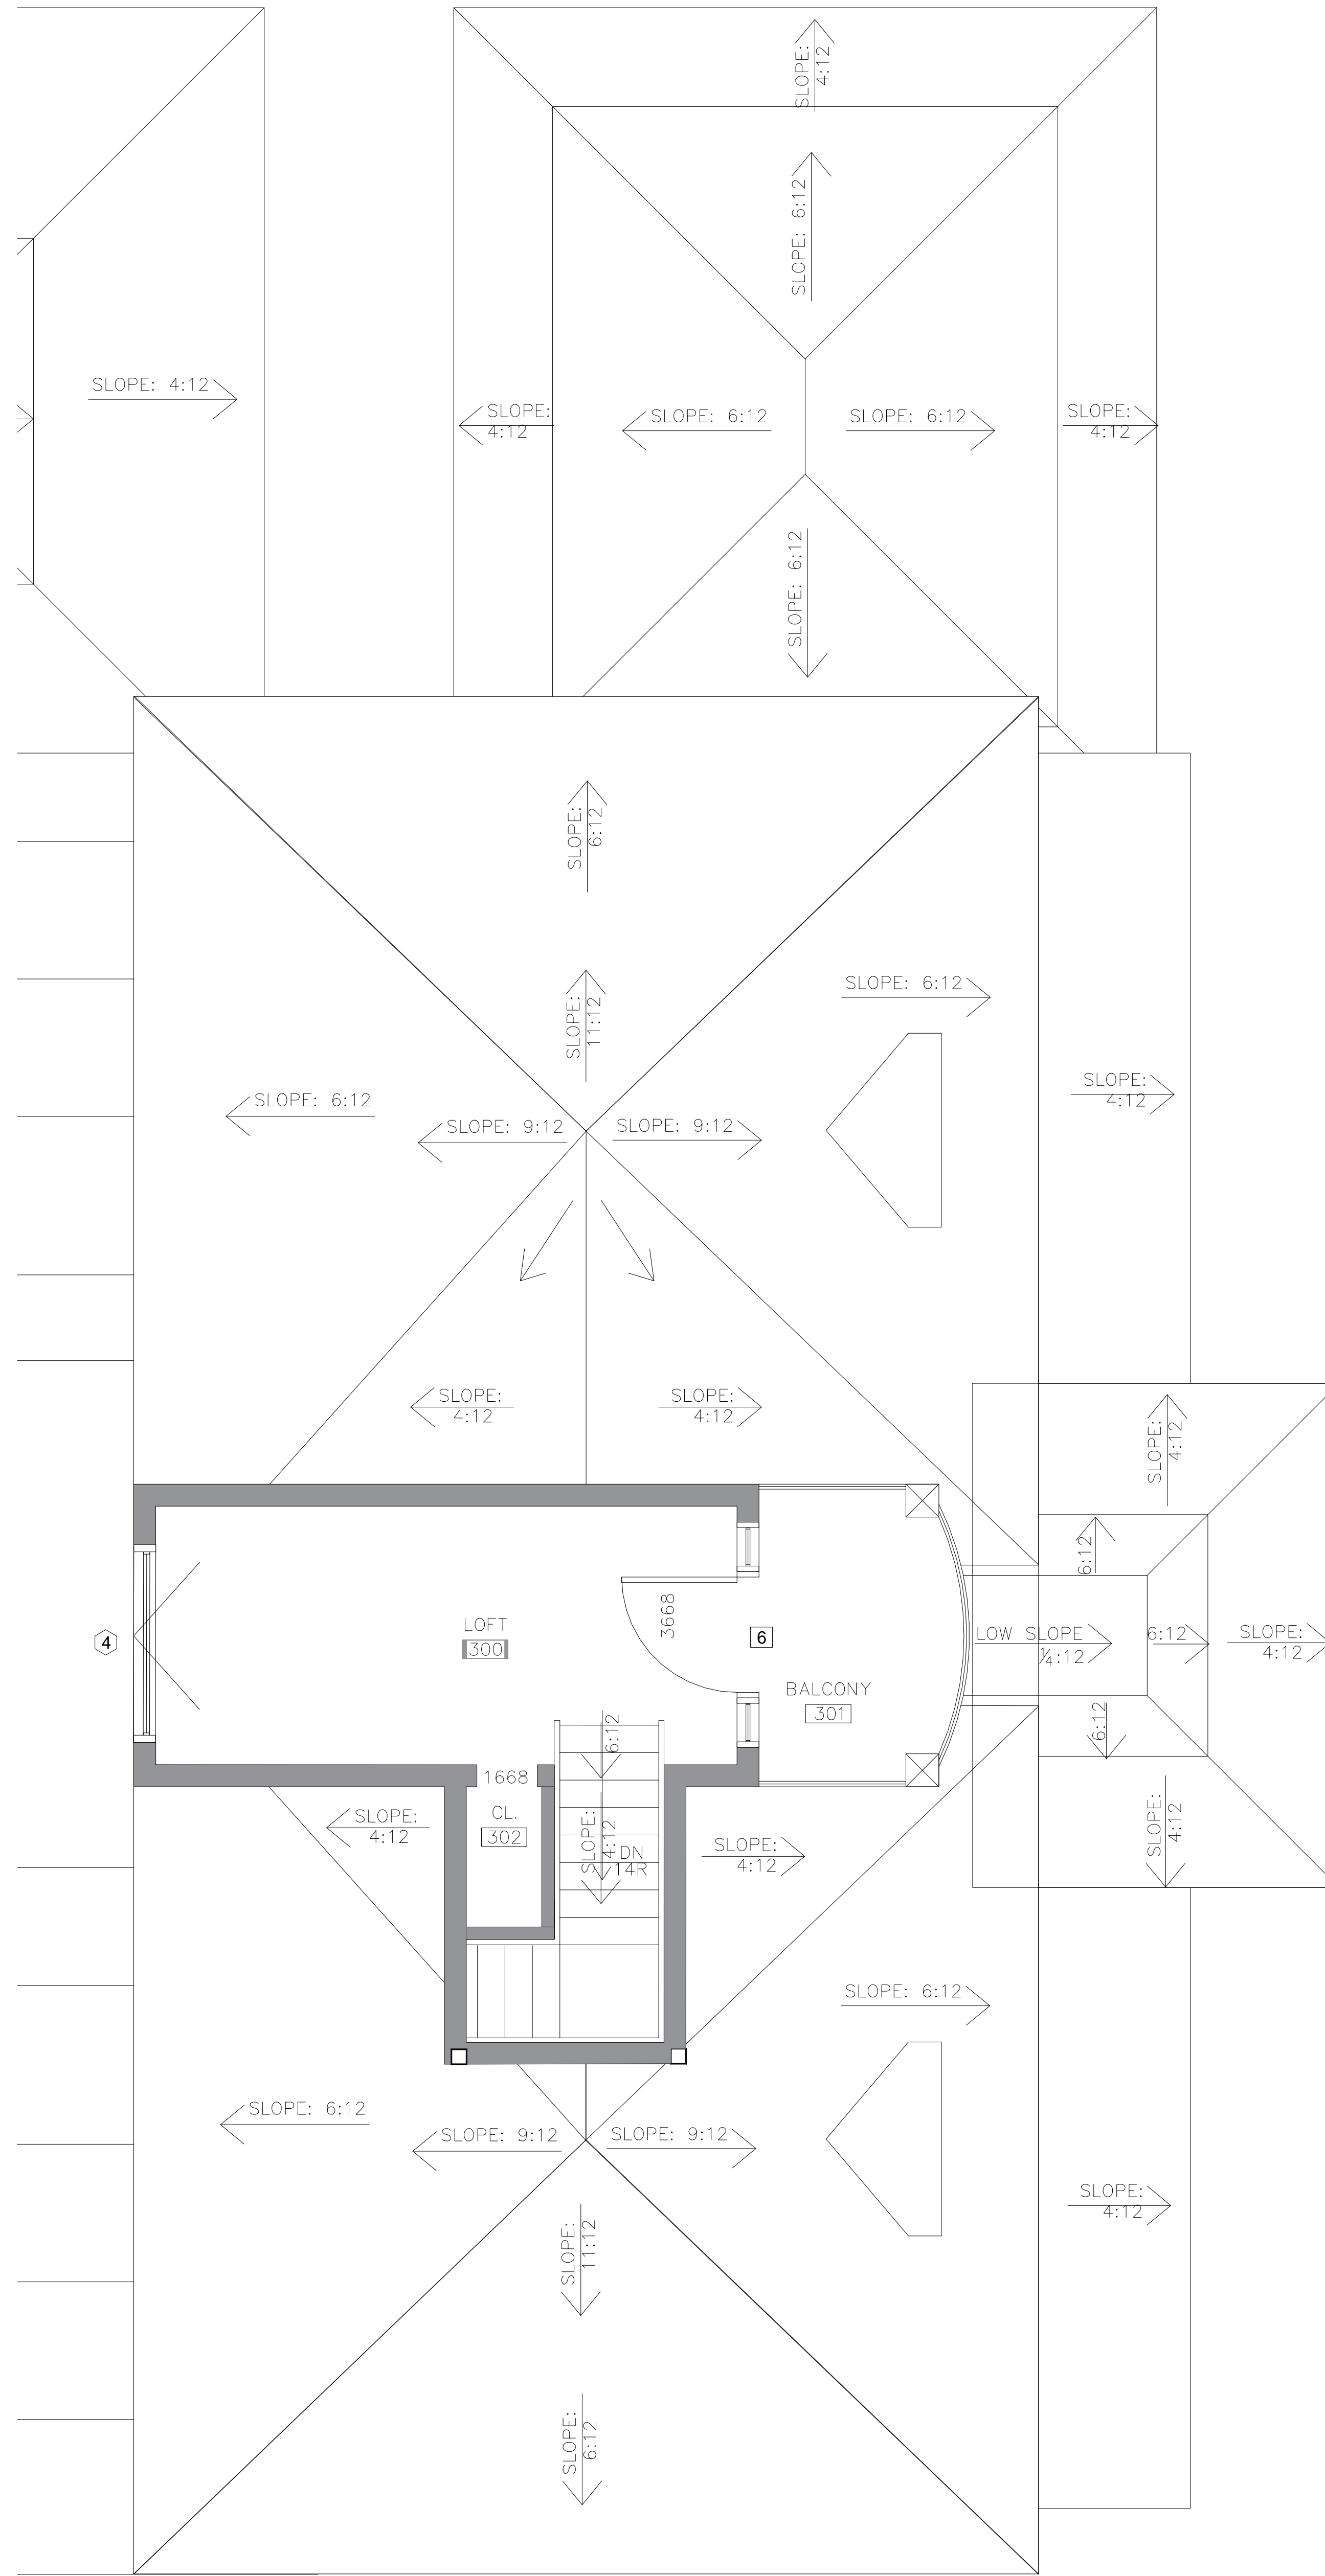


2 PROPOSED LOFT PLAN & SECOND FLOOR ROOF PLAN
1/4" = 1'-0"

WINDOW SCHEDULE				
#	WIDTH	HEIGHT	DESCRIPTION	MANUFACTURER
1	3'-0"	2'-0"	NEW HORIZONTAL SLIDER	TBD BY OWNER
2	3'-0"	6'-0"	SINGLE HUNG	TBD BY OWNER
3	3'-0"	4'-0"	SINGLE HUNG	TBD BY OWNER
4	6'-0"	4'-0"	NEW HORIZONTAL SLIDER	TBD BY OWNER
5	2'-6"	4'-0"	SINGLE HUNG	TBD BY OWNER
6	4'-8"	4'-0"	NEW HORIZONTAL SLIDER	TBD BY OWNER
NOTES: 1. ALL GLAZING IN HAZARDOUS LOCATIONS DEFINED IN F.B.C. CHAPTER 24, SECTION 2408 SAFETY GLAZING INCLUDING SHOWER ENCLOSURES, WINDOWS, ETC. SHALL COMPLY WITH THE REQUIREMENTS OF THE SECTION. 2. NOT USED. 3. ALL NEW WINDOWS SHALL BE IMPACT RESISTANT. 4. CONTRACTOR SHALL VERIFY ALL WINDOW SIZES AND JAMB THICKNESS PRIOR TO ORDERING. 5. ALL OPERABLE WINDOWS SHALL HAVE SCREENS. 6. ALL WINDOWS DESIGNATED AS EGRESS SHALL MEET THE REQUIREMENTS OF F.B.C. PER SECTION R310. 7. WINDOW AND DOOR PERMIT UNDER SEPARATE PERMIT. CONTRACTOR TO PROVIDE NCAS AND WIND LOAD PRESSURES.				


DOOR SCHEDULE				
#	WIDTH	HEIGHT	DESCRIPTION	MANUFACTURER
1	3'-0"	6'-8"	SOLID CORE EXTERIOR DOOR	TBD BY OWNER
2	2'-6"	6'-8"	SOLID CORE EXTERIOR DOOR	TBD BY OWNER
3	5'-0"	6'-8"	SLIDING GLASS DOOR	TBD BY OWNER
4	9'-0"	8'-0"	SLIDING GLASS DOOR	TBD BY OWNER
5	3'-6"	8'-0"	SOLID CORE EXTERIOR DOOR WITH SIDE LITES	TBD BY OWNER
6	3'-6"	8'-0"	SOLID CORE EXTERIOR DOOR WITH SIDE LITES	TBD BY OWNER
NOTES: 1. JAMB DEPTH SHALL BE VERIFIED IN FIELD. 2. NOT USED. 3. ALL DOORS TO EXTERIOR SHALL HAVE WEATHERSTIPPING, THRESHOLD AND SCREENS. 4. ALL GLAZING IN HAZARDOUS LOCATIONS DEFINED IN F.B.C. CHAPTER 24, SECTION 2408 SAFETY GLAZING INCLUDING SHOWER ENCLOSURES, WINDOWS, ETC. SHALL COMPLY WITH REQUIREMENTS OF THE SECTION. 5. ALL NEW EXTERIOR DOOR SHALL BE IMPACT RESISTANT. 6. WINDOW AND DOOR PERMIT UNDER SEPARATE PERMIT. CONTRACTOR TO PROVIDE NCAS AND WIND LOAD PRESSURES.				

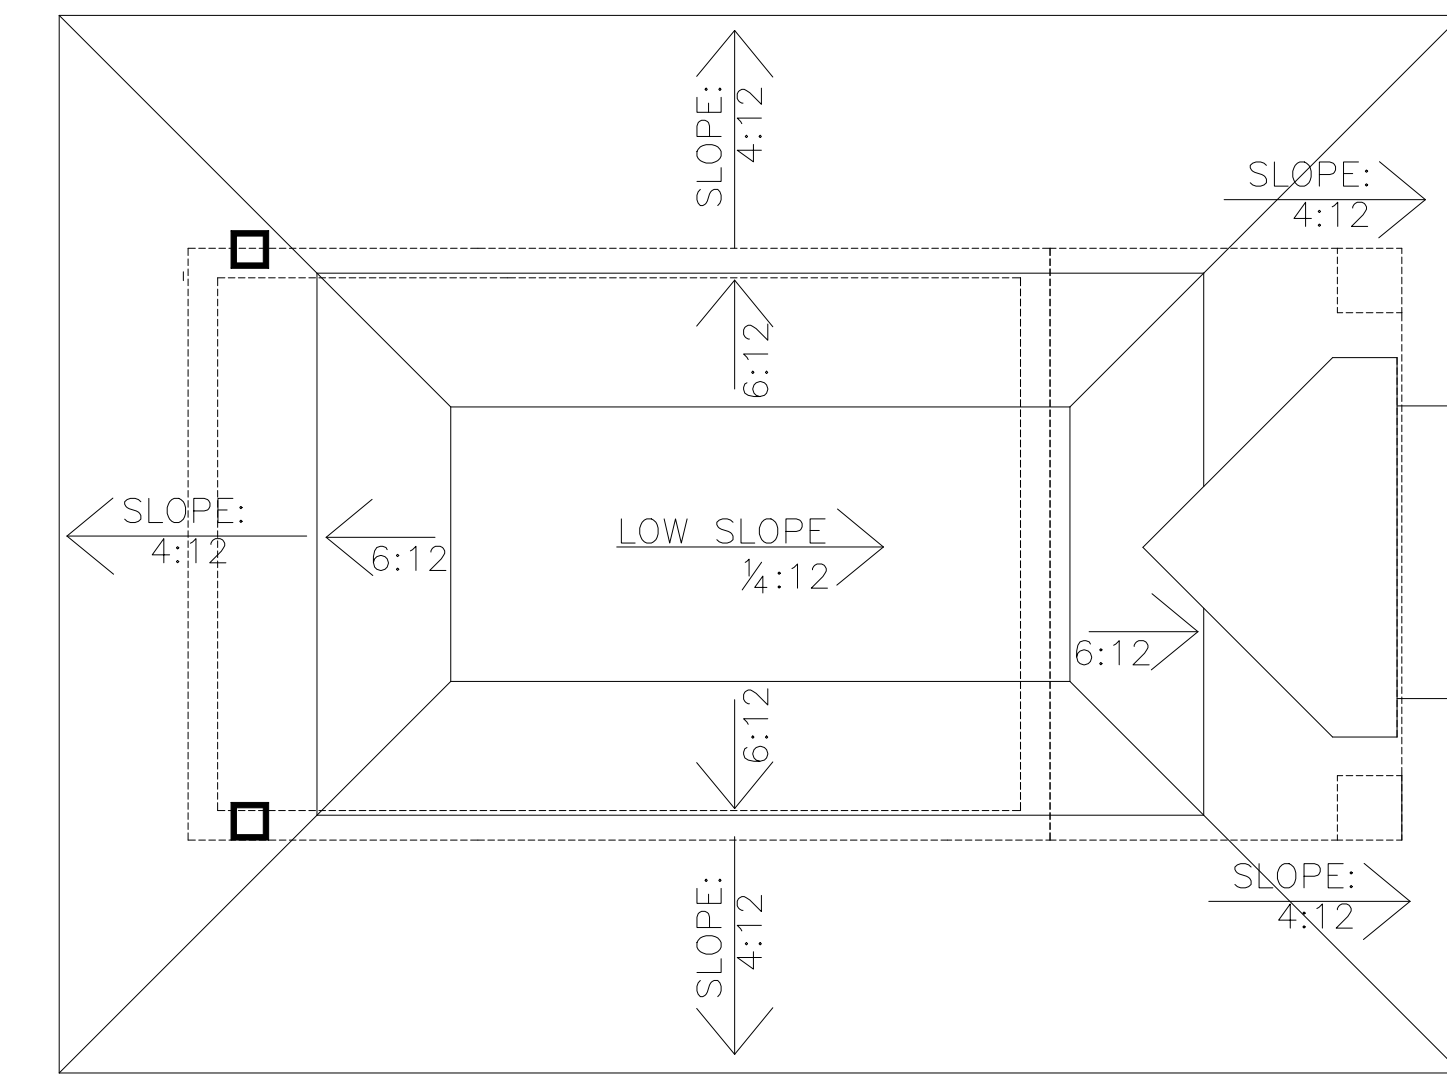


2 PROPOSED LOFT ROOF PLAN
1/4" = 1'-0"

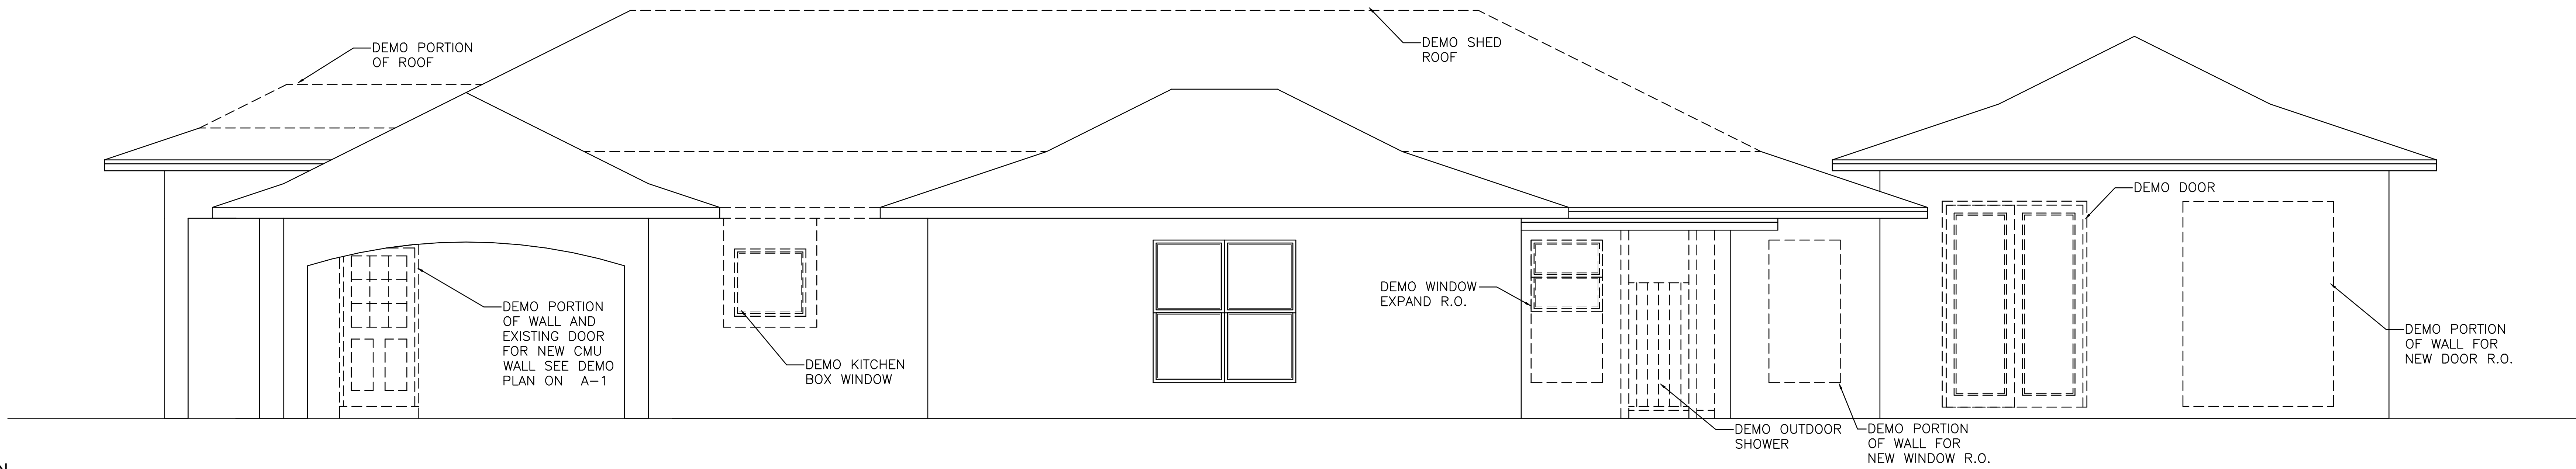


① DEMO RIGHT ELEVATION
1/4" = 1'-0"

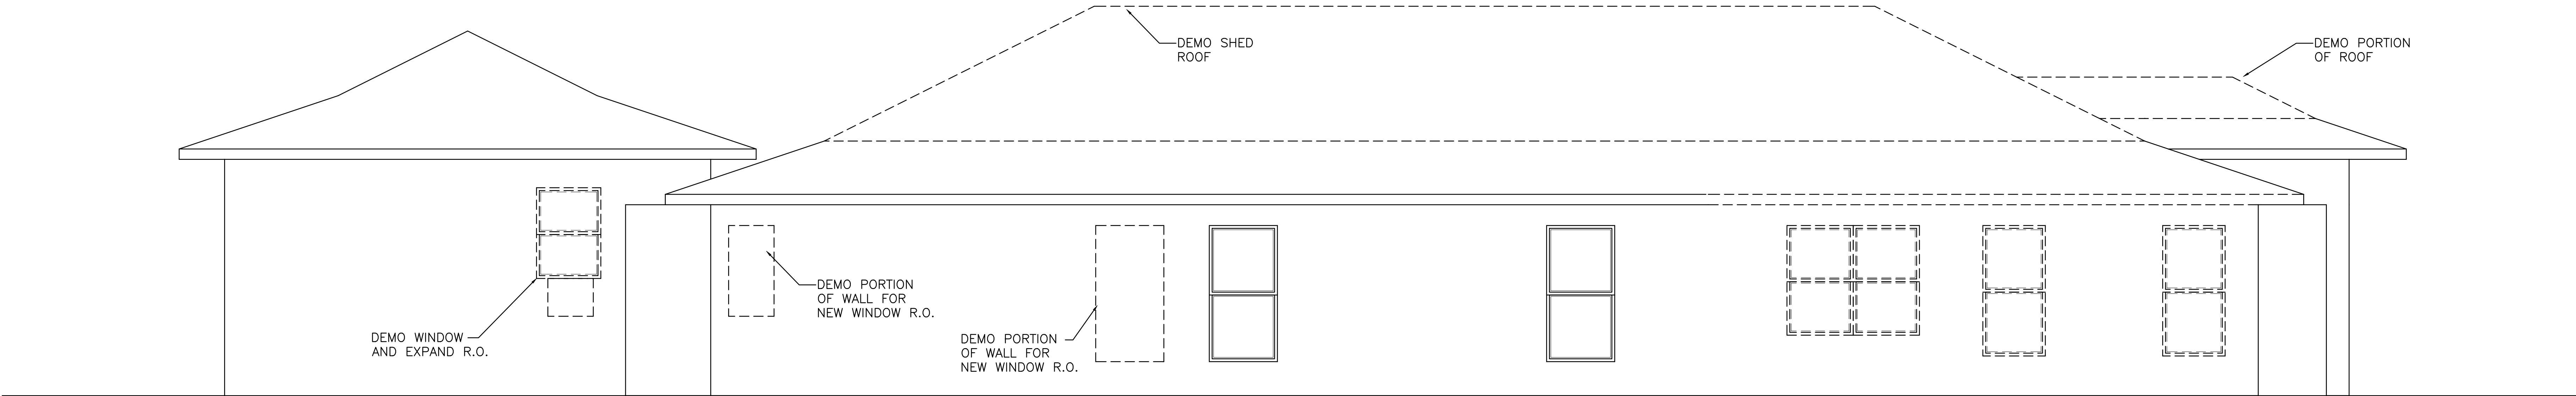

② DEMO LEFT ELEVATION
1/4" = 1'-0"

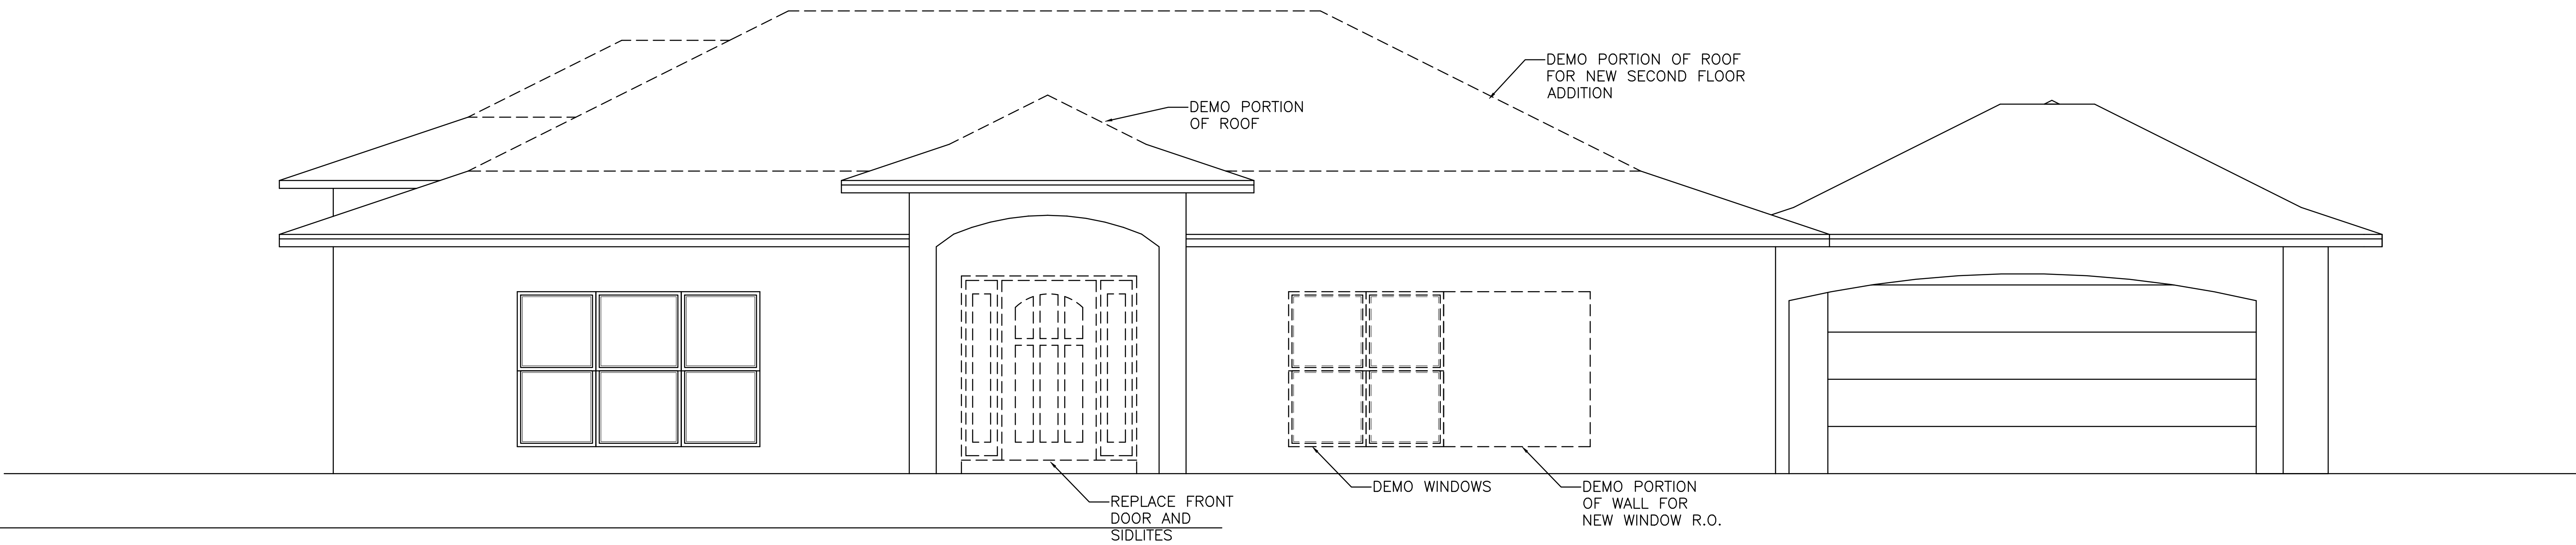


③ DEMO FRONT ELEVATION
1/4" = 1'-0"

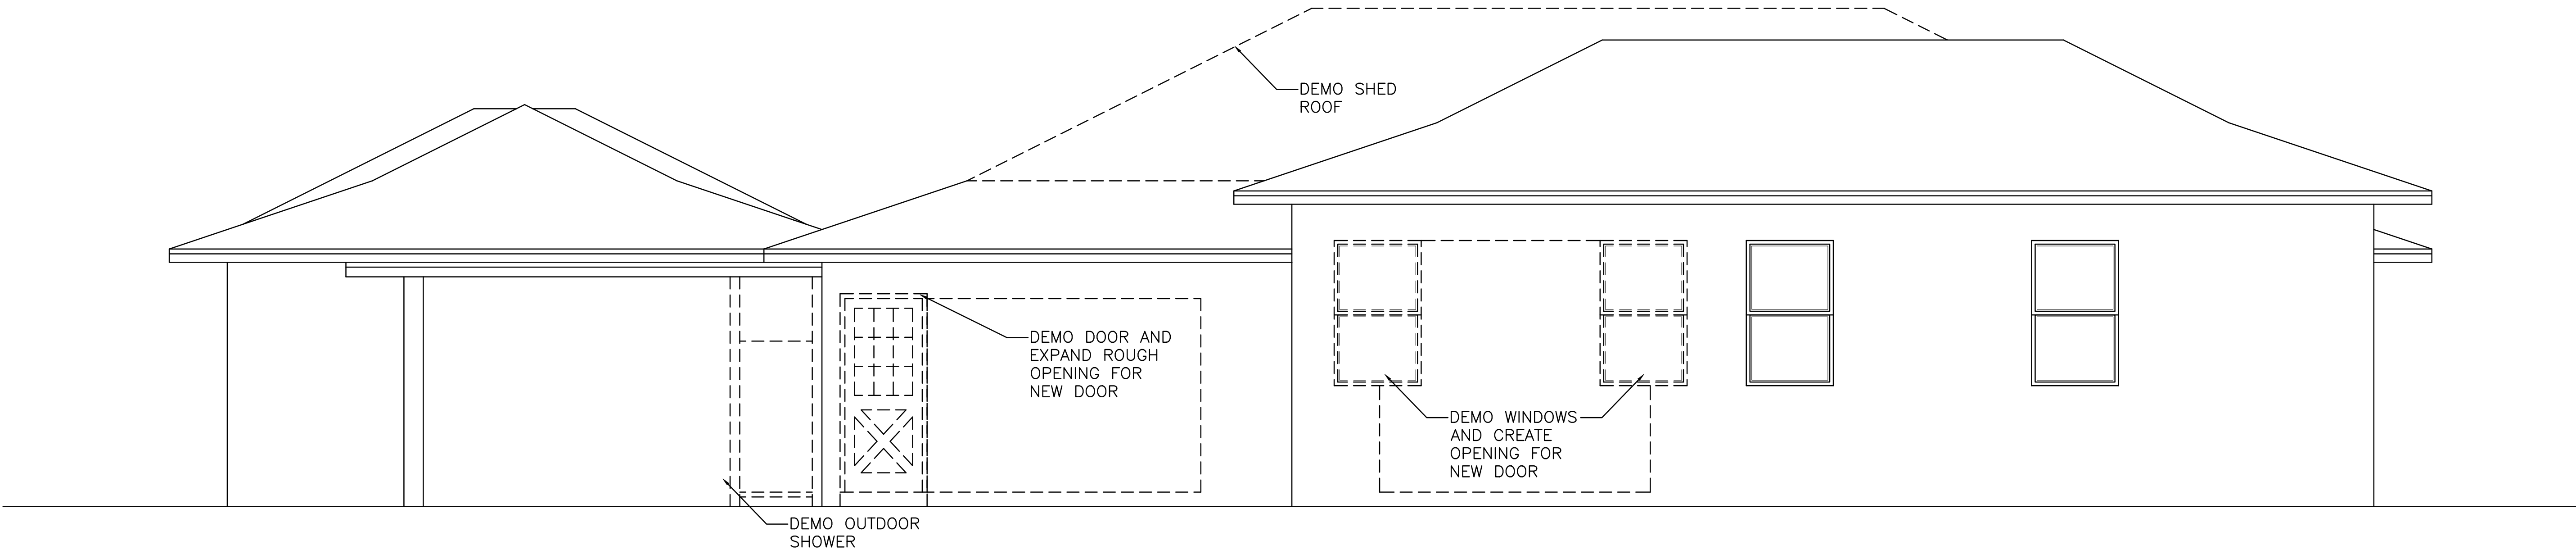


④ DEMO REAR ELEVATION
1/4" = 1'-0"

DEMOLITION LEGEND	
	EXISTING WALL / OBJECT TO BE REMOVED
	EXISTING WALL TO REMAIN

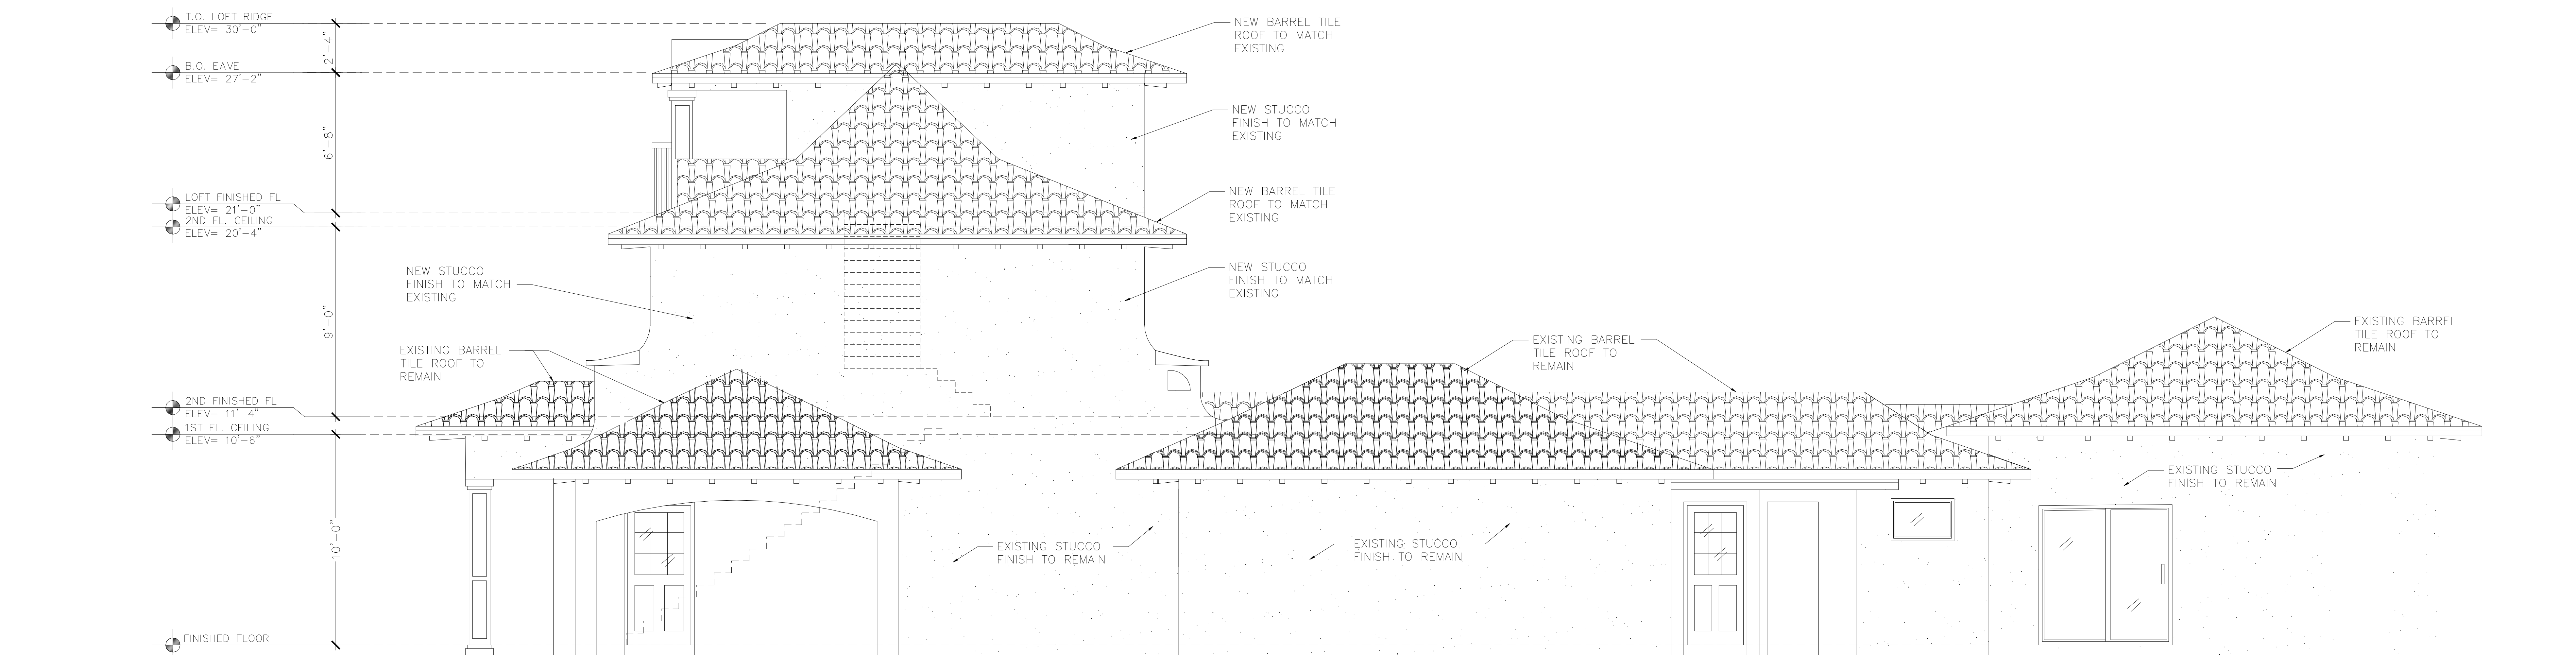


1 RIGHT ELEVATION
1/4" = 1'-0"

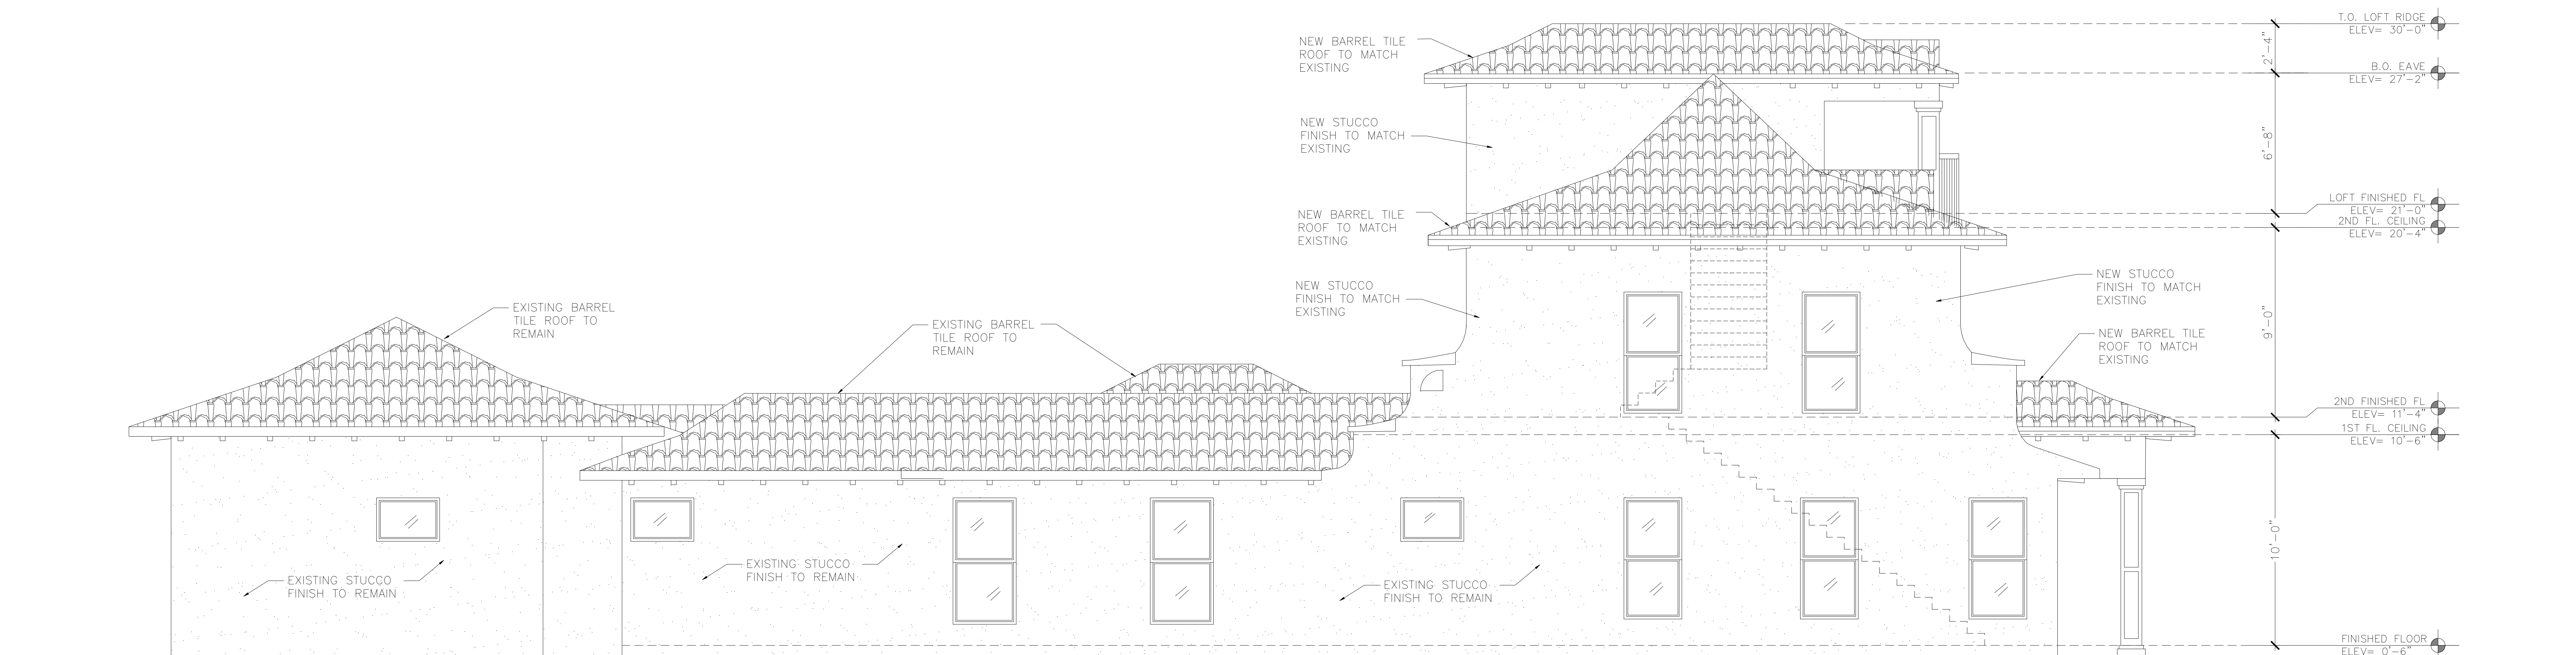

2 LEFT ELEVATION
1/4" = 1'-0"



1 RIGHT ELEVATION
1/4" = 1'-0"

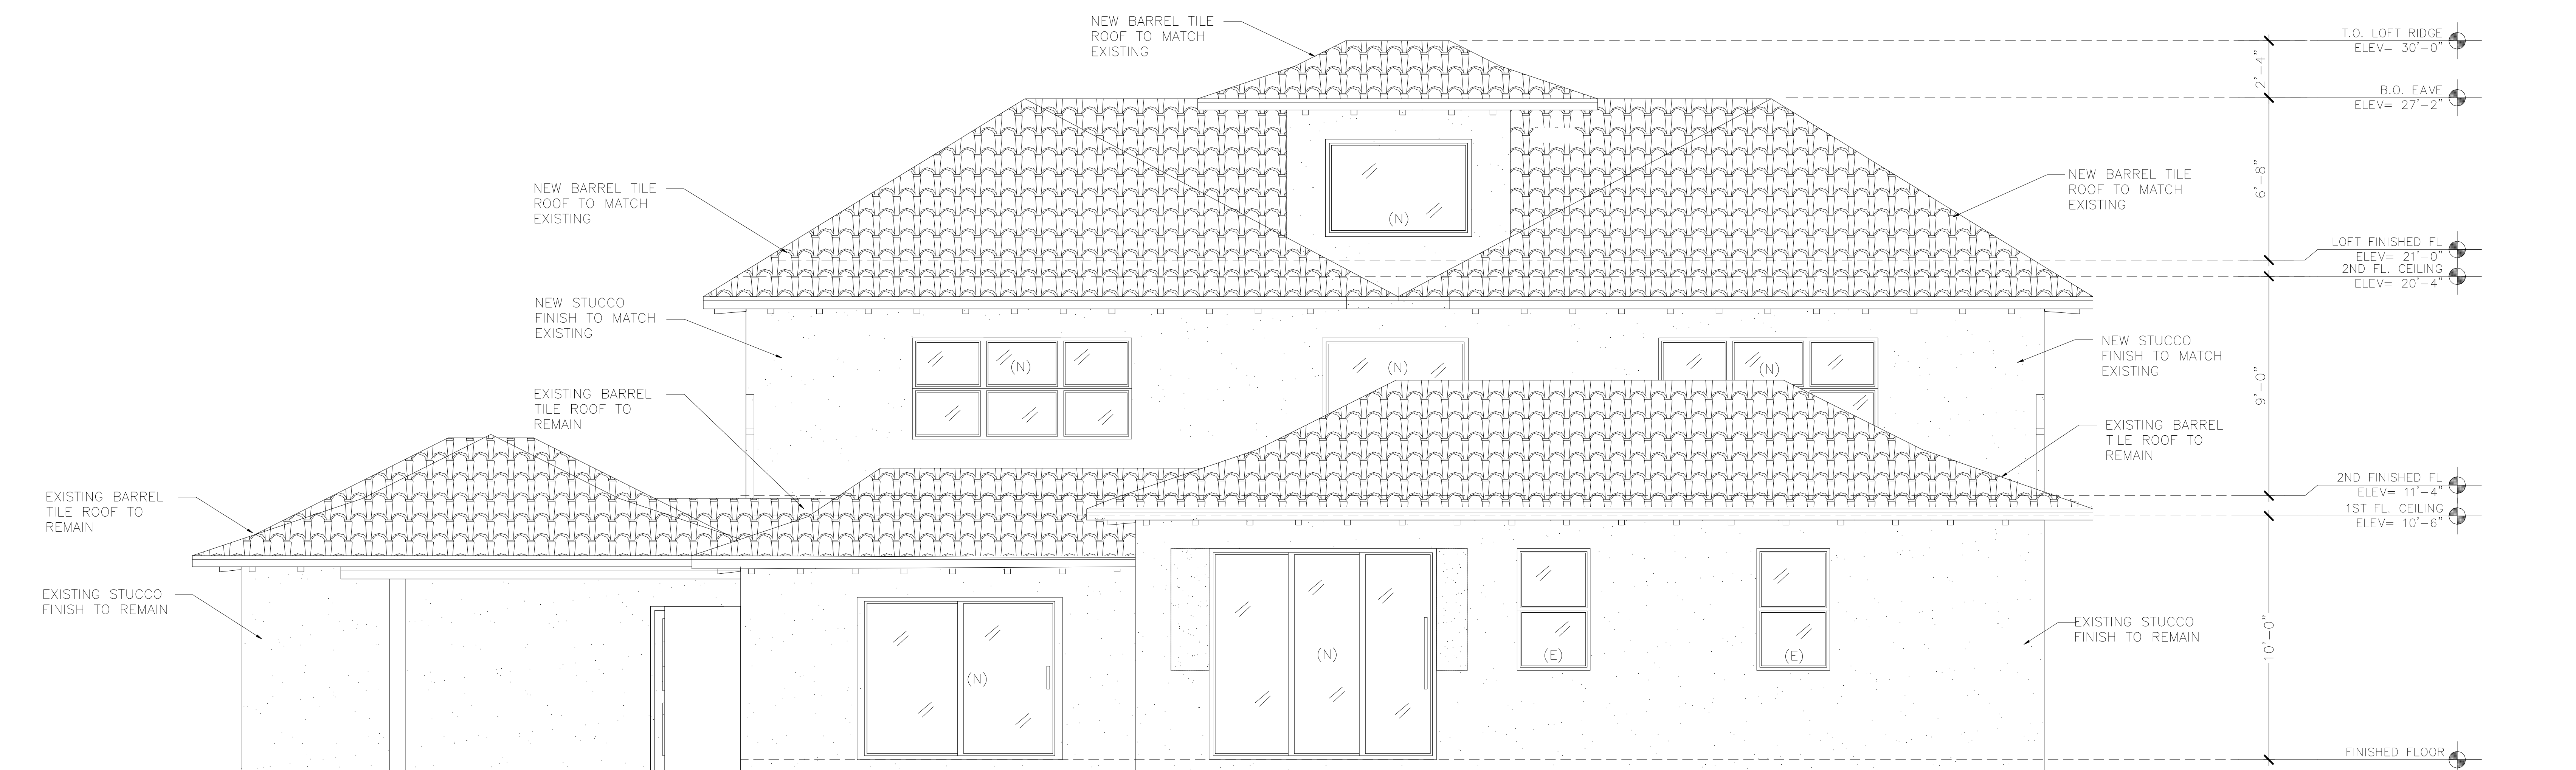

2 LEFT ELEVATION
1/4" = 1'-0"