


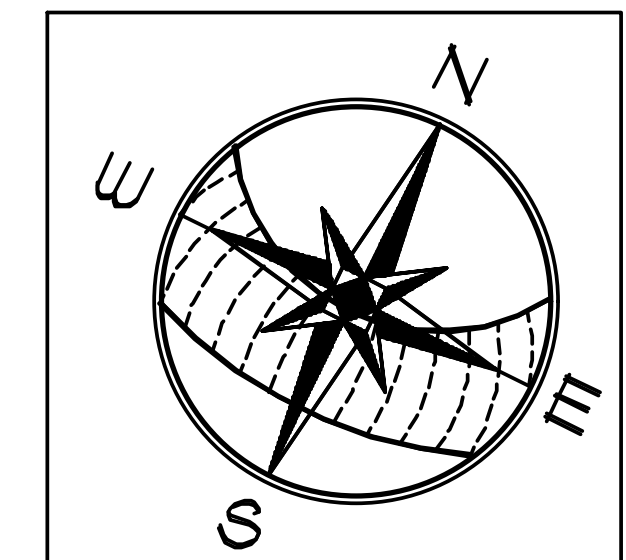


SQUARE FOOTAGE CALCCS.

HEATED AREA	SQ. FT.
LOWER FLOOR	3,313
TOTAL HEATED	3,313
NON-HEATED SF	
GARAGE(S)	643
OUTDOOR LIVING/ DINING	521
COY'D. FRONT PORCH	115
LOWER MASONRY LUG	46
TOTAL NON-HEATED	1,325
TOTAL HTD. & NON-HTD.	4,641

SPECIAL CONSTRUCTION NOTES

- ELEC. WATER HEATER ON RAISED PLATFORM. PROV. FOR PLUMB, GAS, ELEC. WATER, HARDWARE, AND PAN & DRAIN LINES AS REQ'D. INSTALL PER CODE AND MANUF. SPECS. VERIFY LOCATIONS & # OF UNITS WITH BUILDER PRIOR TO INSTALLATION.
- HVAC UNIT IN ATTIC. PROVIDE HARDWARE, FLUE, PAN & DRAIN LINES AS REQ'D. 3/4" FLUOD DECKING FROM ACCESS TO UNIT.
- REVERSED LIGHT COVE @ CEILING. REF. TO INTERIOR ELEVATIONS.
- 48" METAL FF. INSTALL PER MANUF. SPECS. PROV. GAS, & ELEC. VENT AS REQ'D. PER MANUF. SPECS. 20" DEEP FLUSH HEARTH/ SCORED CONC. EDGE FOR DEFINITION.
- 4" MASONRY VENEER AT INTERIOR WALL. MASONRY TO MATCH EXTERIOR WALL OR PER INTERIOR DESIGNER/OWNER SELECTION.
- SLOPE CONC. AS REQ'D. TO DRAIN WATER. (BUILDER TO ACCOUNT FOR 1 1/2" (MIN) DROP FROM FF. TO EXTERIOR FINISHED SURFACE.
- 36"X12" TUB PER SPECS. PROV. ELEC. CONNECTION & GROUND FOR MOTOR AS REQ'D. PROVIDE ACCESS PANEL WITHIN REACH OF MOTOR.
- CUSTOM TILE SHOWER. WATERPROOF SHOWER BASE PER BUILDER SPECS. SLOPE TILE TO CENTER DRAIN. 22" HT. TILE SEAT. SLOPE SEAT TO DRAIN WATER.
- 20"X20" DROPPED SLAB UNDER WASHER. SLOPE TILE TO DRAIN.

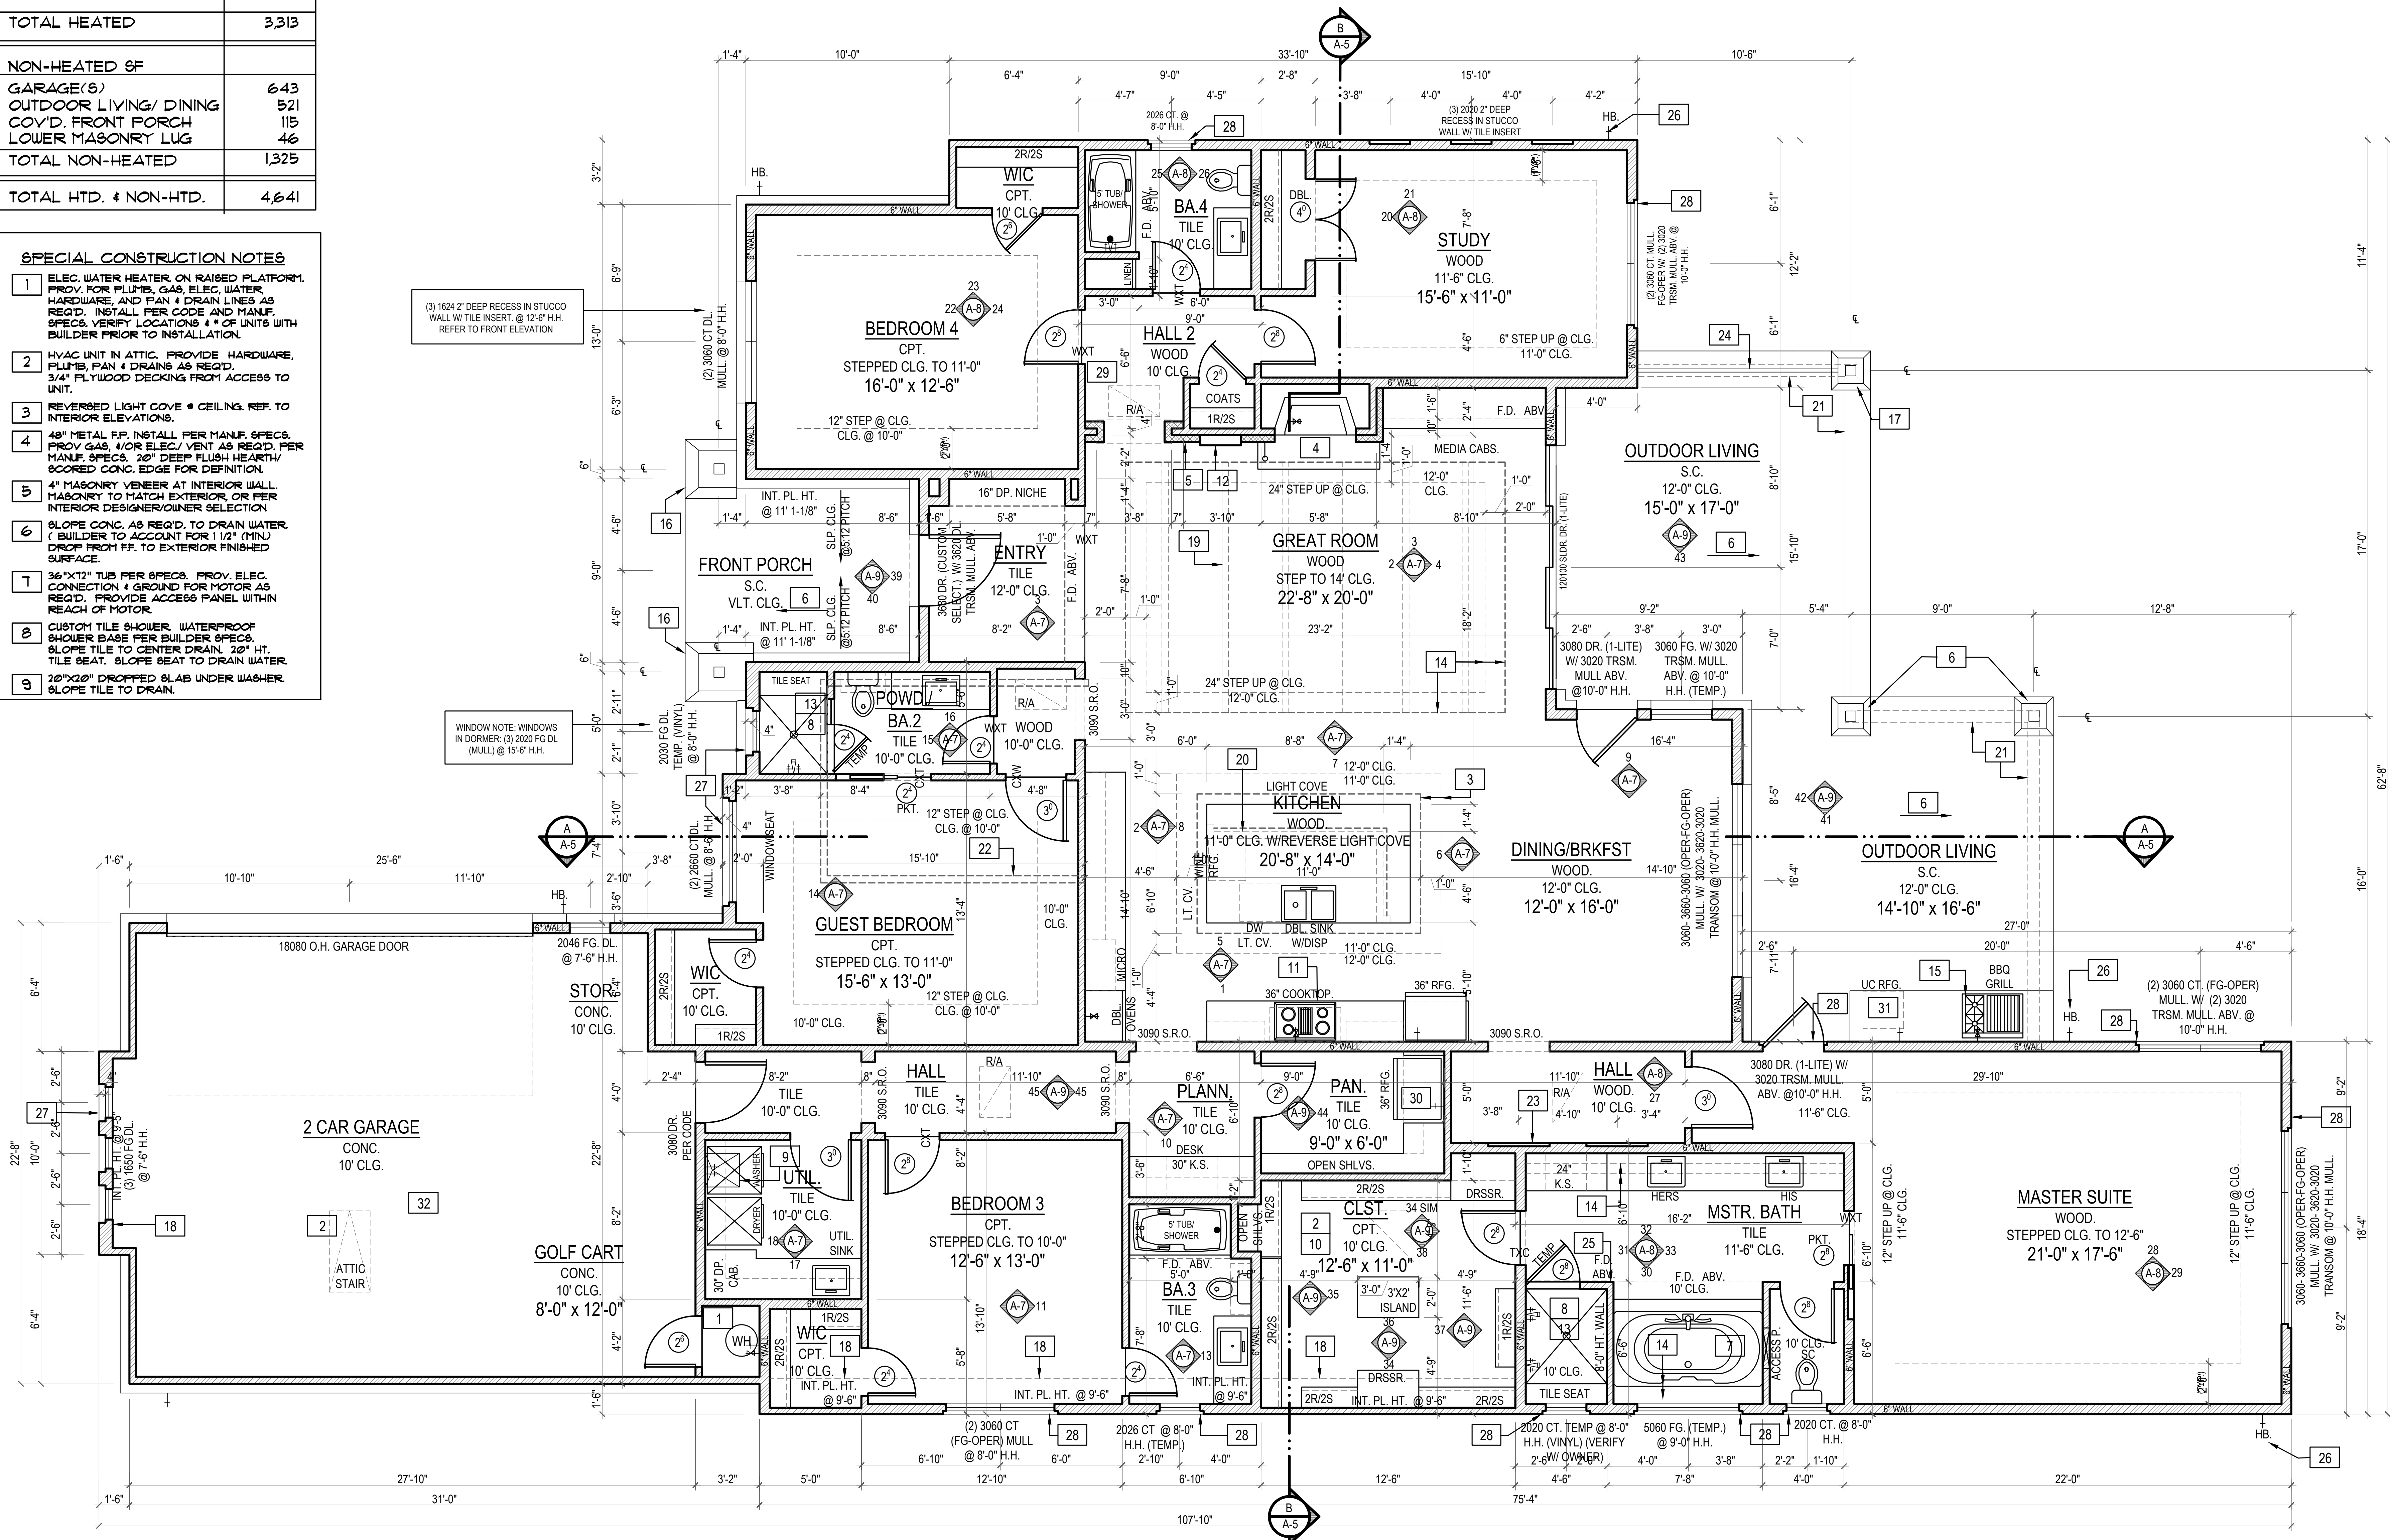

OWNER:
LINDSAY & BLAKE TAYLOR
XXXX XXXXX VIEW LN.
XXXX, TEXAS 71024
T:XXXX XXX-XXXX


BUILDER:
XXXX XXXXX
XXXXX CUSTOM HOMES
2303 RR620 SOUTH, SUITE 135-212
AUSTIN, TEXAS 78134
T:XXXX XXX XXXX

ARCHITECT:
KAI GESCHKE
GESCHKE GROUP ARCHITECTURE
11200 RANCH RD. 2222
AUSTIN, TEXAS 78130
T:512/ 502 8484

ENGINEER:
XXXX XXXXXXX
XXXXX ENGINEERING, LLC
1120 COTTONWOOD CREEK TRAIL
CEDAR PARK, TEXAS 78613
T:XXXX XXX-XXXX

- 30" X 30" ATTIC ACCESS SCUTILE.
- VENTHOOD DESIGN PER OWNER AND/OR INT. DESIGNER. VENT-LINER PER SPECS. PROVIDE ELEC. AS REQ'D.
- 24"X34"X6" DEEP WOOD LEDGES PER INT. ELEV.
- TEMP. GLASS ENCLOSURE ON 36" HT. LOW WALL W/ TILE CAP ON WALL. TEMP. GLASS DOOR.
- RECESSED LIGHT COVE ABV. REFER TO INTERIOR ELEVATIONS.
- PROV. GAS, & ELEC. AT BBQ GRILL AS REQ'D. PER MANUF. SPECS.
- 6X6 STEEL COLUMN W/ TAPERED MASONRY BASE PER ENGINEER'S SPECS. SEE DTL. D/D-2.
- 44" TAPERED STONE BASE W/ STEEL POST PER DETAIL I/D-2.
- CEILING SLOPES W/ ROOF RAFTERS FROM 9'-5 5/8" INT. PLATE TO 10'-0" CLG.
- 4X10" DECO. WOOD BEAMS PER BLDG. SPECS.
- FLUSH HT. 14" DEEP SERVING BAR W/ 4" WALL W/ THIN-CUT 2" STONE VENEER BLW.
- DROPPED STRUC. WOOD-WRAPPED BEAM PER ENGINEER'S SPECS.
- OUTLINE OF DORMER ABV. (REFER TO EXT. ELEVATIONS).
- 36"X18"X21" DEEP REC'D. NICHE. REFER TO INT. ELEV.
- 40" HT. GUARDRAIL PER BLDG. SPECS. & CODE.
- 8" HT. WALL W/ TILE CAP ON TOP. PROVIDE ANCHORING BRACING AS REQ'D. FOR WALL STABILITY.
- BLDR. TO VERIFY HOSE BIB HEIGHT FROM FINISHED GRADE.
- RECESS WINDOW/DOOR 4" FROM EXTERIOR FACE OF WALL PER DEED RESTRICTIONS.
- RECESS WINDOW/DOOR 2" FROM EXTERIOR FACE OF WALL PER DEED RESTRICTIONS.
- 3030 MAS. OPENING W/ 12"X8" WD. HDR. PER BLDG. SPECS.
- PRICE OPTION RFG. VERIFY W/ BLDG.
- PRICE OPTION U.C. RFG. VERIFY W/ BLDG.
- TYPE X GYP&M BOARD IS REQUIRED IN GARAGE.

FLOOR PLAN
SCALE 1/4" = 1'-0"

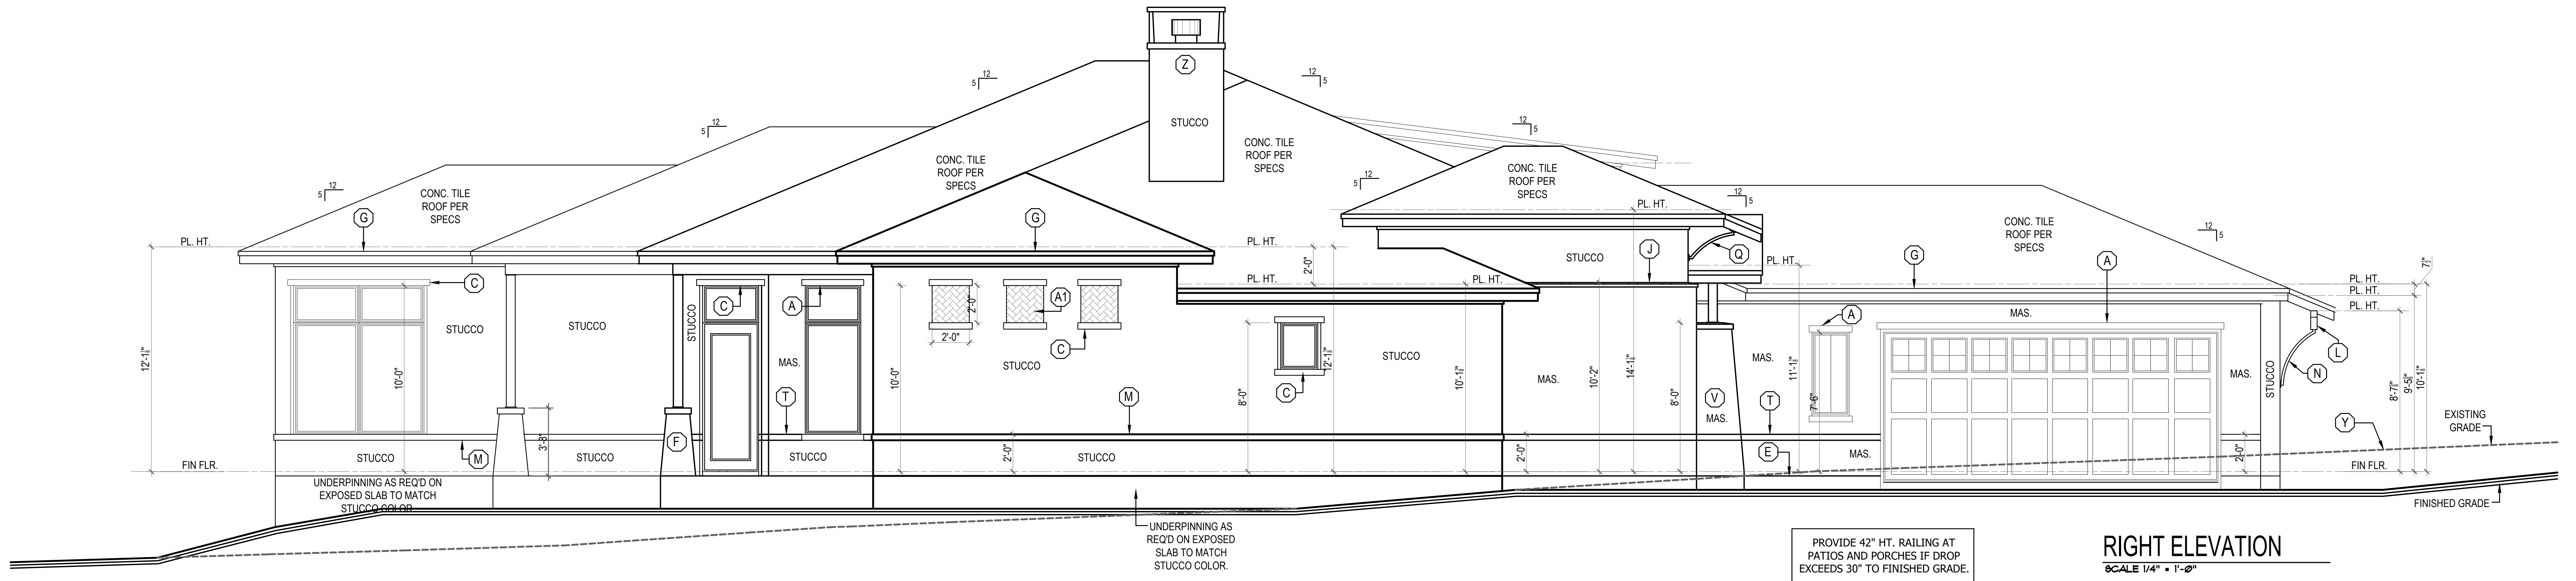

RIGHT ELEVATION
SCALE 1/4" = 1'-0"

NOTE:
HOUSE EXTERIOR IS 100%
MASONRY/STUCCO

- 1) GROUND GRADE LINES SHOWN ON ELEVATIONS MAY VARY FROM ACTUAL FINISHED GRADE. BUILDER TO VERIFY ACTUAL SITE CONDITIONS ON SITE.
- 2) MAX. EXPOSED FOUNDATIONS TO BE 18" OR PER APPLICABLE DEED RESTRICTIONS (WHICHEVER IS LESS).
- 3) CHIMNEY IS SHOWN AT MINIMAL HEIGHT REQUIREMENTS PER CODE. BUILDER TO VERIFY ADDITIONAL HEIGHT REQUIREMENTS BASED ON SITE AND WIND CONDITIONS.
- 4) ALL MASONRY OR STUCCO TRIM/BANDING TO PROJECT 1 1/2" FROM FACE OF FIELD UNO. SLOPE TO DRAIN WATER ADEQUATELY.
- 5) RECESS DOORS AND WINDOWS FROM EXTERIOR FACE OF STUCCO WALLS PER DEED RESTRICTIONS. REFER TO FLOOR PLANS.

EXTERIOR ELEVATION NOTES


- (A) 4" MAS. TRIM/SILL.
- (B) 8" MAS. TRIM/SILL.
- (C) 4" STUCCO TRIM/SILL.
- (D) 6" MAS. TRIM/SILL.
- (E) MASONRY LUG.
- (F) 44" HT. TAPERED MASONRY BASE W/ 6"x6" STEEL POST PER DETAIL 11/D-2.
- (G) FASCIA 4" OVERHANG PER DETAIL AND/OR BLDG. SPECS (TYP).
- (H) N/A
- (J) 3" STUCCO WATERTABLE. REFER TO DETAIL 4/D-1.
- (K) NO TRIM AT WINDOW SLOPE RETURN TO ADEQUATELY DRAIN WATER. FLASH AS REQ'D.
- (L) 4X STRUCTURAL BEAM PER ENGINEER'S SPECS.
- (M) 4" STUCCO BAND TO CONCEAL STUCCO EXPANSION JOINTS. BLOCK OUT AS REQ'D. TO PROJECT 1 1/2" FROM FACE OF STUCCO.
- (N) METAL BRACKET & BEAM PER DETAIL 6/D-1.
- (P) DECO. WOOD CORBELS PER BLDG. SPECS. SEE DETAIL 8/D-1.
- (Q) METAL BRACKET PER DETAIL 8/D-1.
- (R) N/A
- (S) SADDLE AND FLASH AS REQ'D. AT DEAD VALLEY.
- (T) 4" FLUSH STONE BAND. (DO NOT PROJECT FROM FACE OF MASONRY.)
- (U) 8" STUCCO TRIM/SILL.
- (V) METAL COLUMN W/ TAPERED MAS. BASE SUPPORTING STEEL FRAME ROOF PER ENGINEER'S SPECS. SEE DETAIL 12/D-2.
- (W) WOOD UNWRAPPED STRUCTURAL WOOD BEAM PER ENGINEER'S SPECS. REFER TO DETAIL 11/D-2.
- (X) N/A
- (Y) N/A
- (Z) STUCCO CHIMNEY WITH MTL. SPARK ARRESTOR. CHIMNEY TO BE 24" (MIN) ABV. HIGHEST ROOF WITHIN 10'-0". MTL. CHIMNEY CAP PER SPECS & CODE. CRICKET AND FLASHING AS REQ'D (MTL. STUDS ONLY ABV. SPARK ARRESTOR).
- (AI) 2" DEEP RECESS IN STUCCO WALL W/ TILE INSERT. TILE PER BLDG. SPECS.

OWNER:
LINDSAY & BLAKE TAYLOR
XXXX XXXXX VIEW LN.
XXXX, TEXAS 71024
T.(XXX) XXX-XXXX


BUILDER:
XXXX XXXXX
XXXXX CUSTOM HOMES
2303 REB20 SOUTH, SUITE 135-212
AUSTIN, TEXAS 78134
T.(XXX) XXX-XXXX

ARCHITECT:
KAI GESCHKE
GESCHKE GROUP ARCHITECTURE
11200 RANCH RD. 2222
AUSTIN, TEXAS 78730
T.(512) 502 8484

ENGINEER:
XXXX XXXXXX
XXXXX ENGINEERING, LLC
1120 COTTONWOOD CREEK TRAIL
CEDAR PARK, TEXAS 78613
T.(XXX) XXX-XXXX

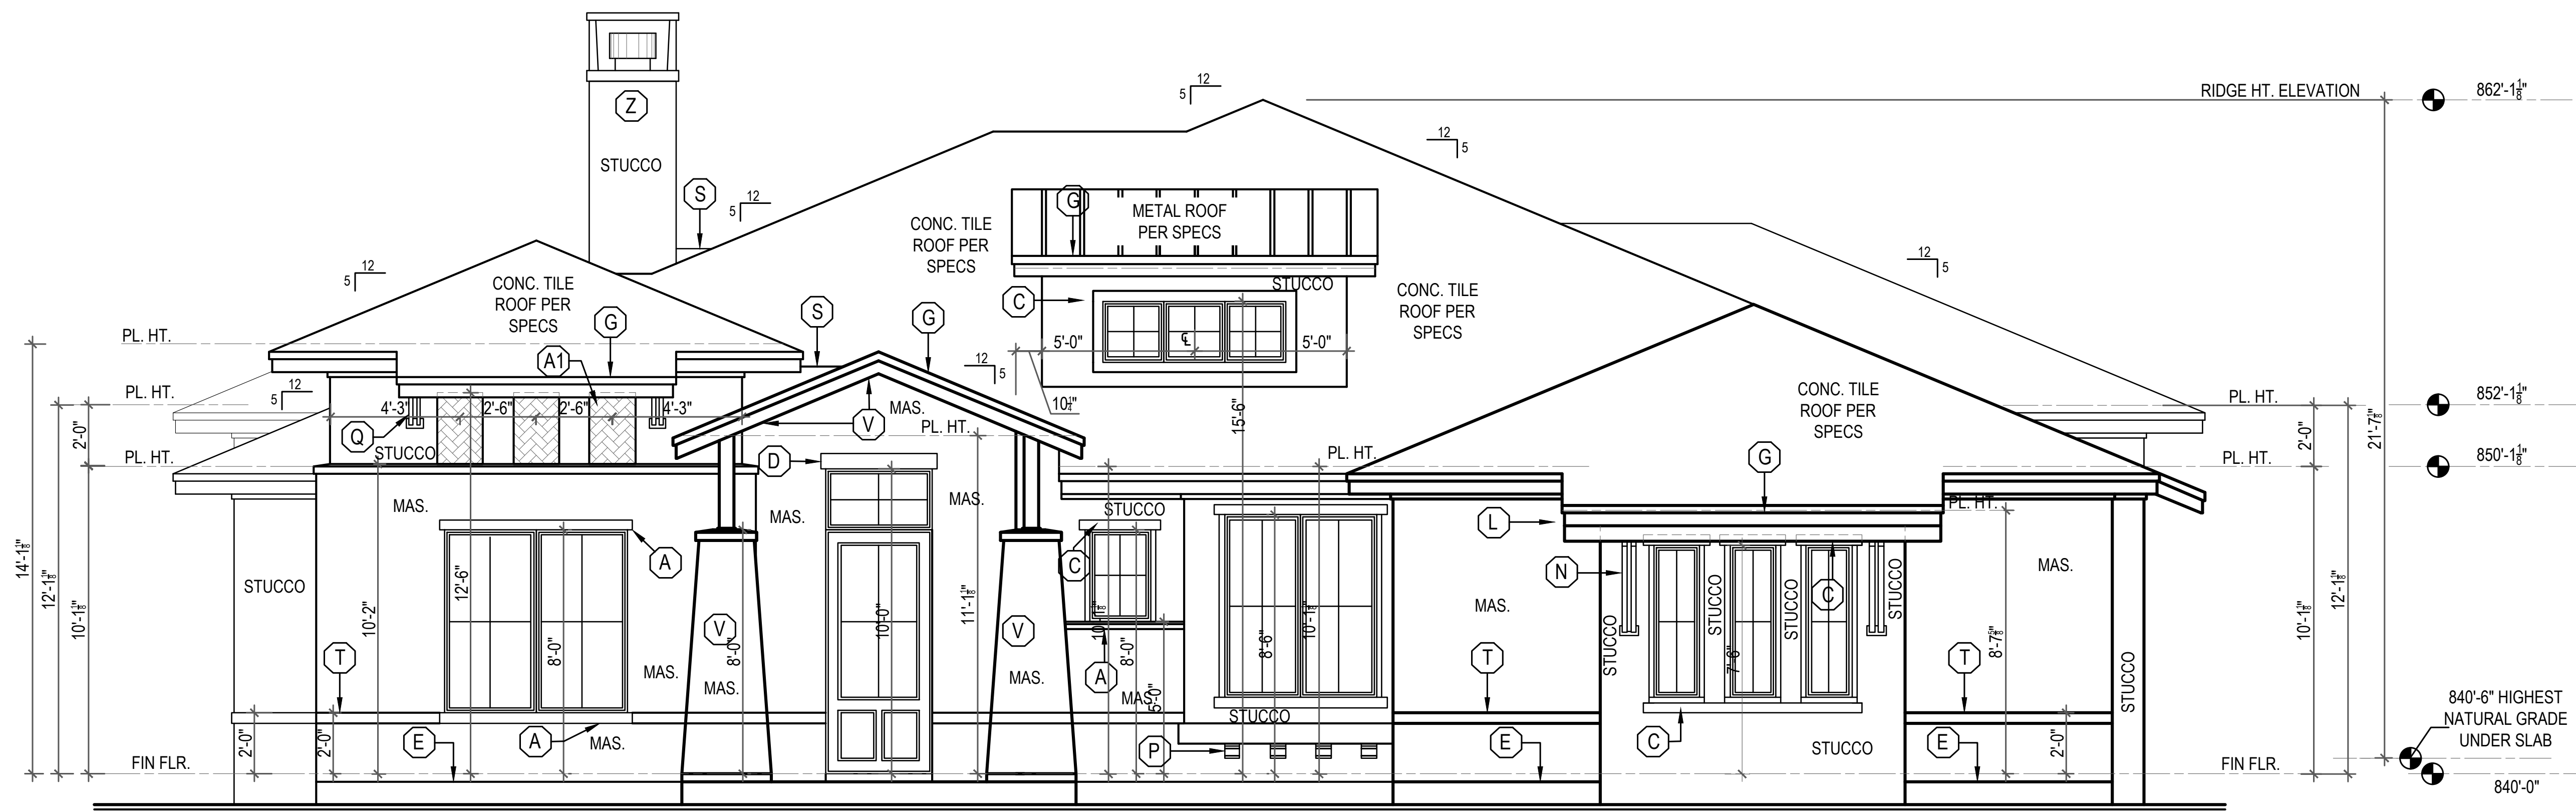

FRONT ELEVATION
SCALE 1/4" = 1'-0"

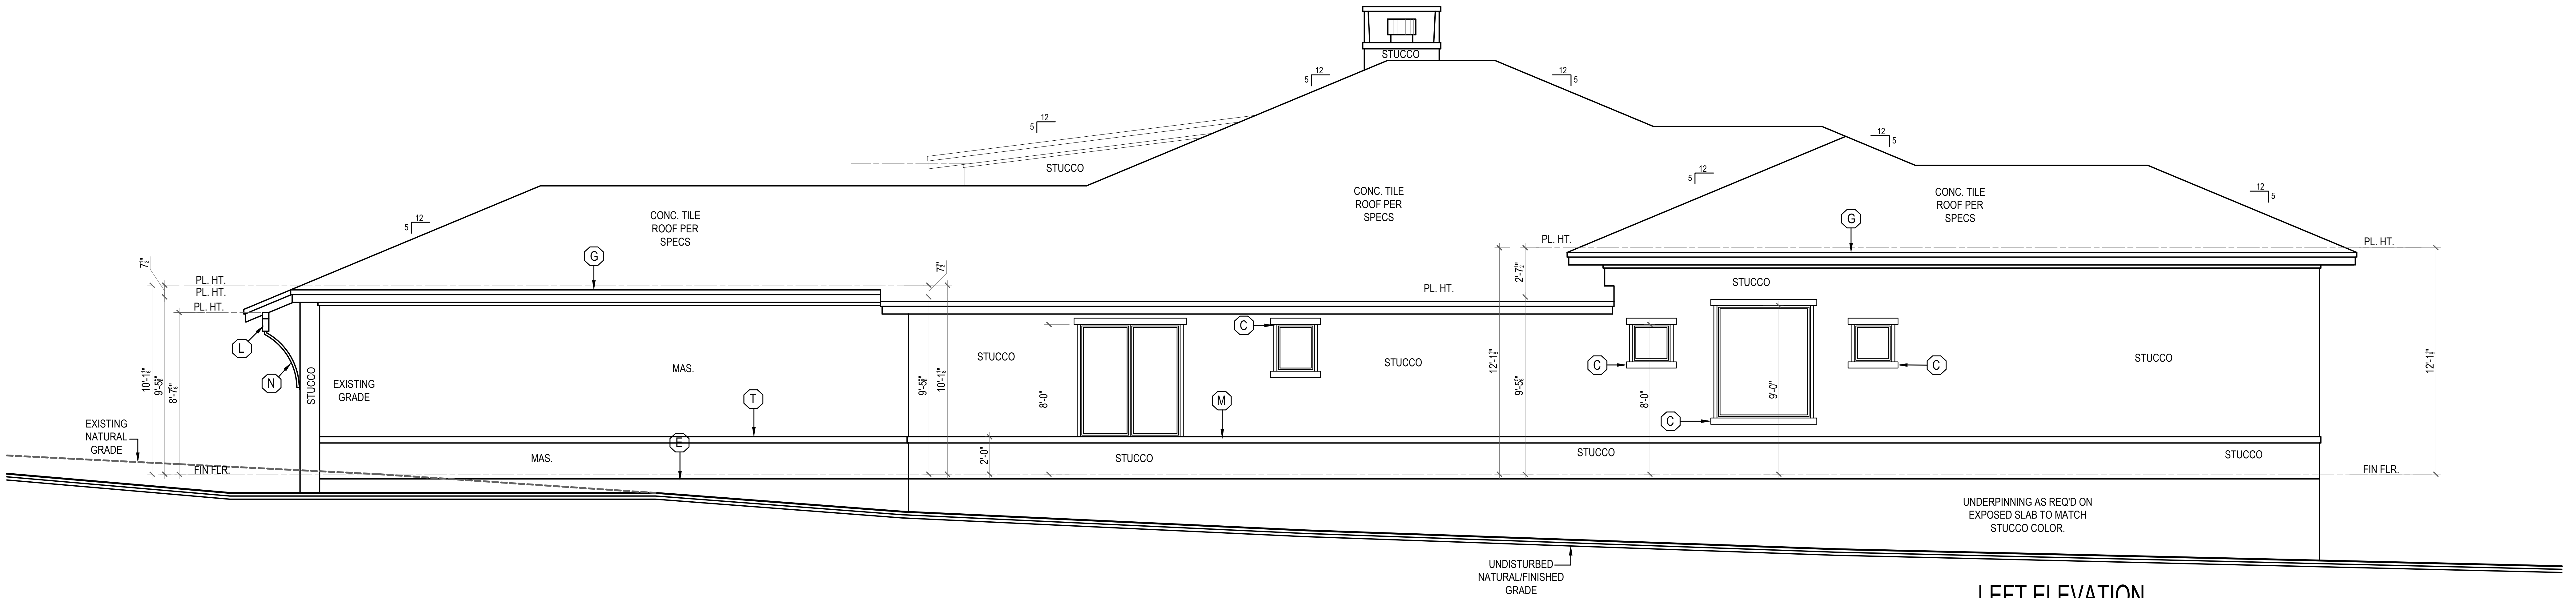

LEFT ELEVATION

SCALE 1/4" = 1'-0"

NOTE:
HOUSE EXTERIOR IS 100%
MASONRY/STUCCO

- 1) GROUND GRADE LINES SHOWN ON ELEVATIONS MAY VARY FROM ACTUAL FINISHED GRADE. BUILDER TO VERIFY ACTUAL SITE CONDITIONS ON SITE.
- 2) MAX. EXPOSED FOUNDATIONS TO BE 18" OR PER APPLICABLE DEED RESTRICTIONS (WHICHEVER IS LESS)
- 3) CHIMNEY IS SHOWN AT MINIMAL HEIGHT REQUIREMENTS PER CODE. BUILDER TO VERIFY ADDITIONAL HEIGHT REQUIREMENTS BASED ON SITE AND WIND CONDITIONS.
- 4) ALL MASONRY OR STUCCO TRIM/BANDING TO PROJECT 1 1/2" FROM FACE OF FIELD UNO. SLOPE TO DRAIN WATER ADEQUATELY.
- 5) RECESSED DOORS AND WINDOWS FROM EXTERIOR FACE OF STUCCO WALLS PER DEED RESTRICTIONS. REFER TO FLOOR PLANS.

EXTERIOR ELEVATION NOTES


- (A) 4" MAS. TRIM/SILL.
- (B) 8" MAS. TRIM/SILL.
- (C) 4" STUCCO TRIM/SILL.
- (D) 6" MAS. TRIM/SILL.
- (E) MASONRY LUG.
- (F) 44" HT. TAPERED MASONRY BASE W/ 6"x6" STEEL POST PER DETAIL 1/D-2.
- (G) FASCIA & OVERHANG PER DETAIL AND/OR BLDR. SPECS (TYP)
- (H) N/A
- (J) 3" STUCCO WATERTABLE. REFER TO DETAIL 4/D-1
- (K) NO TRIM AT WINDOW. SLOPE RETURN TO ADEQUATELY DRAIN WATER. FLASH AS REQ'D.
- (L) 4X STRUCTURAL BEAM PER ENGINEER'S SPECS.
- (M) 4" STUCCO BAND TO CONCEAL STUCCO EXPANSION JOINTS. BLOCK OUT AS REQ'D. TO PROJECT 1 1/2" FROM FACE OF STUCCO
- (N) METAL BRACKET & BEAM PER DETAIL 6/D-1.
- (P) DECO. WOOD CORBELS PER BLDR. SPECS. SEE DETAIL 5/D-1.
- (Q) METAL BRACKET PER DETAIL 8/D-1.
- (R) N/A
- (S) SADDLE AND FLASH AS REQ'D. AT DEAD VALLEY.
- (T) 4" FLUSH STONE BAND. (DO NOT PROJECT FROM FACE OF MASONRY.)
- (U) 8" STUCCO TRIM/SILL.
- (V) METAL COLUMNS W/ TAPERED MAS. BASE SUPPORTING STEEL FRAME ROOF PER ENGINEER'S SPECS. SEE DETAIL 12/D-2.
- (W) WOOD WRAPPED STRUCTURAL WOOD BEAM PER ENGINEER'S SPECS. REFER TO DETAIL 11/D-2.
- (X) N/A
- (Y) N/A
- (Z) STUCCO CHIMNEY WITH MTL. SPARK ARRESTOR. CHIMNEY TO BE 24" (MIN) ABV. HIGHEST ROOF WITHIN 10'-0". MTL. CHIMNEY CAP PER SPECS & CODE. CRICKET AND FLASHING AS REQ'D (MTL. STUDS ONLY ABV. SPARK ARRESTOR).
- (AI) 2" DEEP RECESS IN STUCCO WALL W/ TILE INSERT. TILE PER BLDR. SPECS.

OWNER:
LINDSAY & BLAKE TAYLOR
XXXX XXXXX VIEW LN.
XXXX, TEXAS 71024
T.(XXX) XXX-XXXX

BUILDER:
XXXX XXXXX
XXXXX CUSTOM HOMES
2303 RRE20 SOUTH, SUITE 135-212
AUSTIN, TEXAS 78134
T.(XXX) XXX-XXXX

ARCHITECT:
KAI GESCHKE
GESCHKE GROUP ARCHITECTURE
11200 RANCH RD. 2222
AUSTIN, TEXAS 78130
T.(512) 502 8484



ENGINEER:
XXXX XXXXXXX
XXXXX ENGINEERING, LLC
1120 COTTONWOOD CREEK TRAIL
CEDAR PARK, TEXAS 78613
T.(XXX) XXX-XXXX

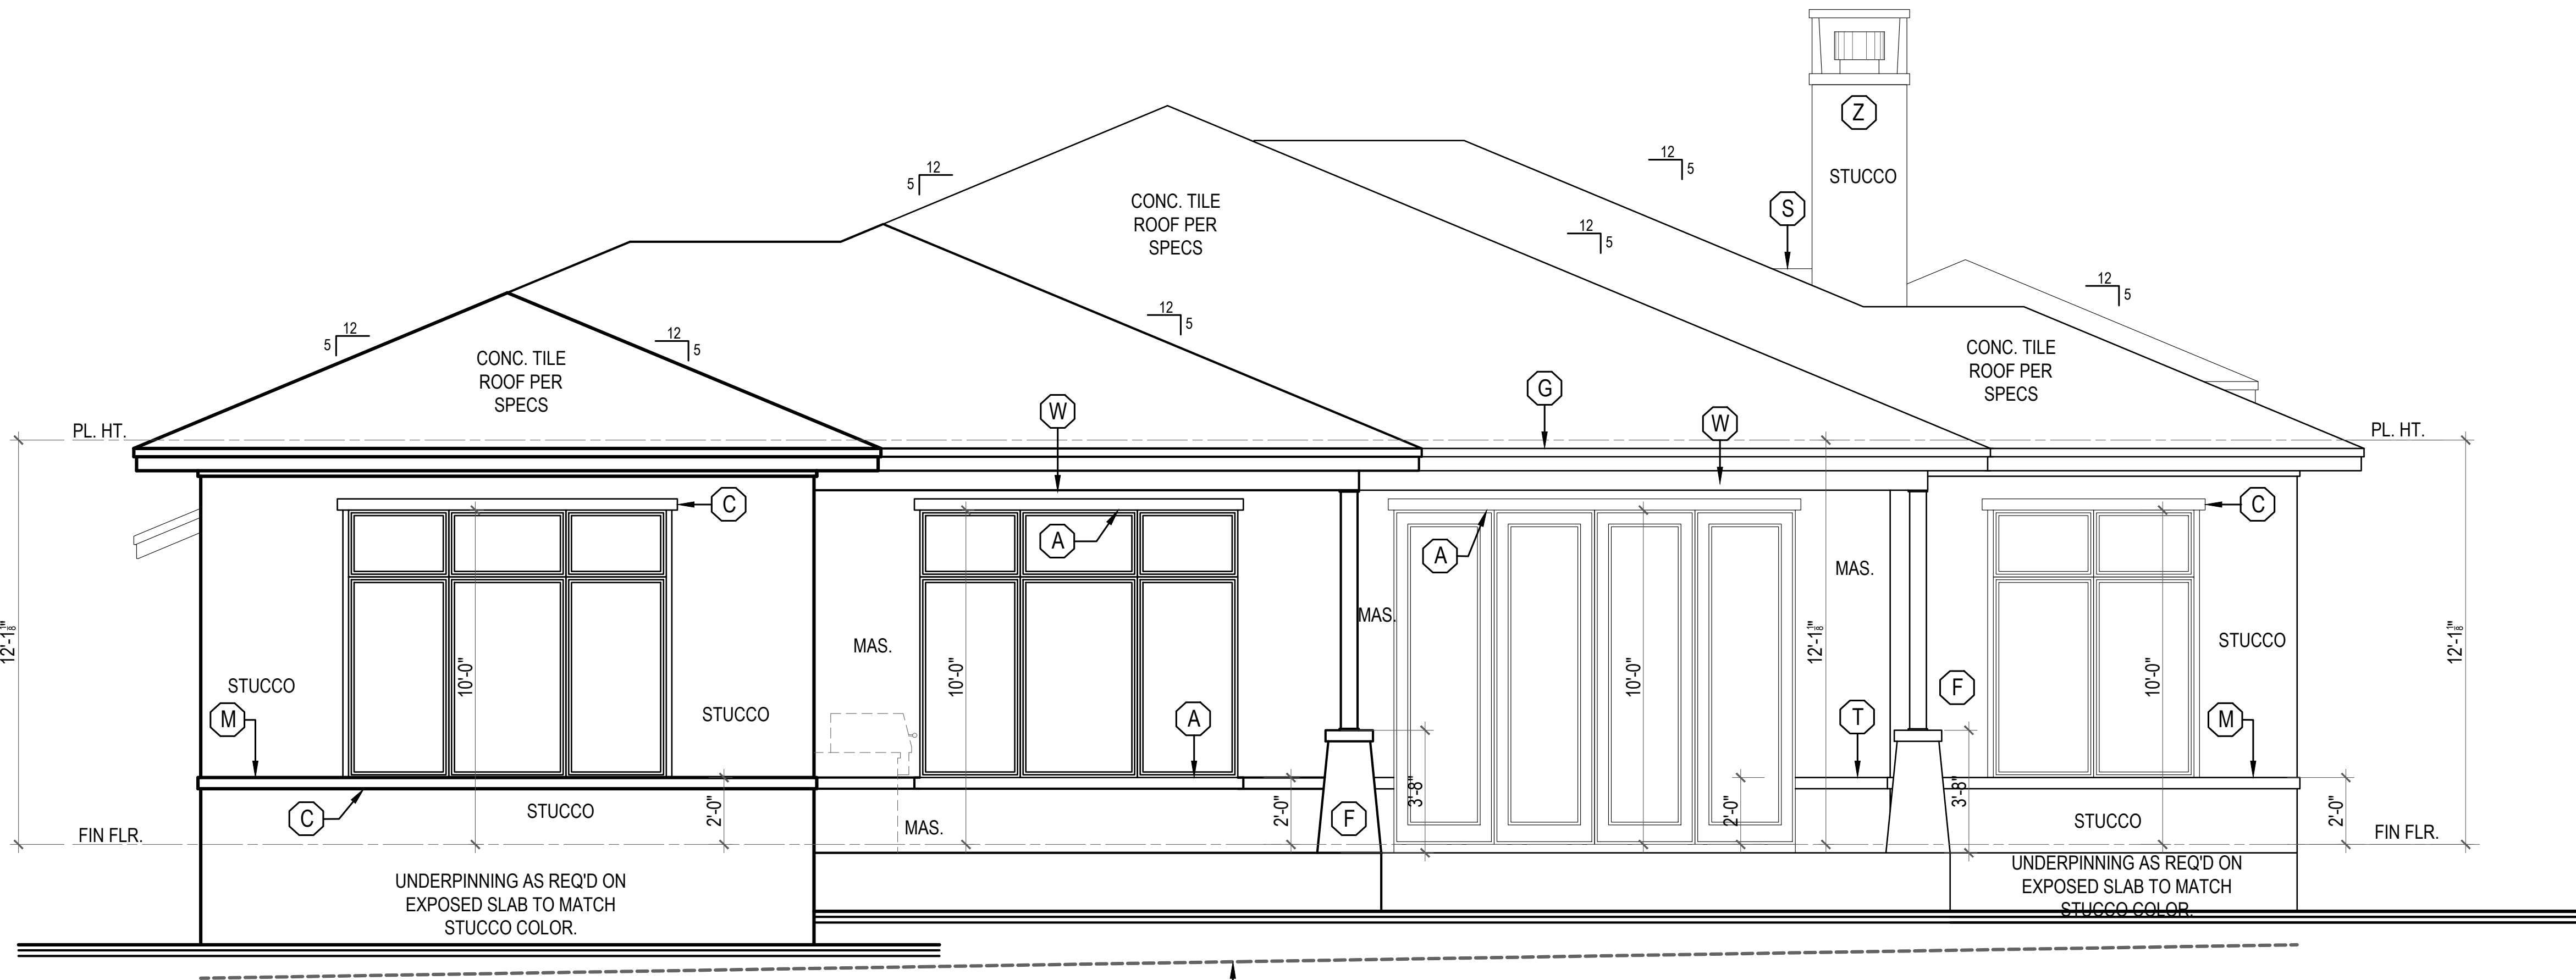

REAR ELEVATION

SCALE 1/4" = 1'-0"

PROVIDE 42" HT. RAILING AT PATIOS
AND PORCHES IF DROP EXCEEDS 30"
TO FINISHED GRADE.

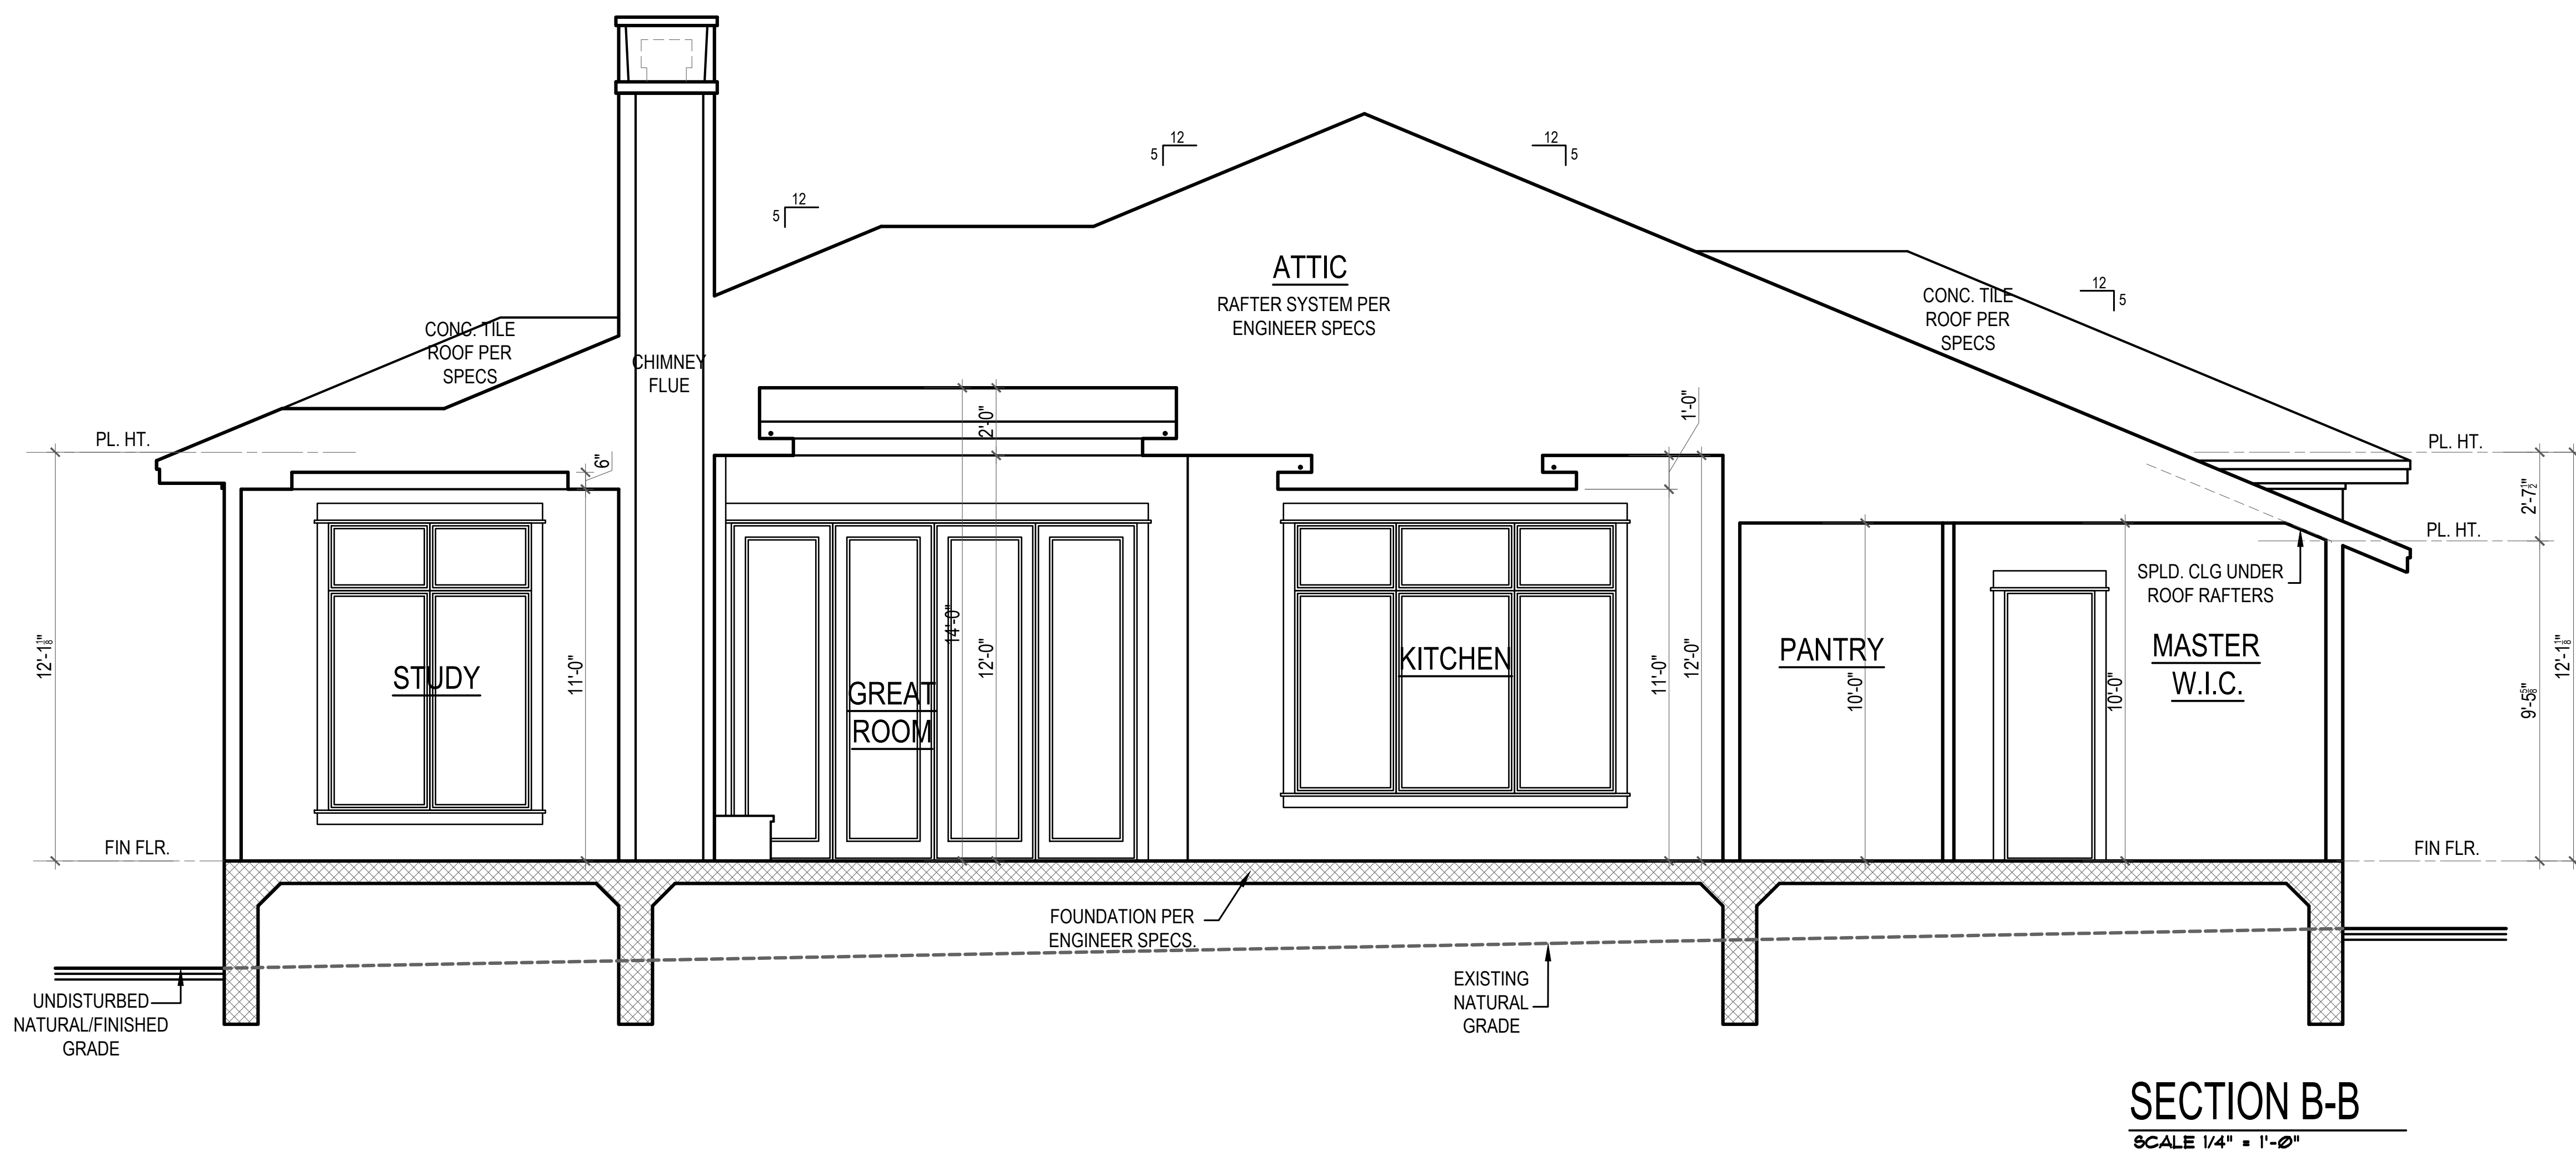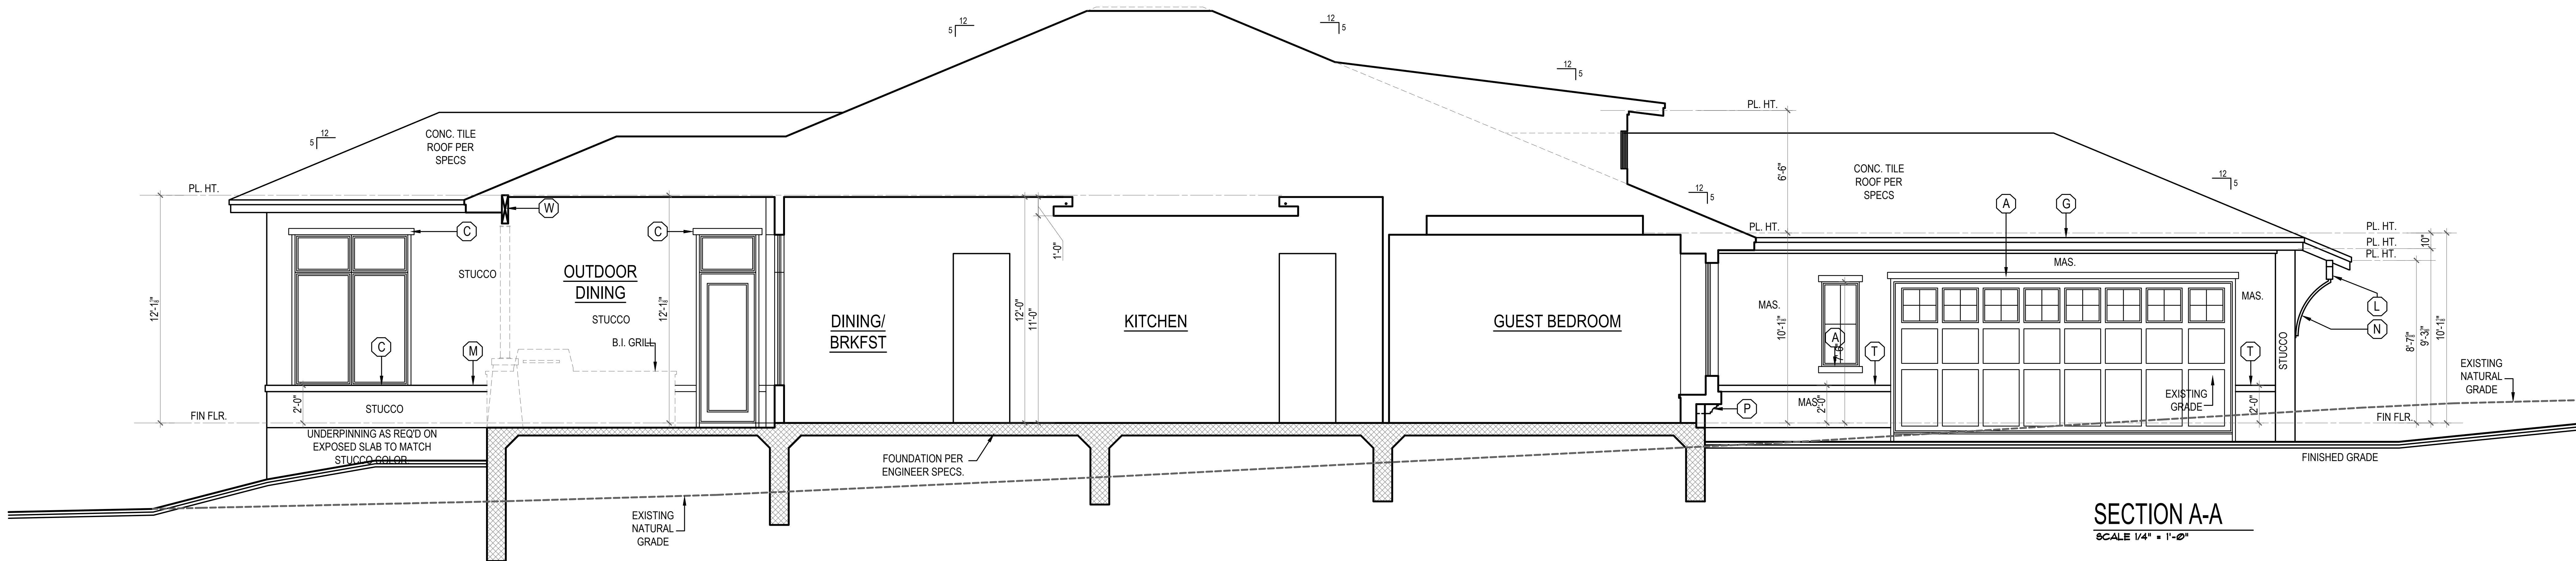

NOTE:
HOUSE EXTERIOR IS 100%
MASONRY/STUCCO

- 1) GROUND GRADE LINES SHOWN ON ELEVATIONS MAY VARY FROM ACTUAL FINISHED GRADE. BUILDER TO VERIFY ACTUAL SITE CONDITIONS ON SITE.
- 2) MAX. EXPOSED FOUNDATIONS TO BE 18" OR PER APPLICABLE DEED RESTRICTIONS (WHICHEVER IS LESS)
- 3) CHIMNEY IS SHOWN AT MINIMAL HEIGHT REQUIREMENTS PER CODE. BUILDER TO VERIFY ADDITIONAL HEIGHT REQUIREMENTS BASED ON SITE AND WIND CONDITIONS.
- 4) ALL MASONRY OR STUCCO TRIM/BANDING TO PROJECT 1 1/2" FROM FACE OF FIELD UNO. SLOPE TO DRAIN WATER ADEQUATELY.
- 5) RECESS DOORS AND WINDOWS FROM EXTERIOR FACE OF STUCCO WALLS PER DEED RESTRICTIONS, REFER TO FLOOR PLANS.

EXTERIOR ELEVATION NOTES

- (A) 4" MAS. TRIM/BILL.
- (B) 8" MAS. TRIM/BILL.
- (C) 4" STUCCO TRIM/BILL.
- (D) 6" MAS. TRIM/BILL.
- (E) MASONRY LUG.
- (F) 44" HT. TAPERED MASONRY BASE W/ 6"x6" STEEL POST PER DETAIL 11/D-2.
- (G) PARCIA 4 OVERHANGS PER DETAIL AND/OR BLDG. SPECS (TYP)
- (H) N/A
- (J) 3" STUCCO WATERTABLE. REFER TO DETAIL 4/D-1.
- (K) NO TRIM AT WINDOW. SLOPE RETURN TO ADEQUATELY DRAIN WATER. FLASH AS REQ'D.
- (L) 4X STRUCTURAL BEAM PER ENGINEER'S SPECS.
- (M) 4" STUCCO BAND TO CONCEAL STUCCO EXPANSION JOINTS. BLOCK OUT AS REQ'D. TO PROJECT 1 1/2" FROM FACE OF STUCCO
- (N) METAL BRACKET 4 BEAM PER DETAIL 6/D-1.
- (P) DECO. WOOD CORBELS PER BLDG. SPECS. SEE DETAIL 5/D-1.
- (Q) METAL BRACKET PER DETAIL 8/D-1.
- (R) N/A
- (S) SADDLE AND FLASH AS REQ'D. AT DEAD VALLEY.
- (T) 4" FLUSH STONE BAND. (DO NOT PROJECT FROM FACE OF MASONRY)
- (U) 8" STUCCO TRIM/BILL.
- (V) METAL COLUMN W/ TAPERED MAS. BASE SUPPORTING STEEL FRAME ROOF PER ENGINEER'S SPECS. SEE DETAIL 11/D-2.
- (W) WOOD UNRAFFED STRUCTURAL WOOD BEAM PER ENGINEER'S SPECS. REFER TO DETAIL 11/D-2.
- (X) N/A
- (Y) N/A
- (Z) STUCCO CHIMNEY WITH MTL. SPARK ARRESTOR. CHIMNEY TO BE 24" (MIN) ABV. HIGHEST ROOF WITHIN 120'-0". MTL. CHIMNEY CAP PER SPECS 4 CODE. CRICKET AND FLASHING AS REQ'D (MTL. STUDS ONLY ABV. SPARK ARRESTOR).
- (A) 2" DEEP RECESS IN STUCCO WALL W/ TILE INSERT. TILE PER BLDG. SPECS.



















OWNER:
LINDSAY & BLAKE TAYLOR
XXX XXXXX VIEW LN.
XXXX, TEXAS 71024
T.(XXX) XXX-XXXX

BUILDER:
XXX XXXXX
XXXXX CUSTOM HOMES
2303 RR620 SOUTH, SUITE 135-212
AUSTIN, TEXAS 78734
T.(XXX) XXX XXXX

ARCHITECT:
KAI GESCHKE
GESCHKE GROUP ARCHITECTURE
11200 RANCH RD, 2222
AUSTIN, TEXAS 78730
T.(512) 502 8484


ENGINEER:
XXXX XXXXXX
XXXXX ENGINEERING, LLC
1120 COTTONWOOD CREEK TRAIL
CEDAR PARK, TEXAS 78613
T.(XXX) XXX-XXXX

SCHEMATIC ROOF PLAN

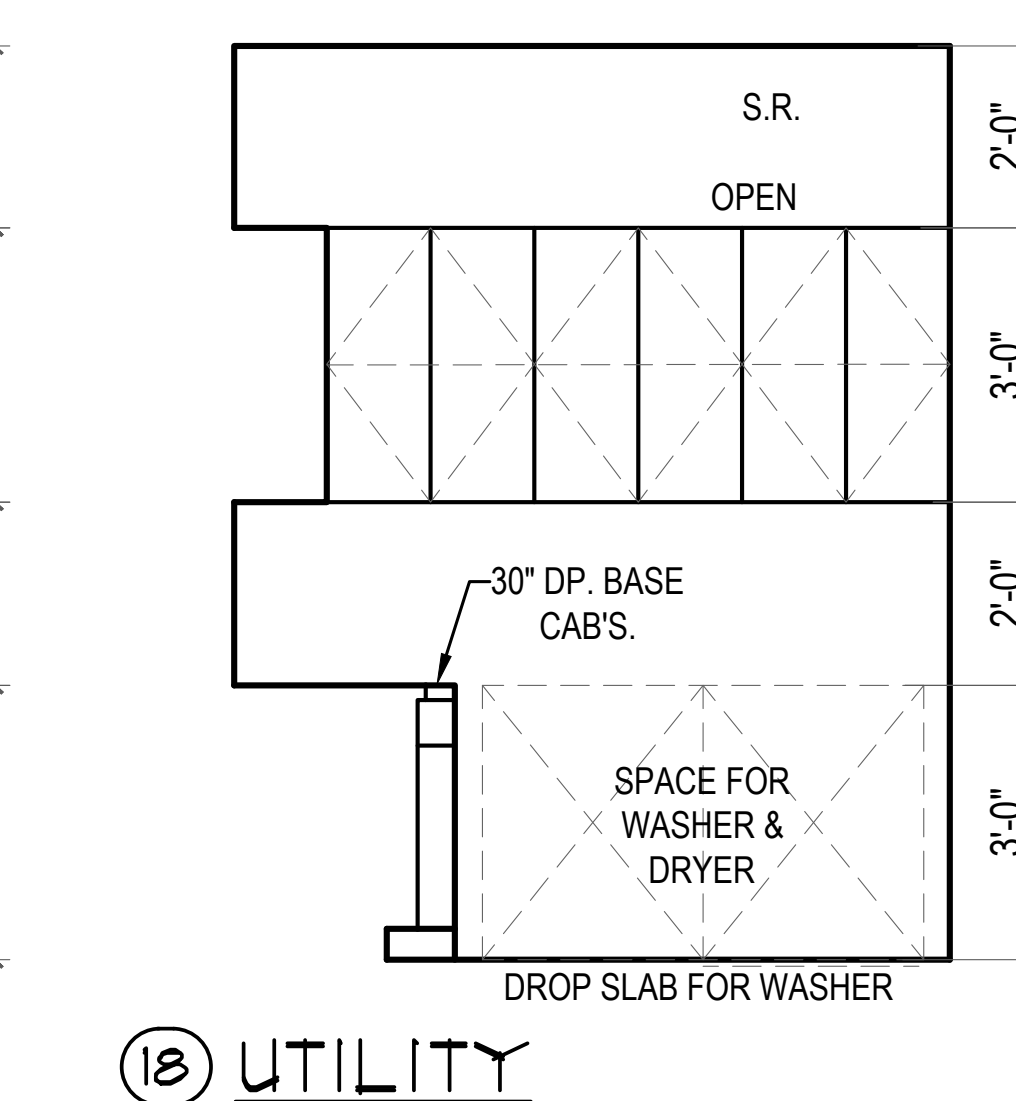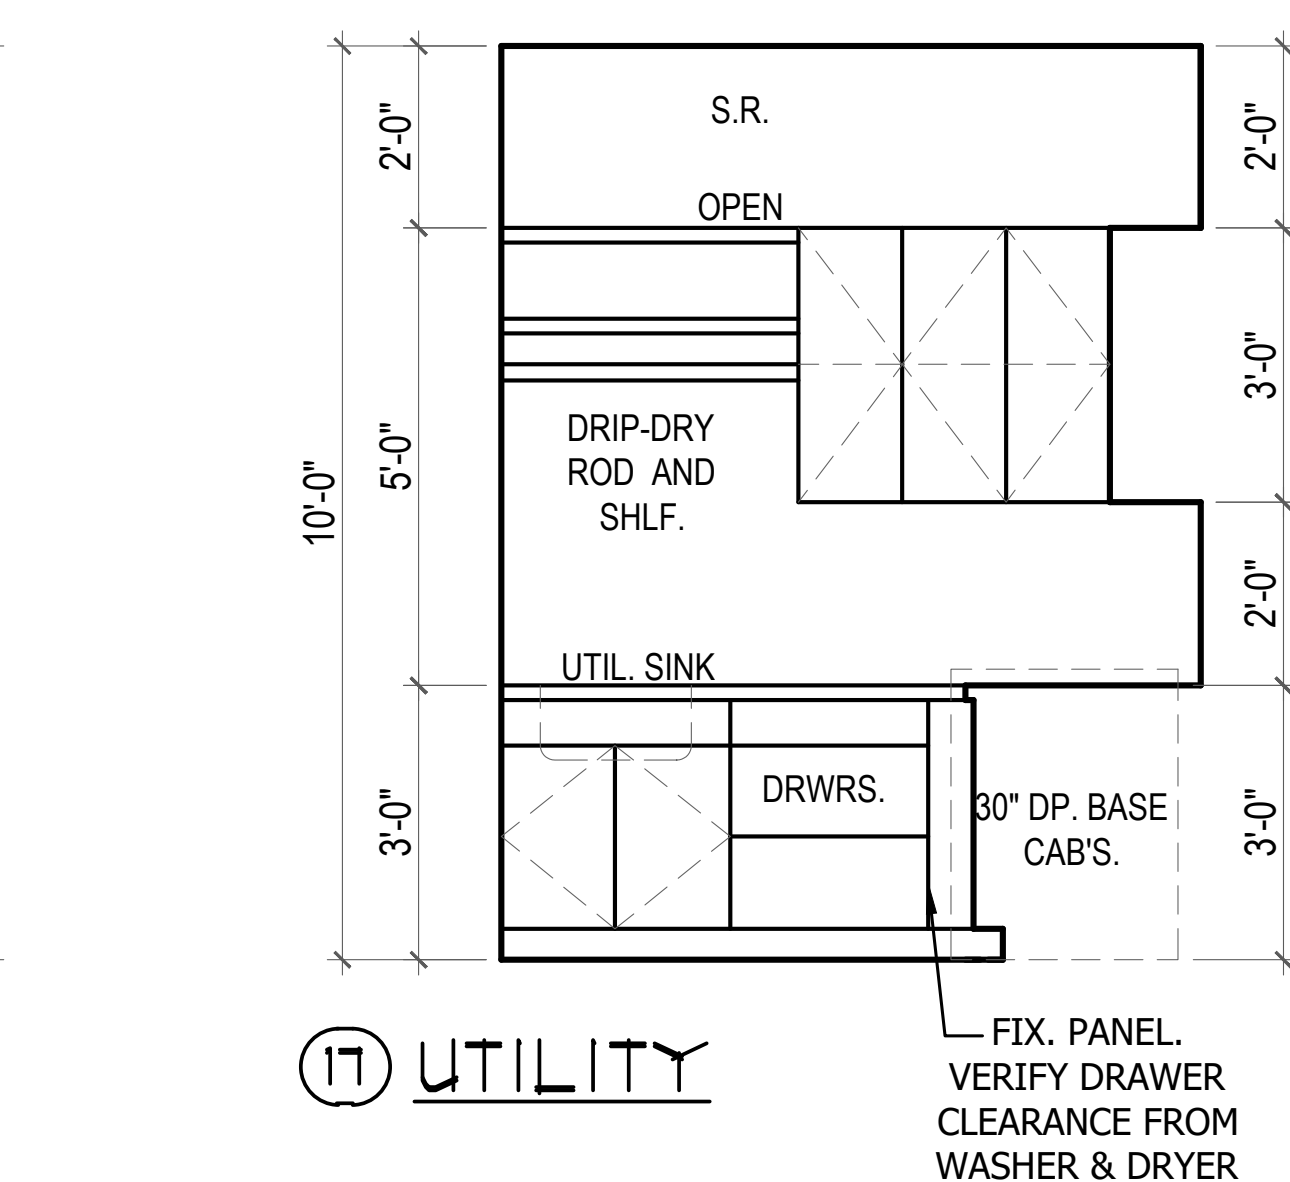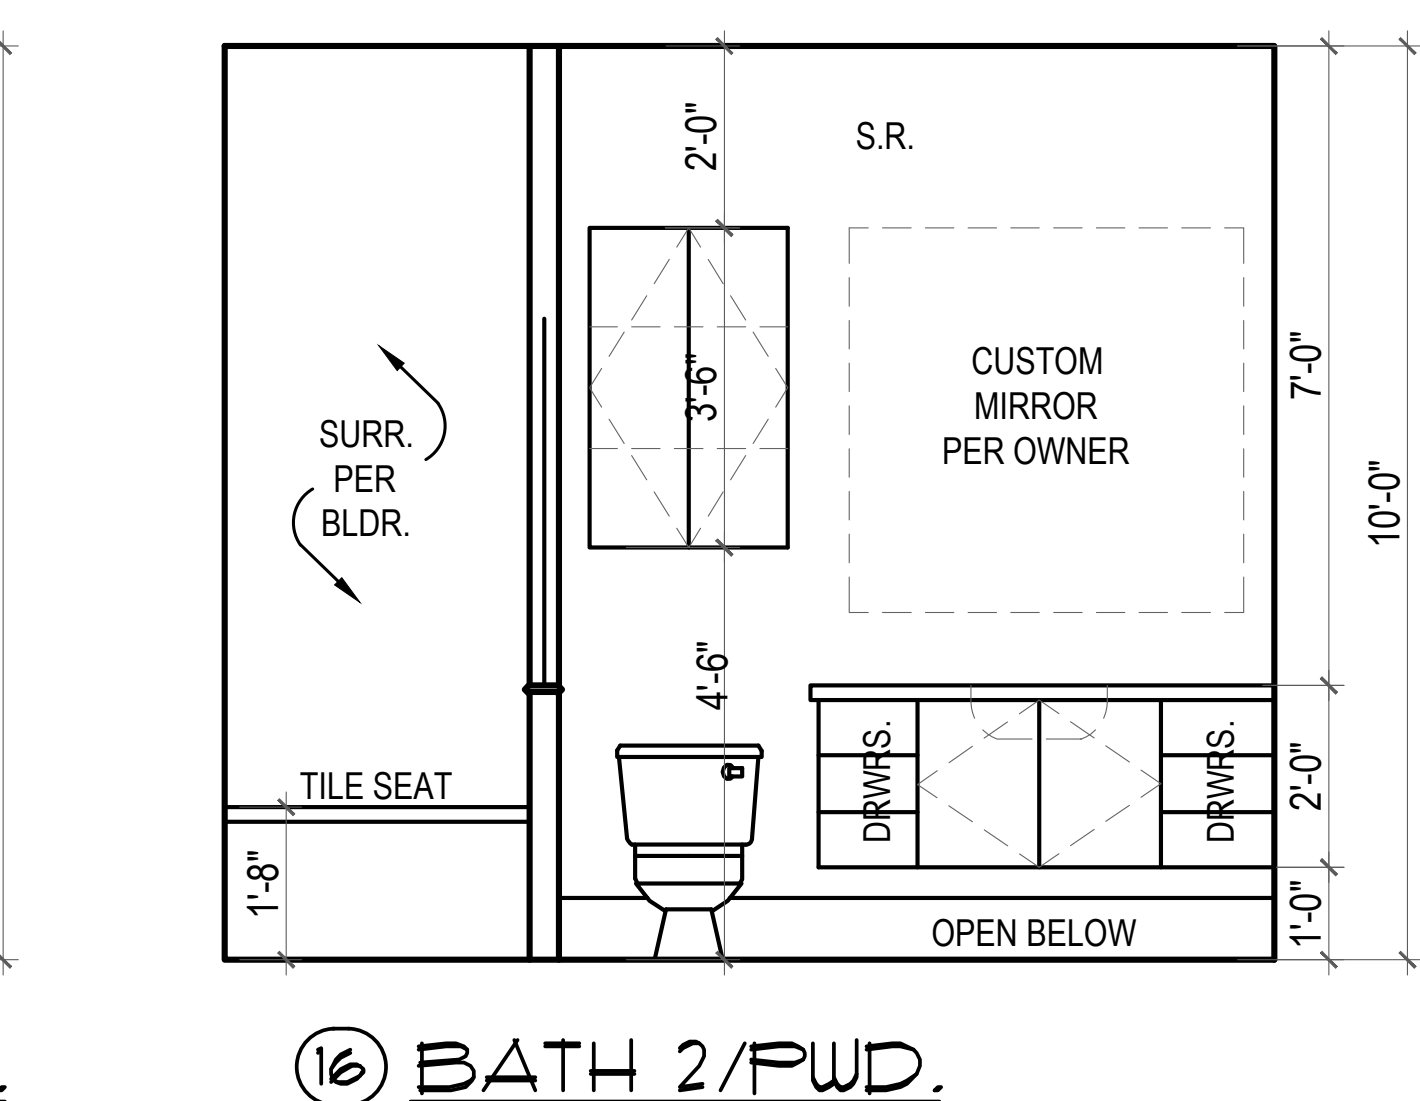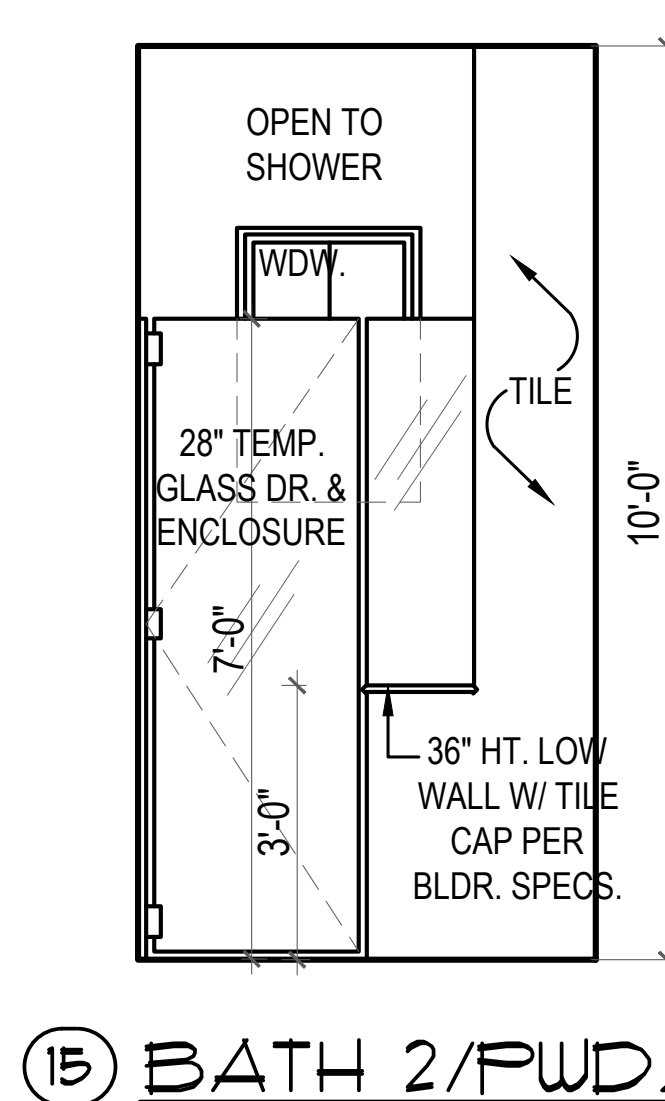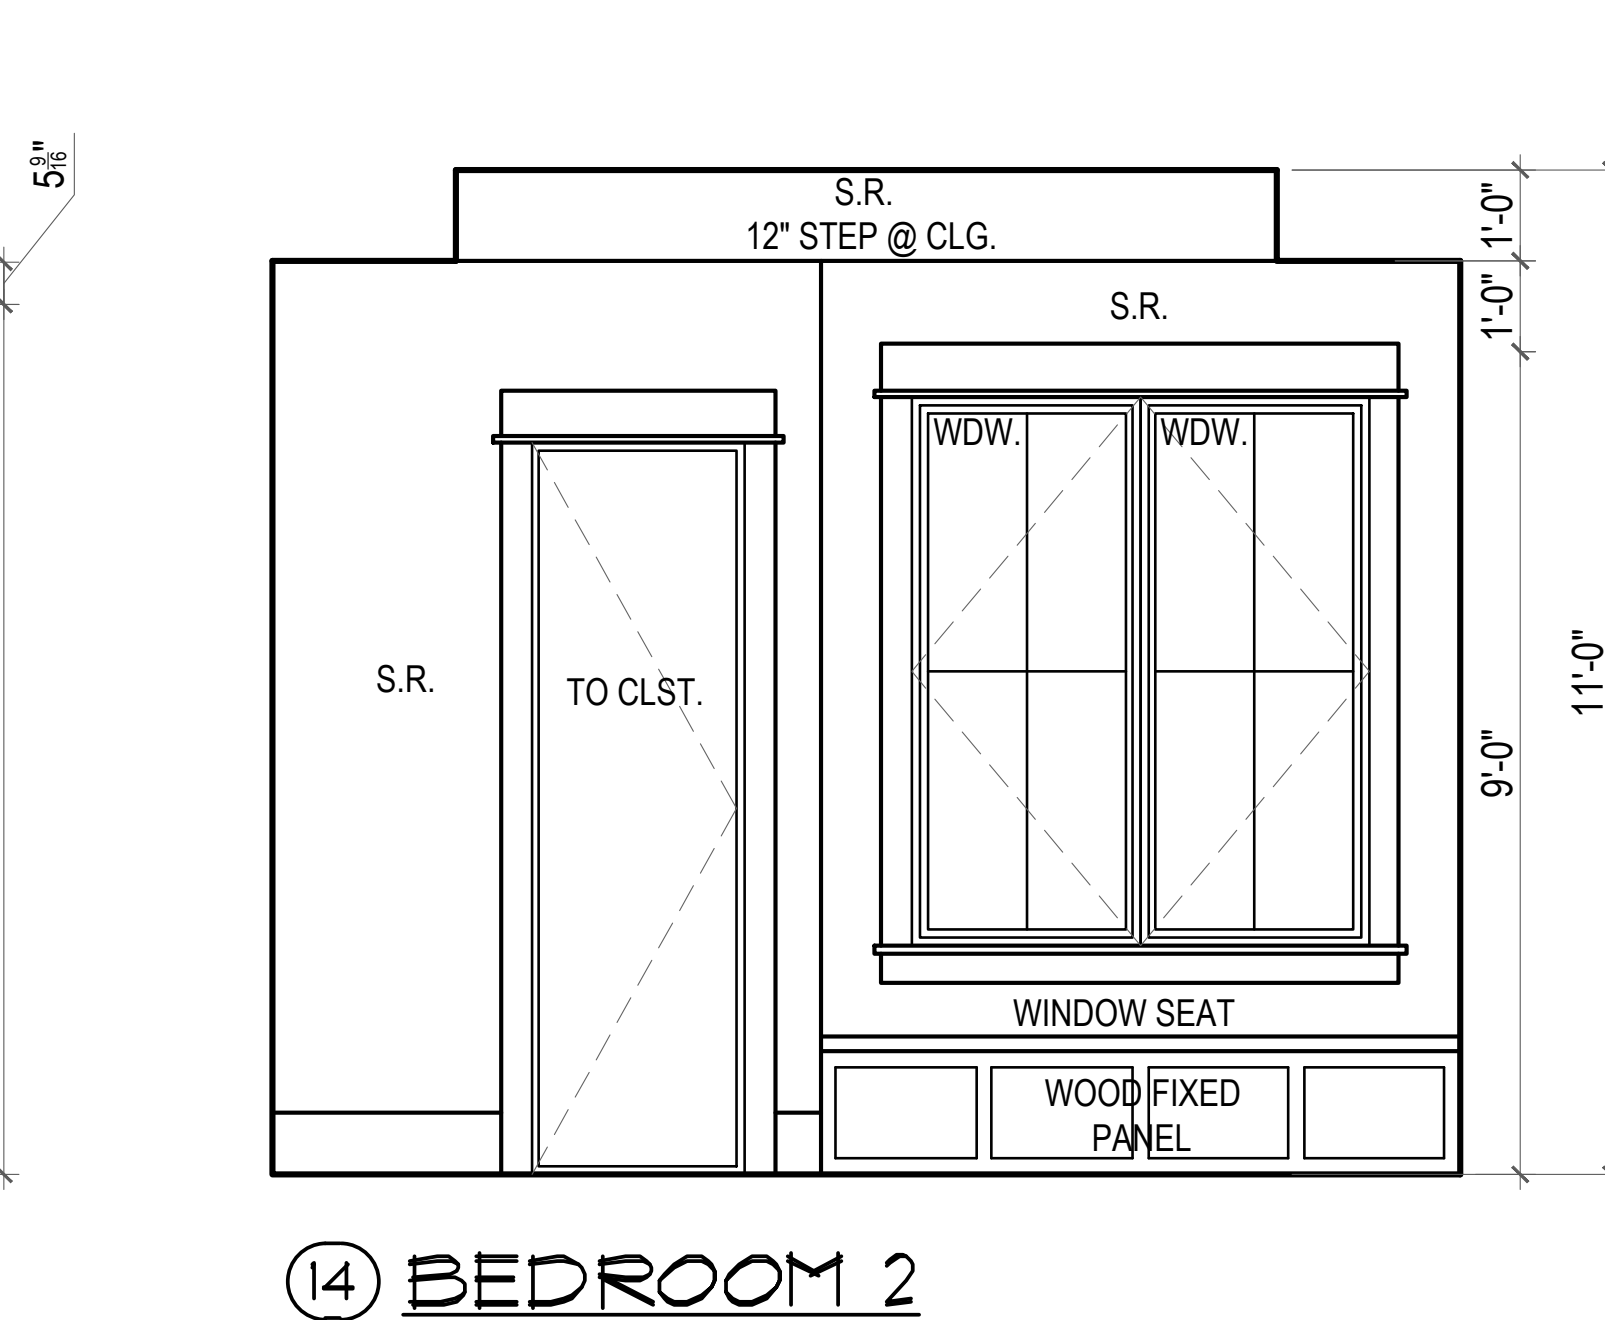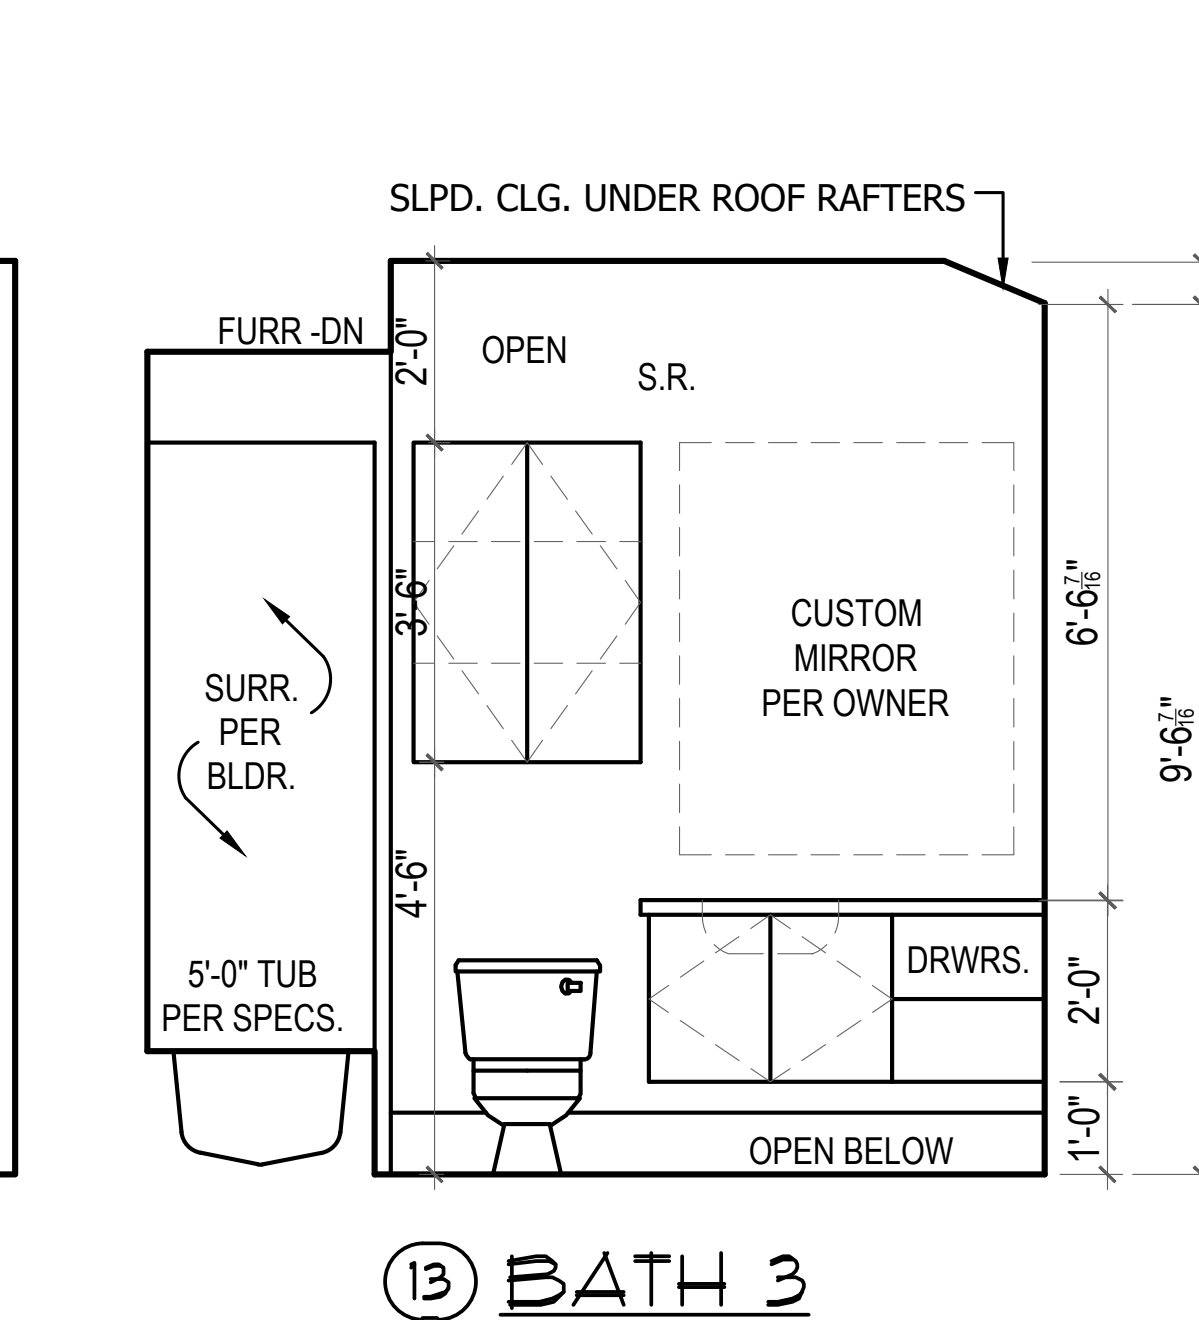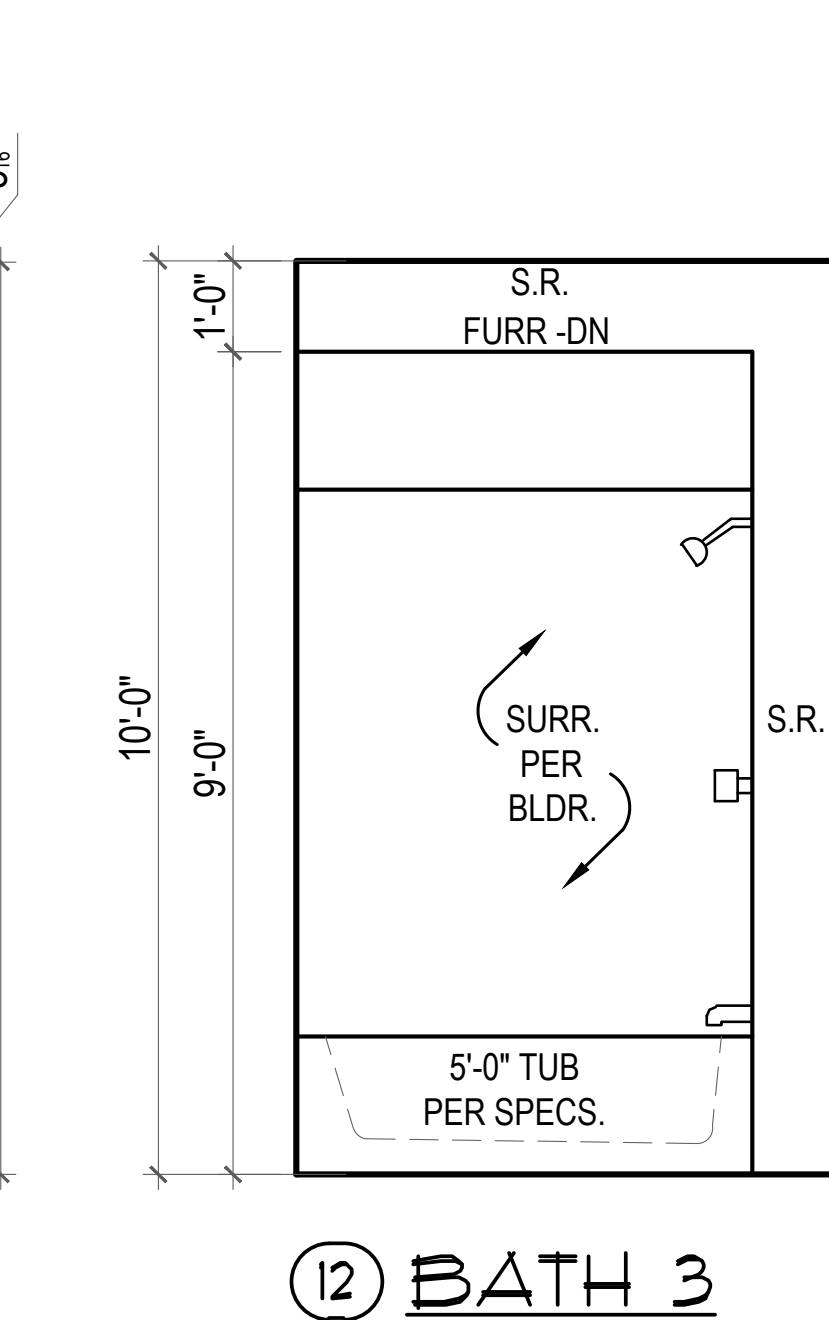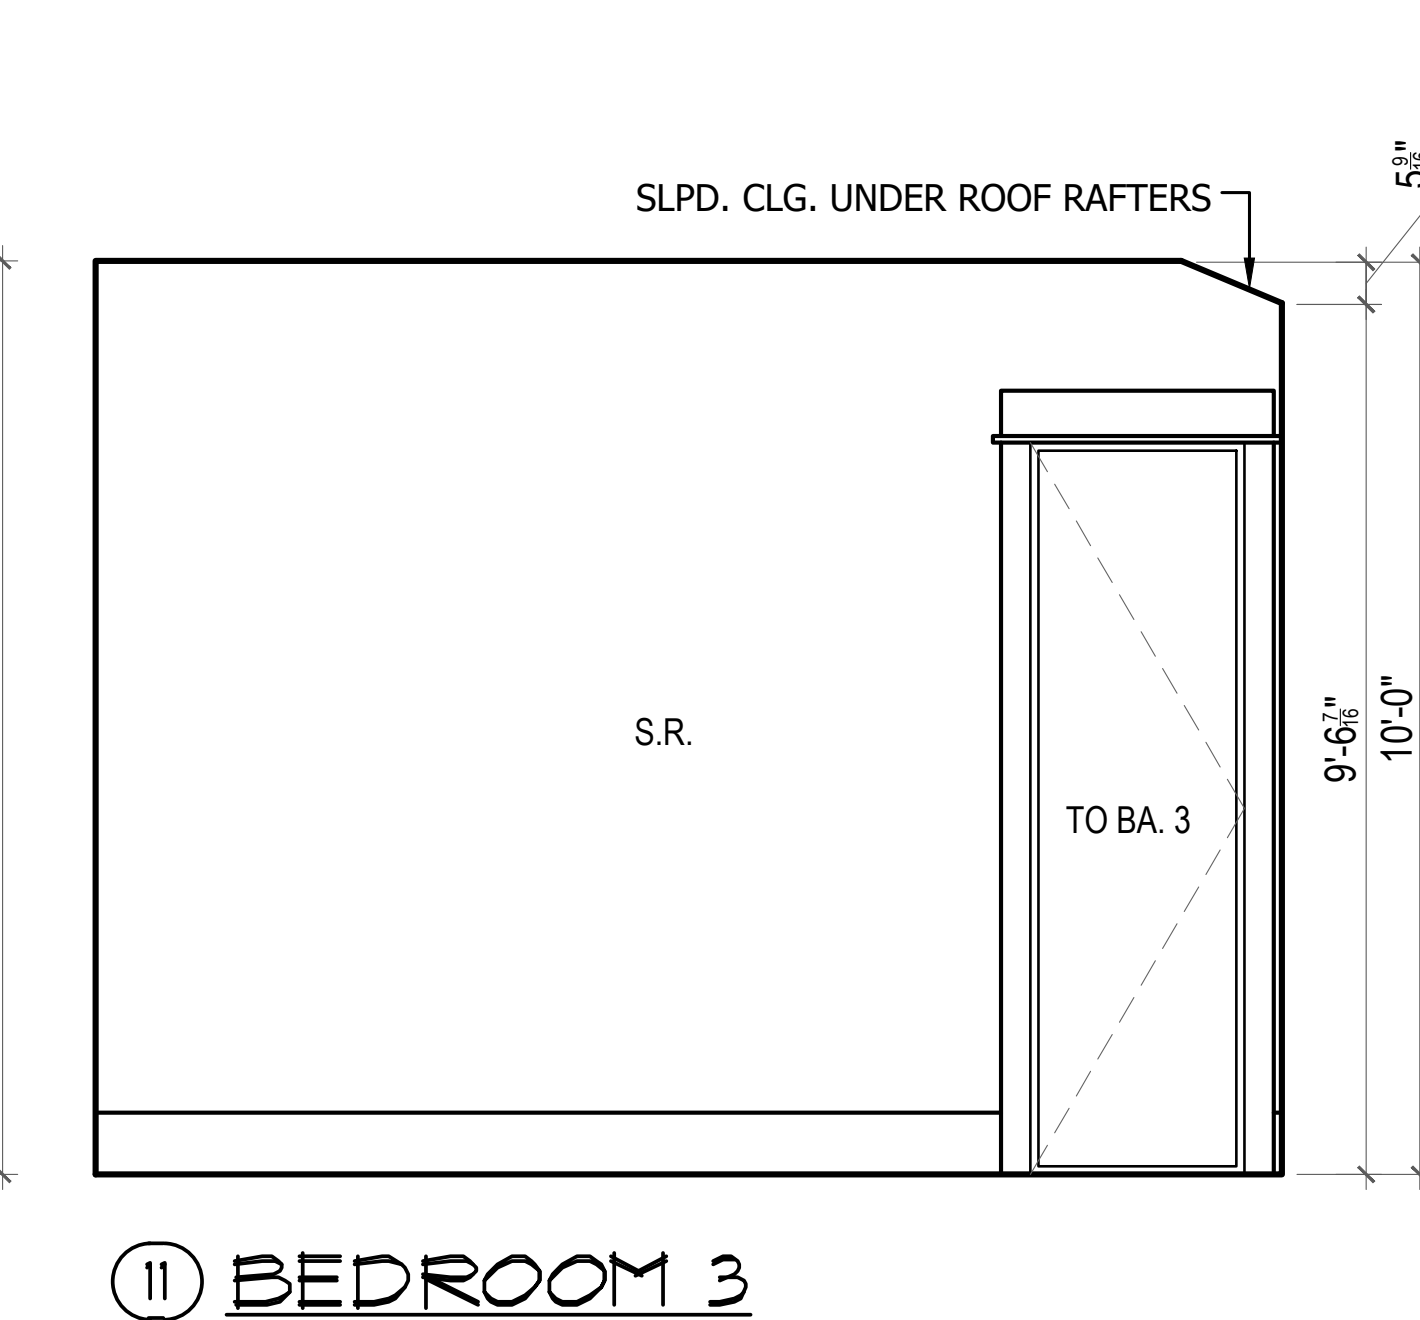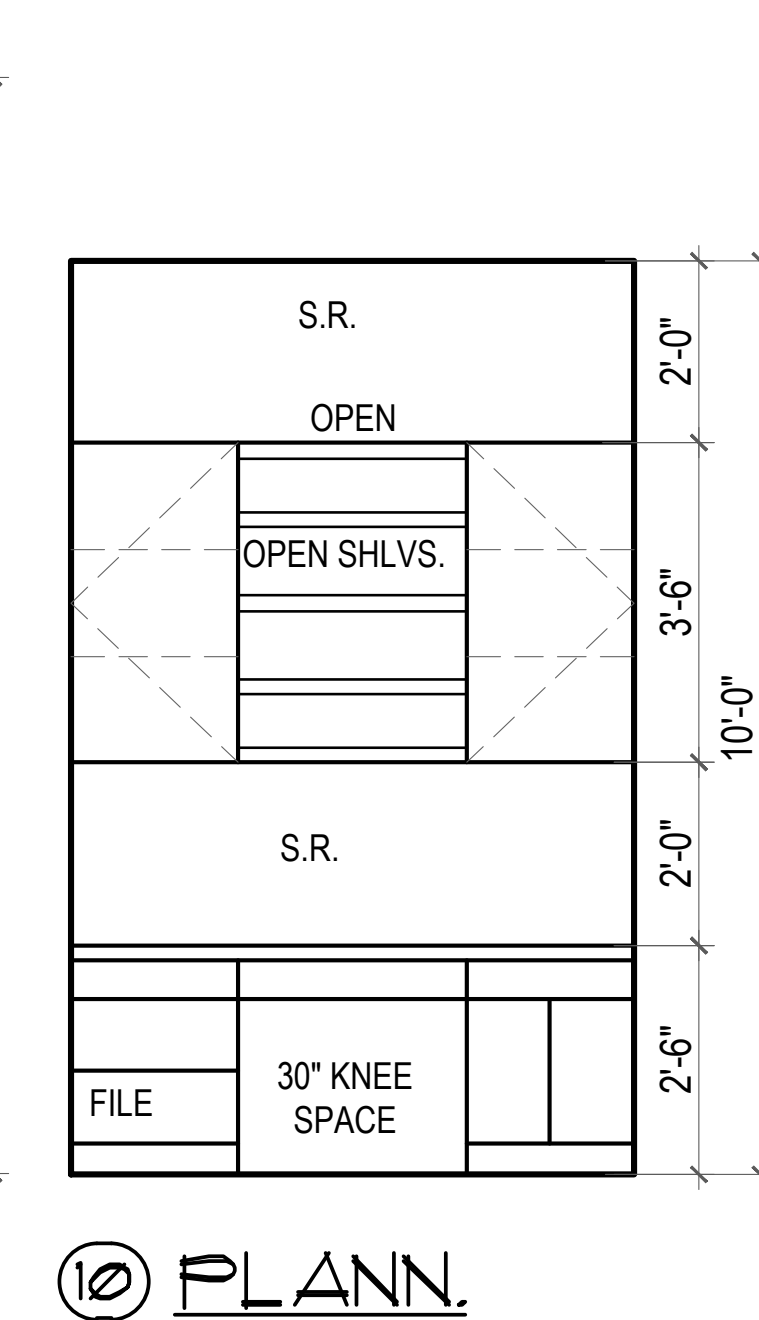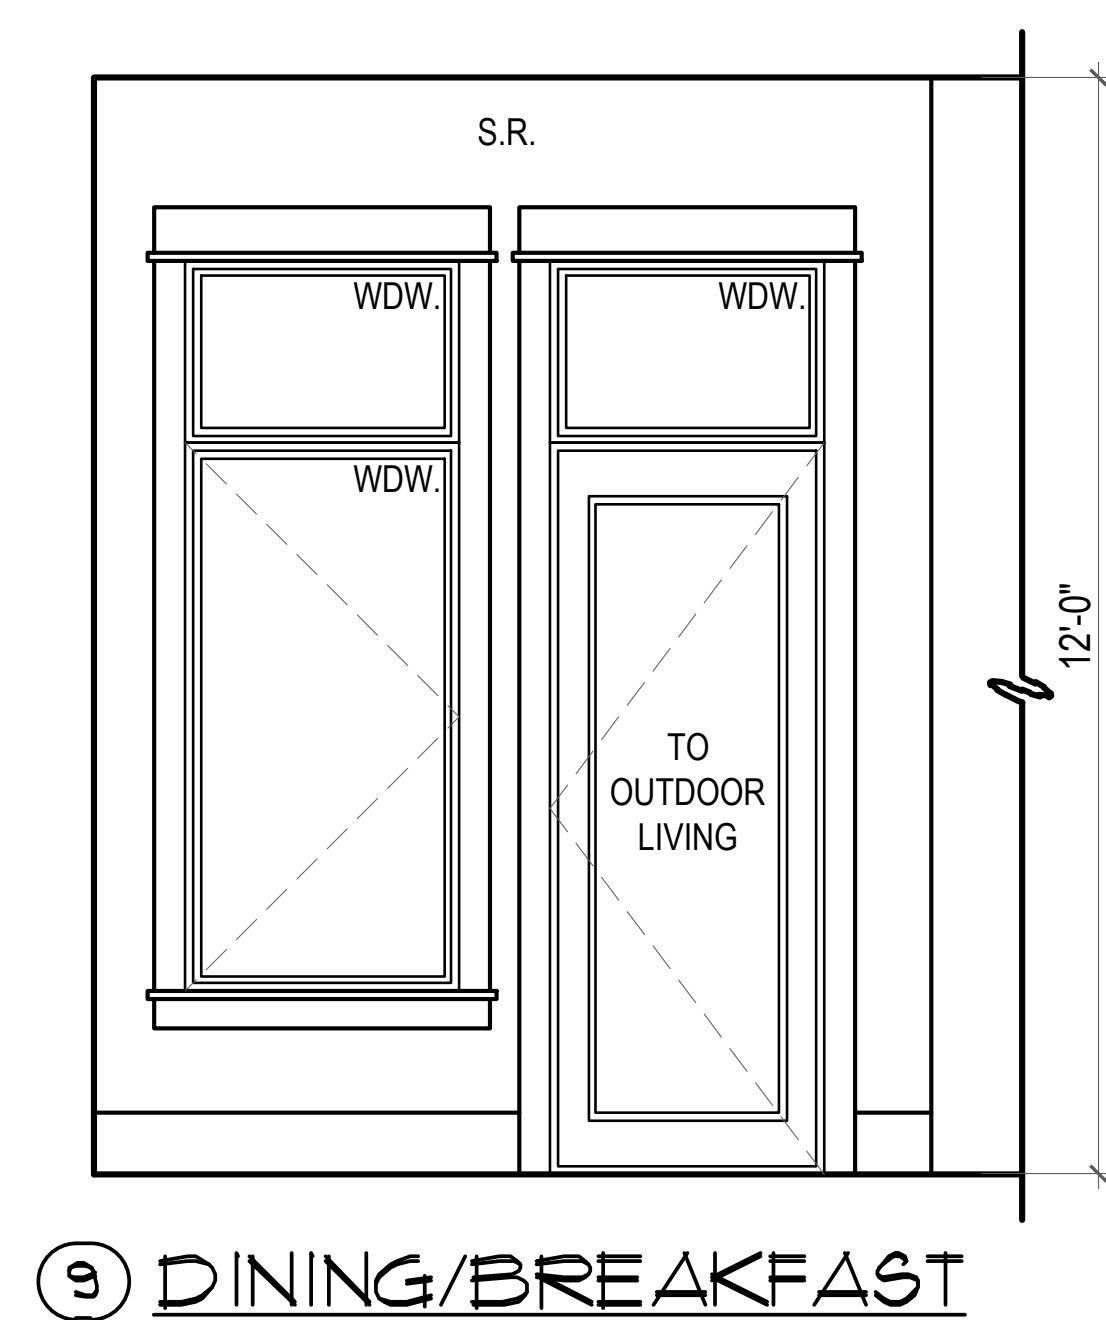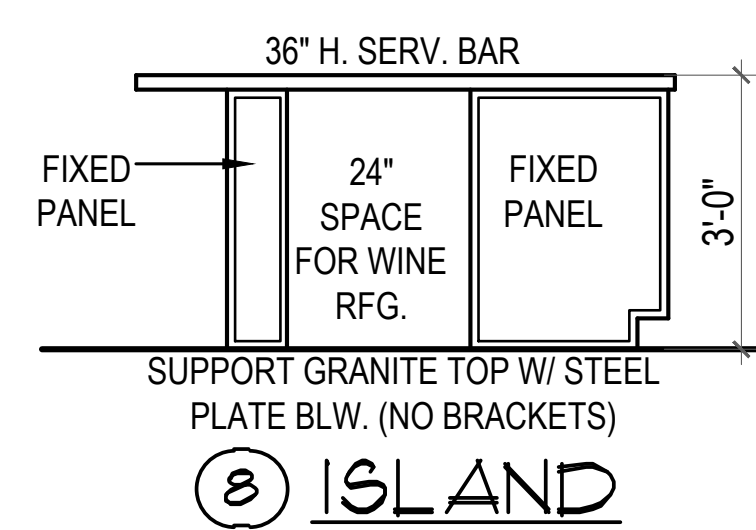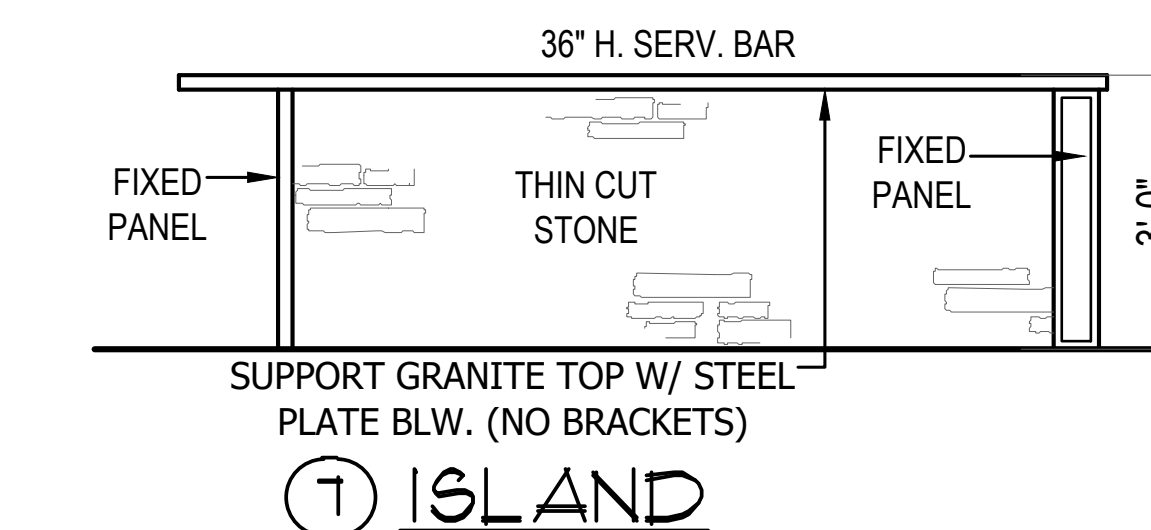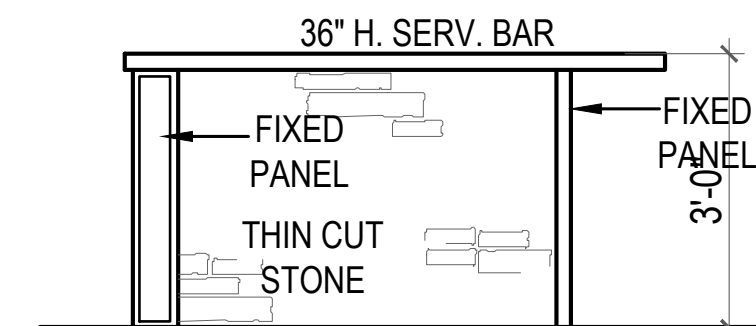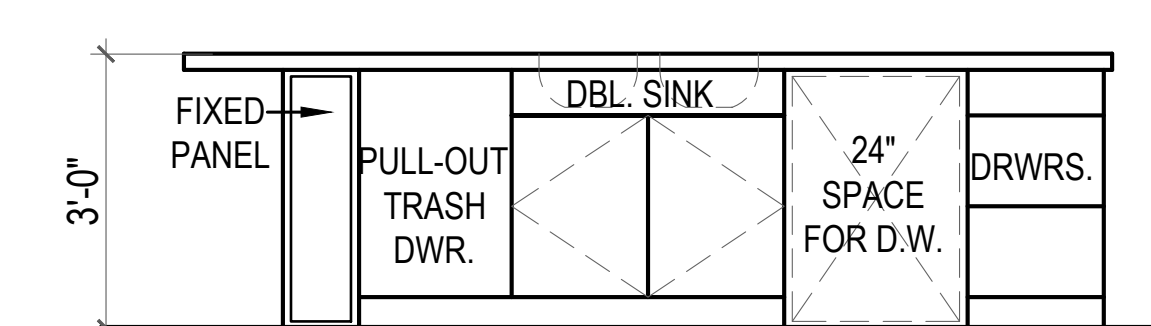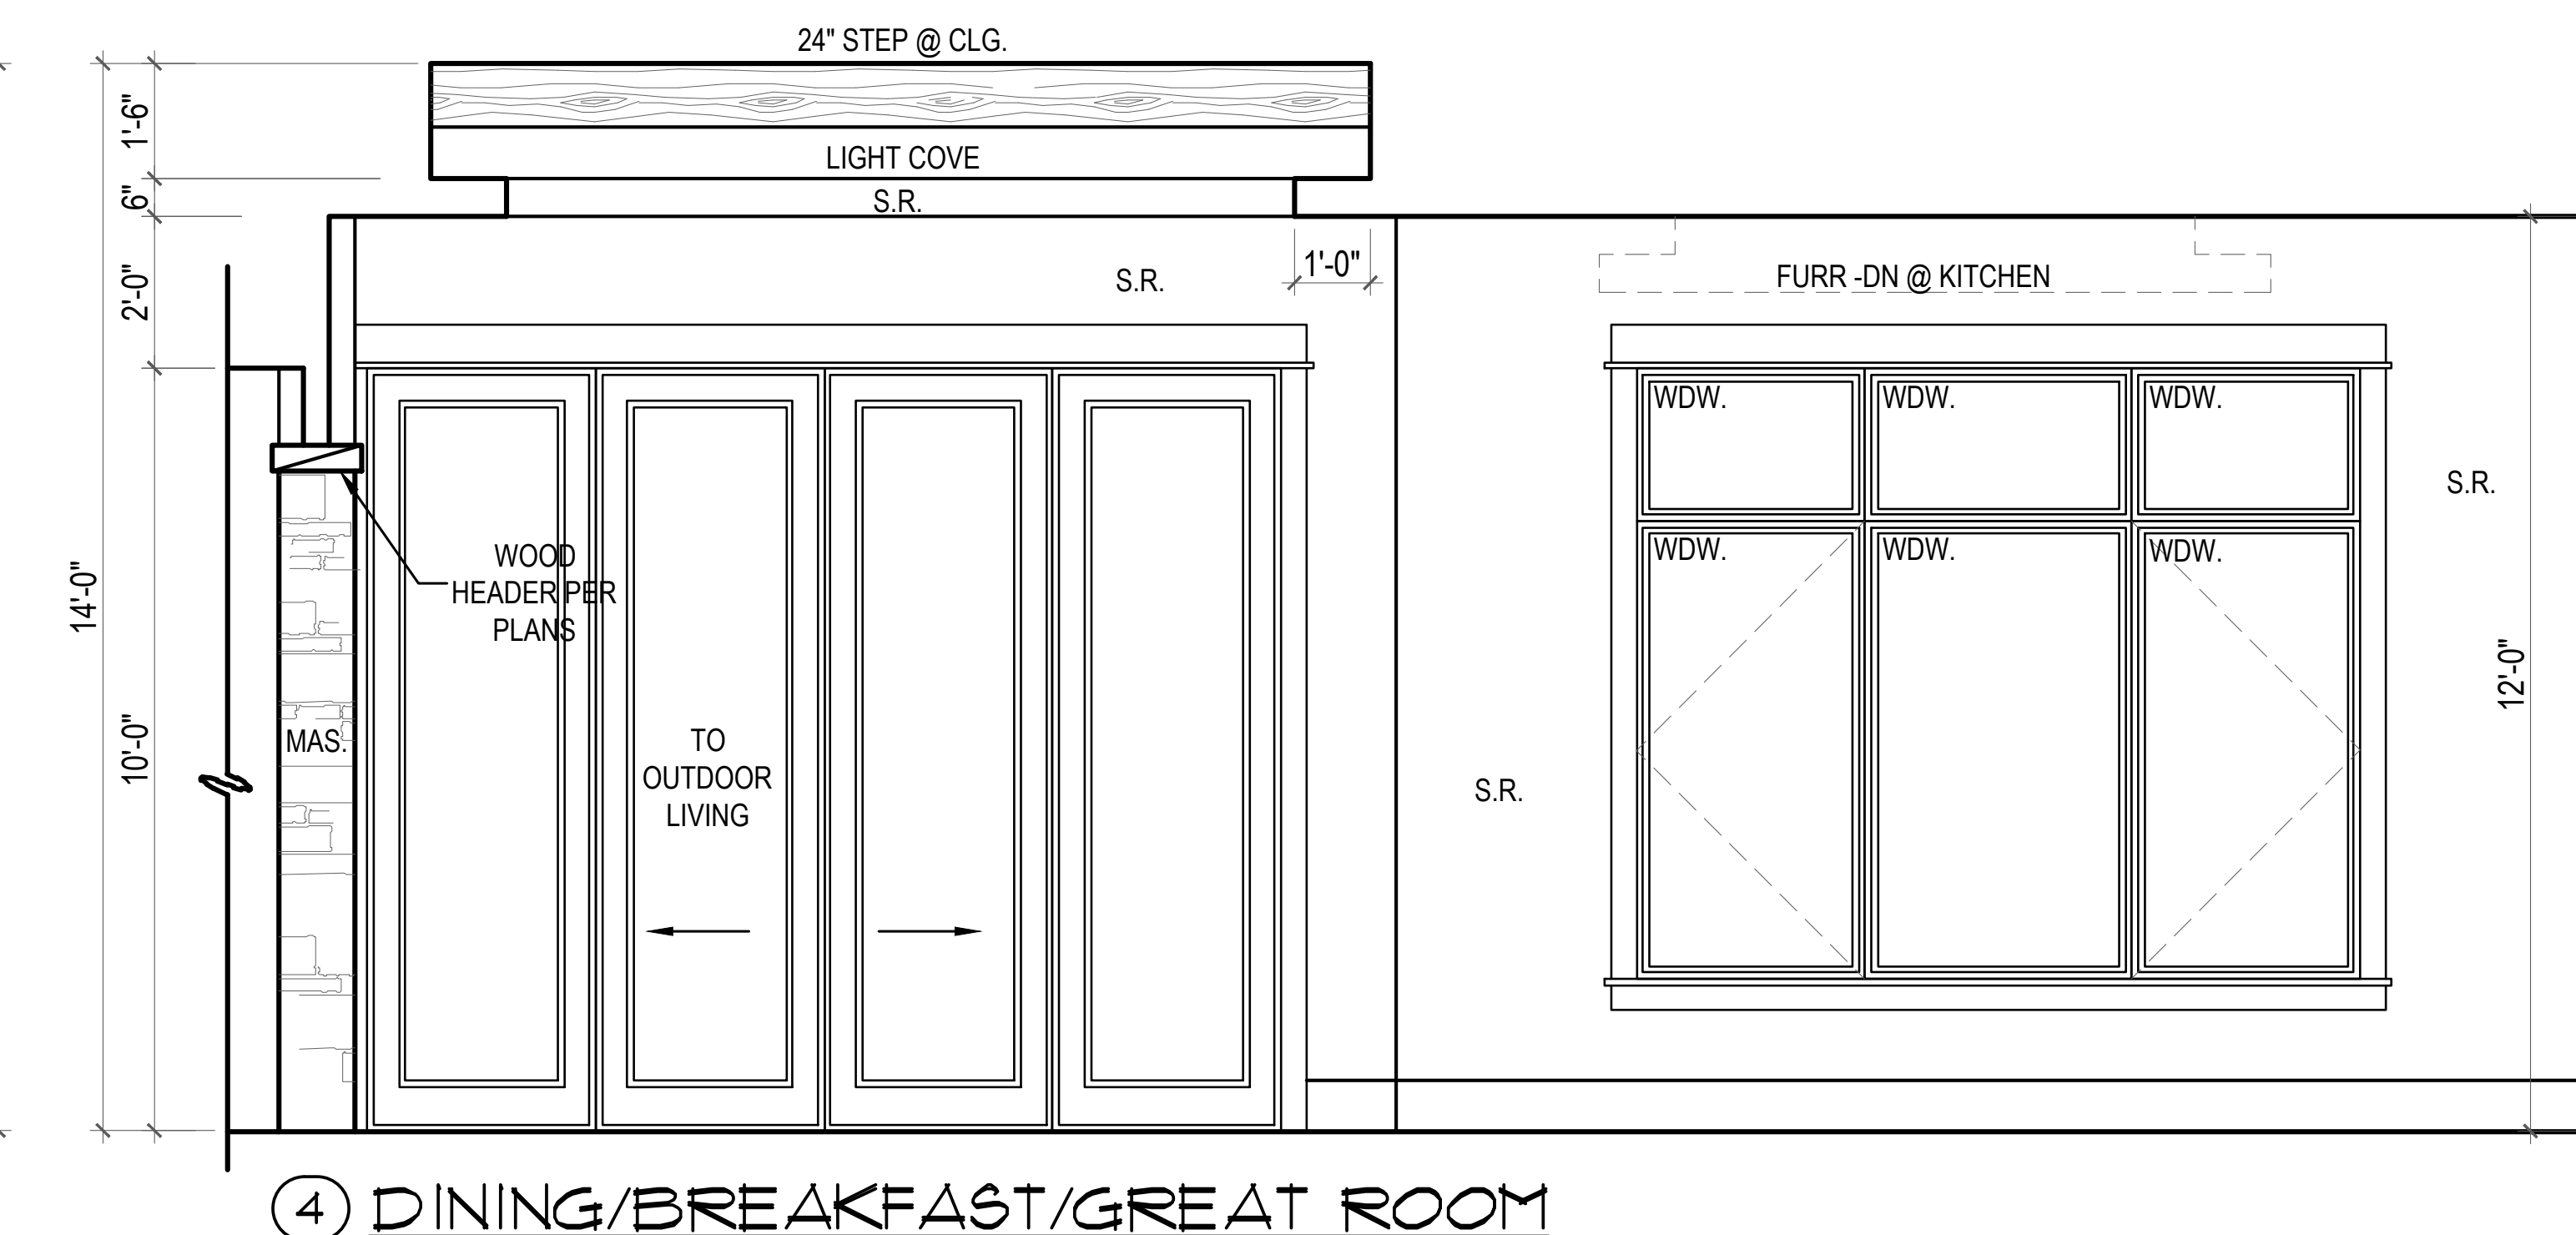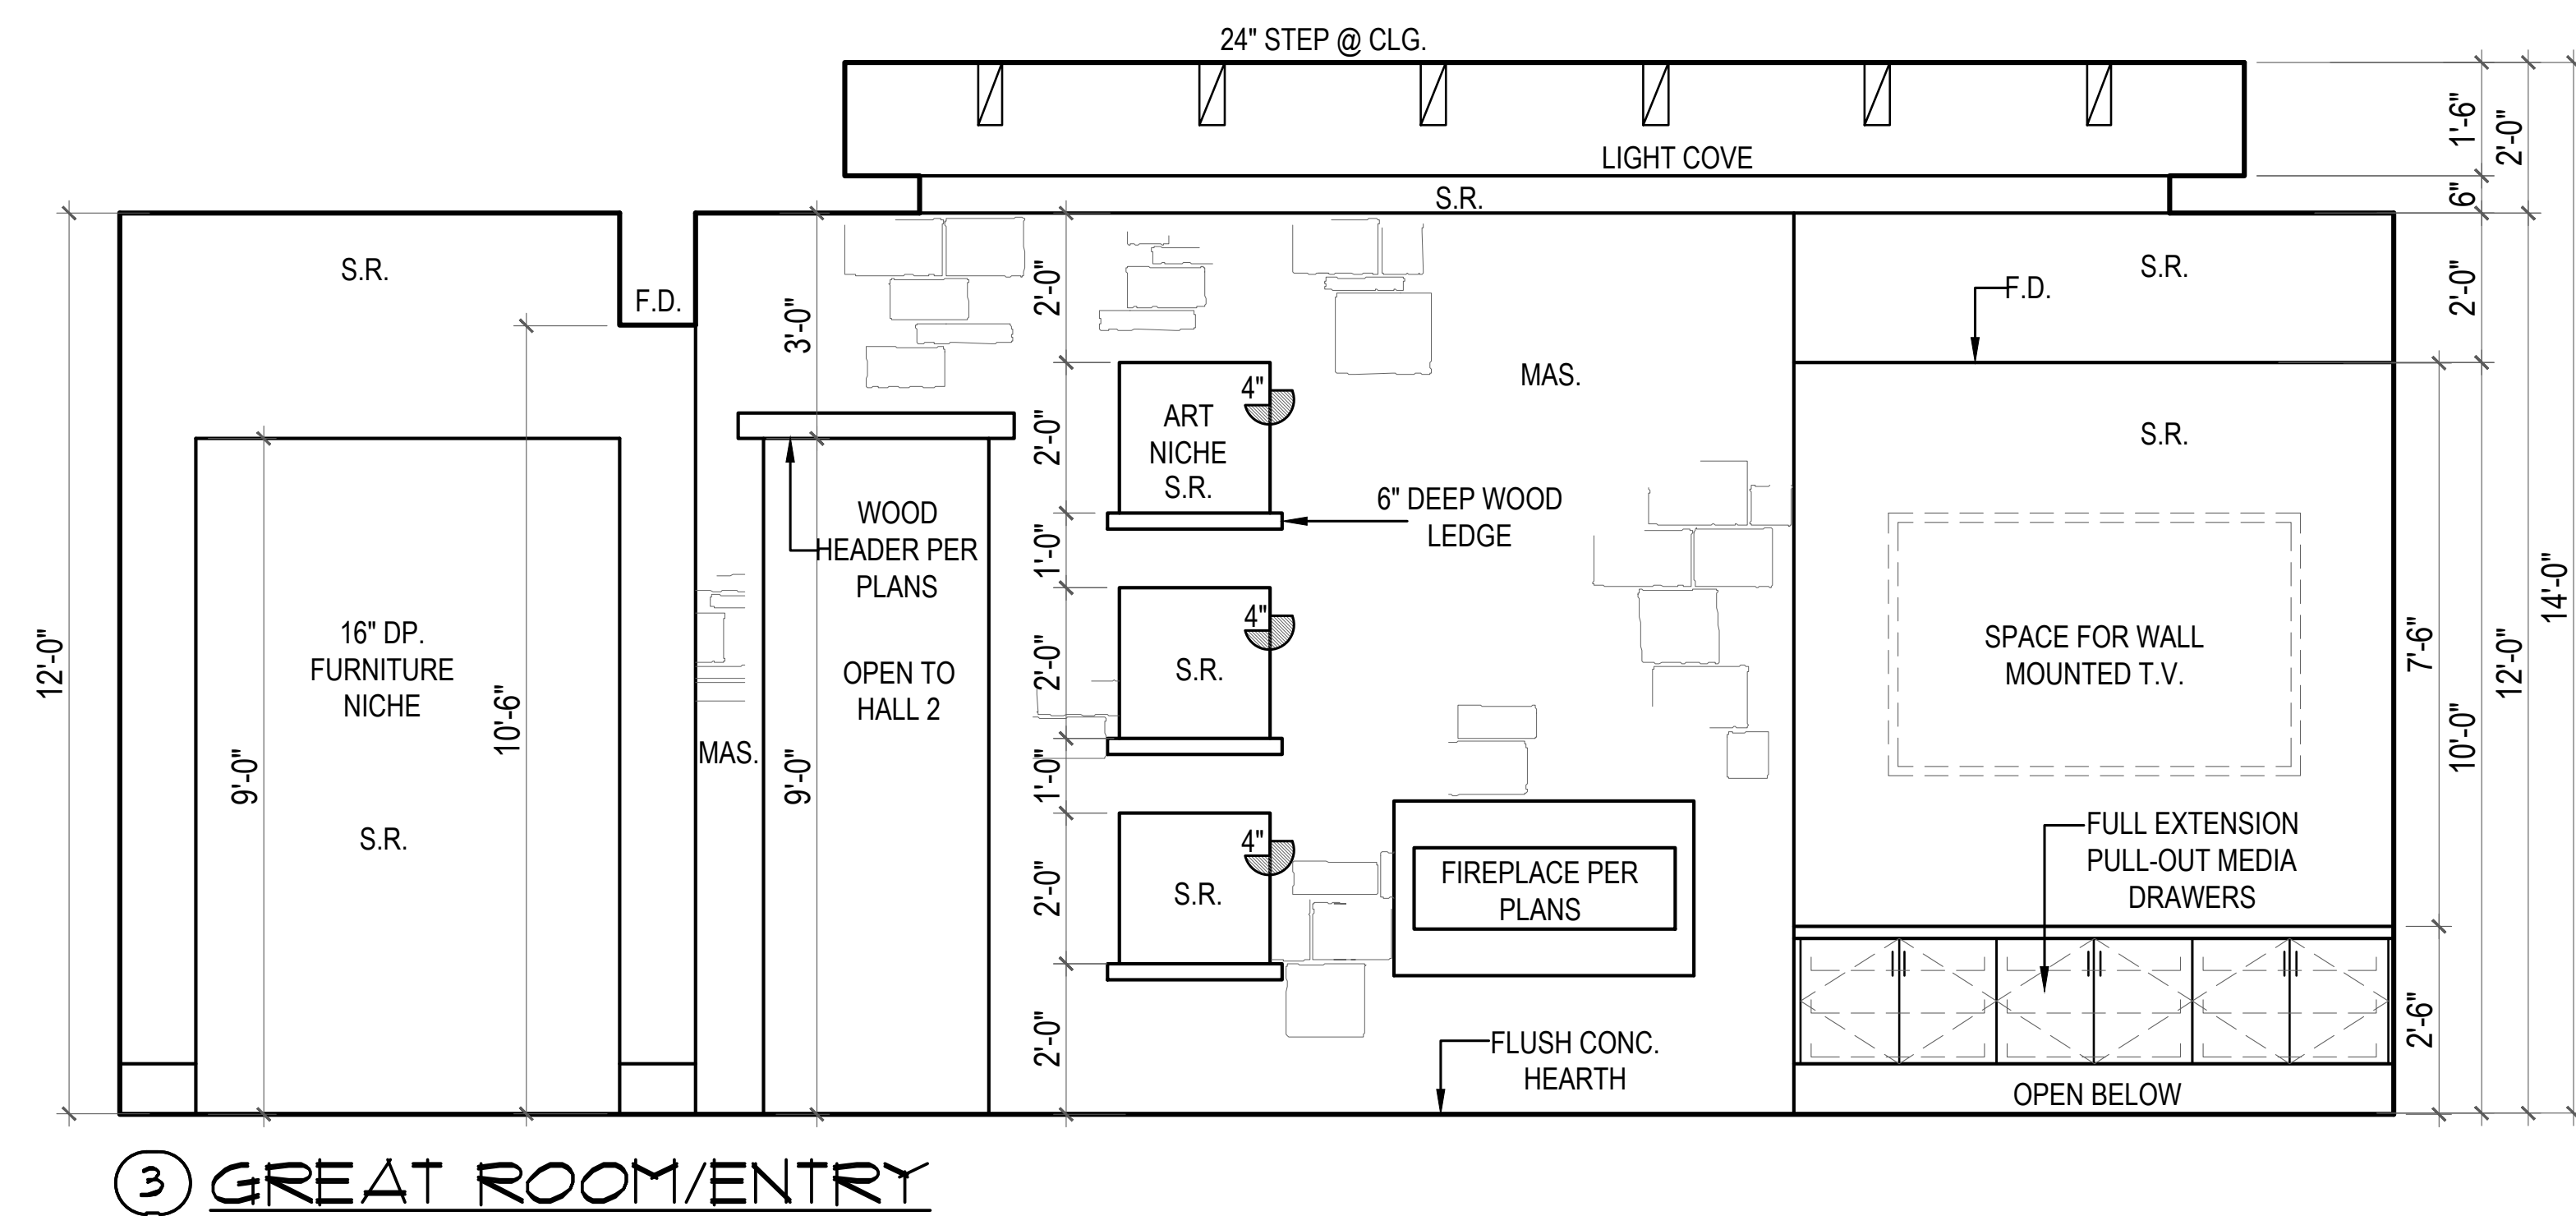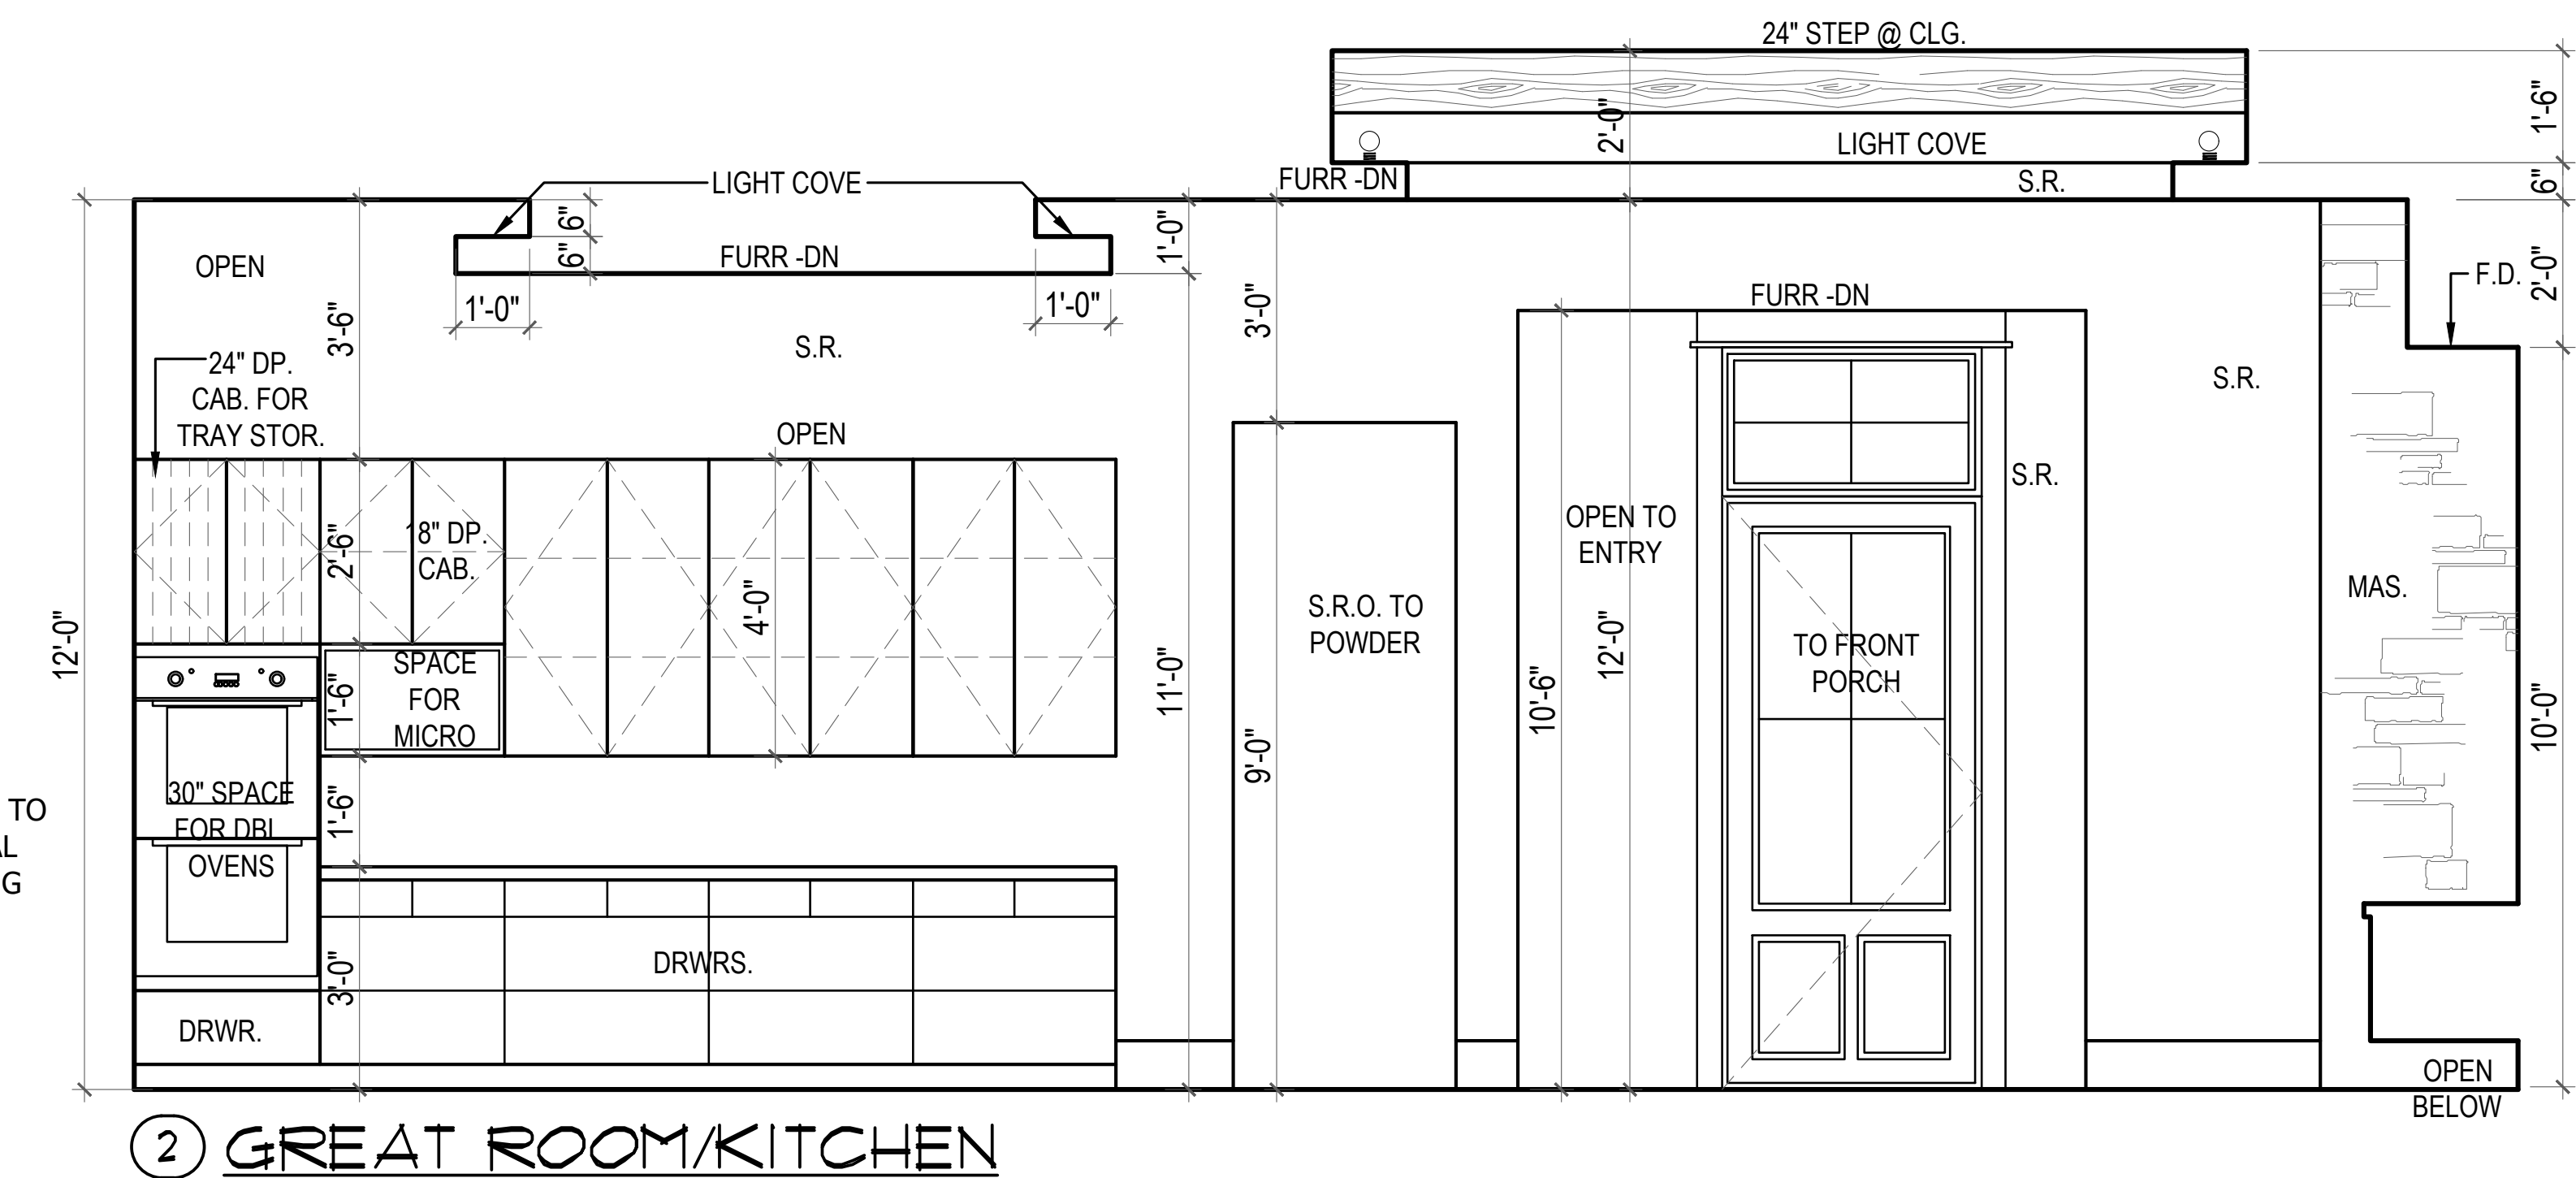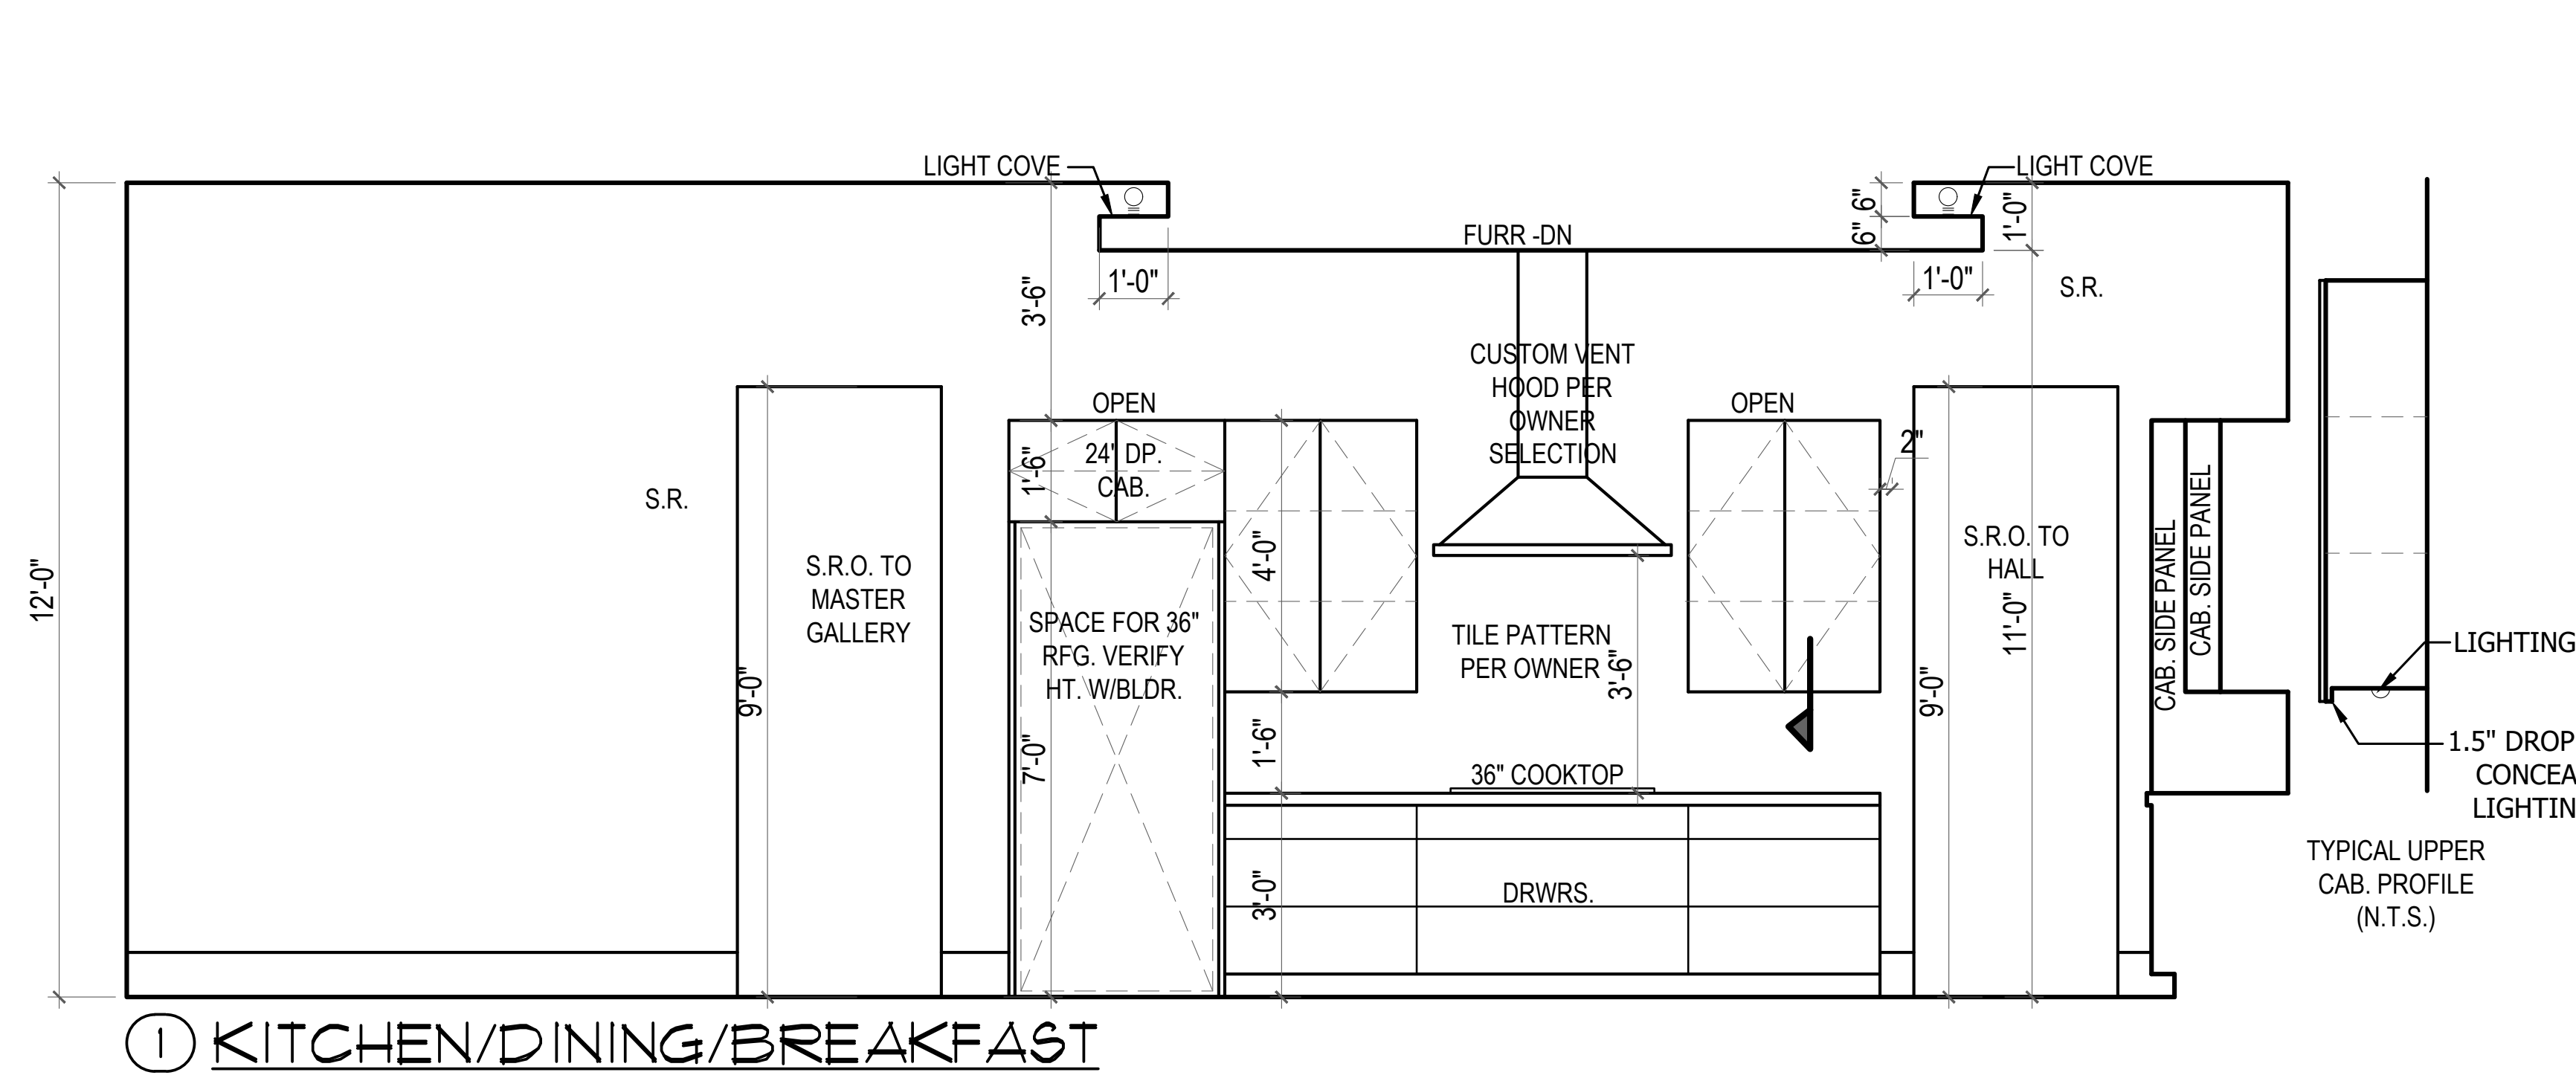


⑲ N/A


INTERIOR
ELEVATIONS
SCALE 3/8" = 1'-0"

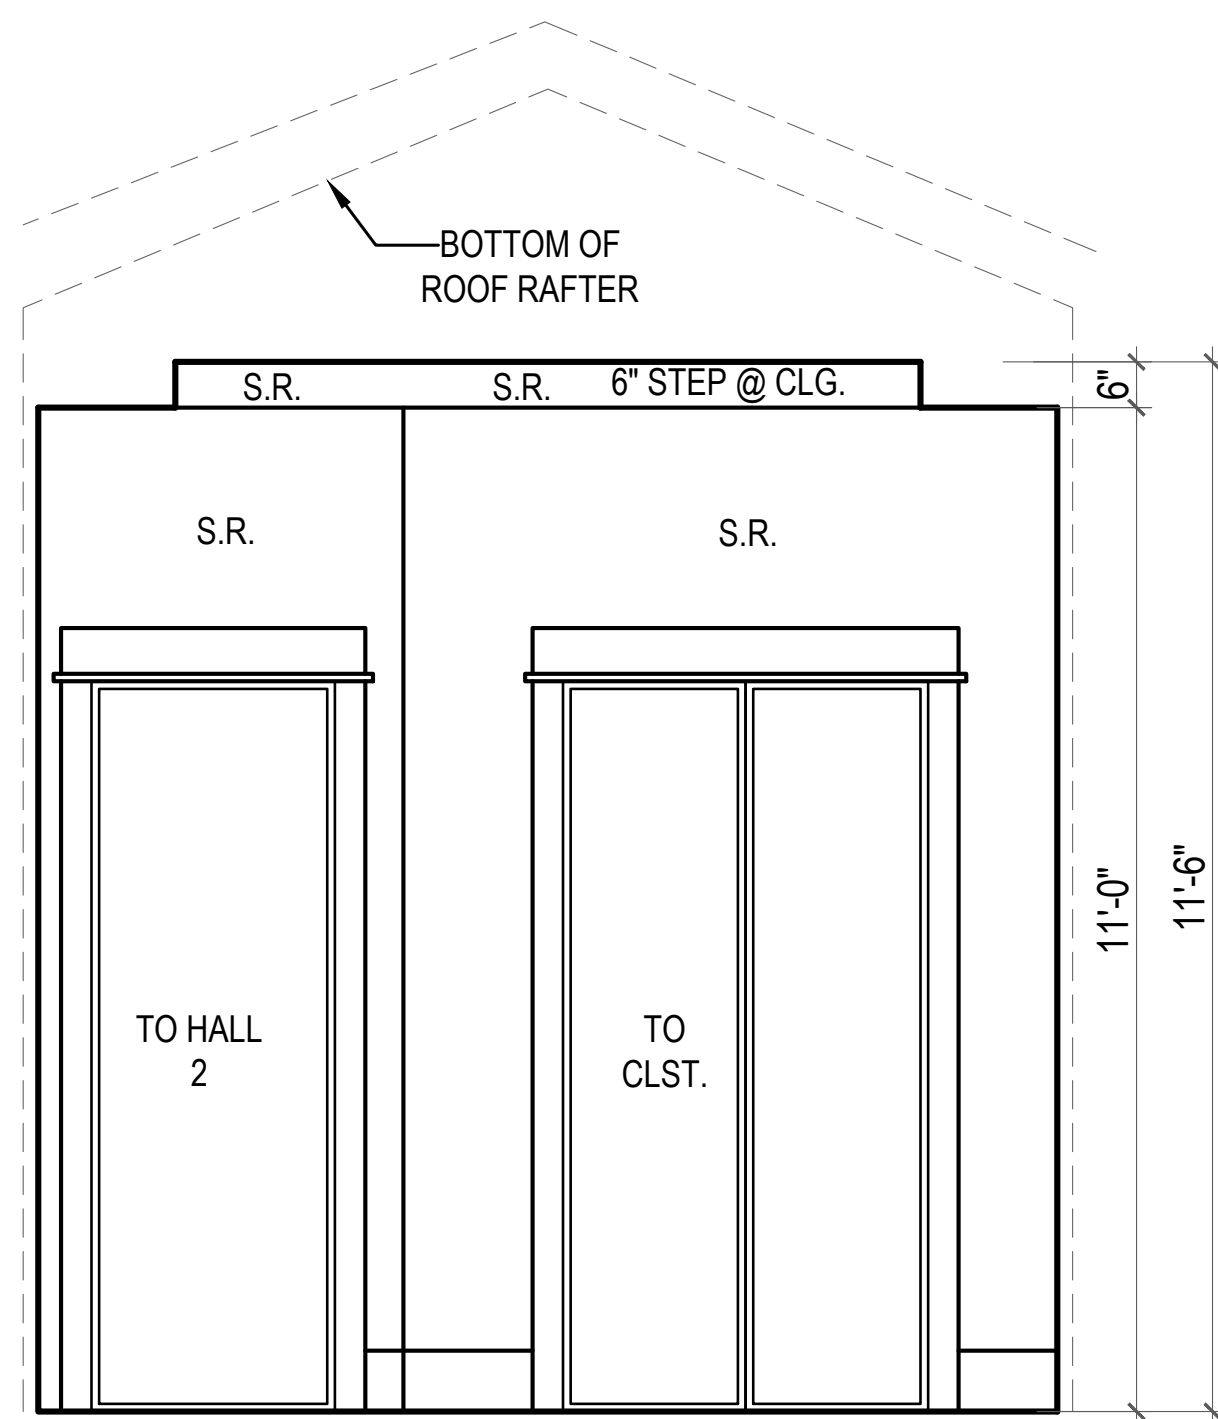


20 STUDY

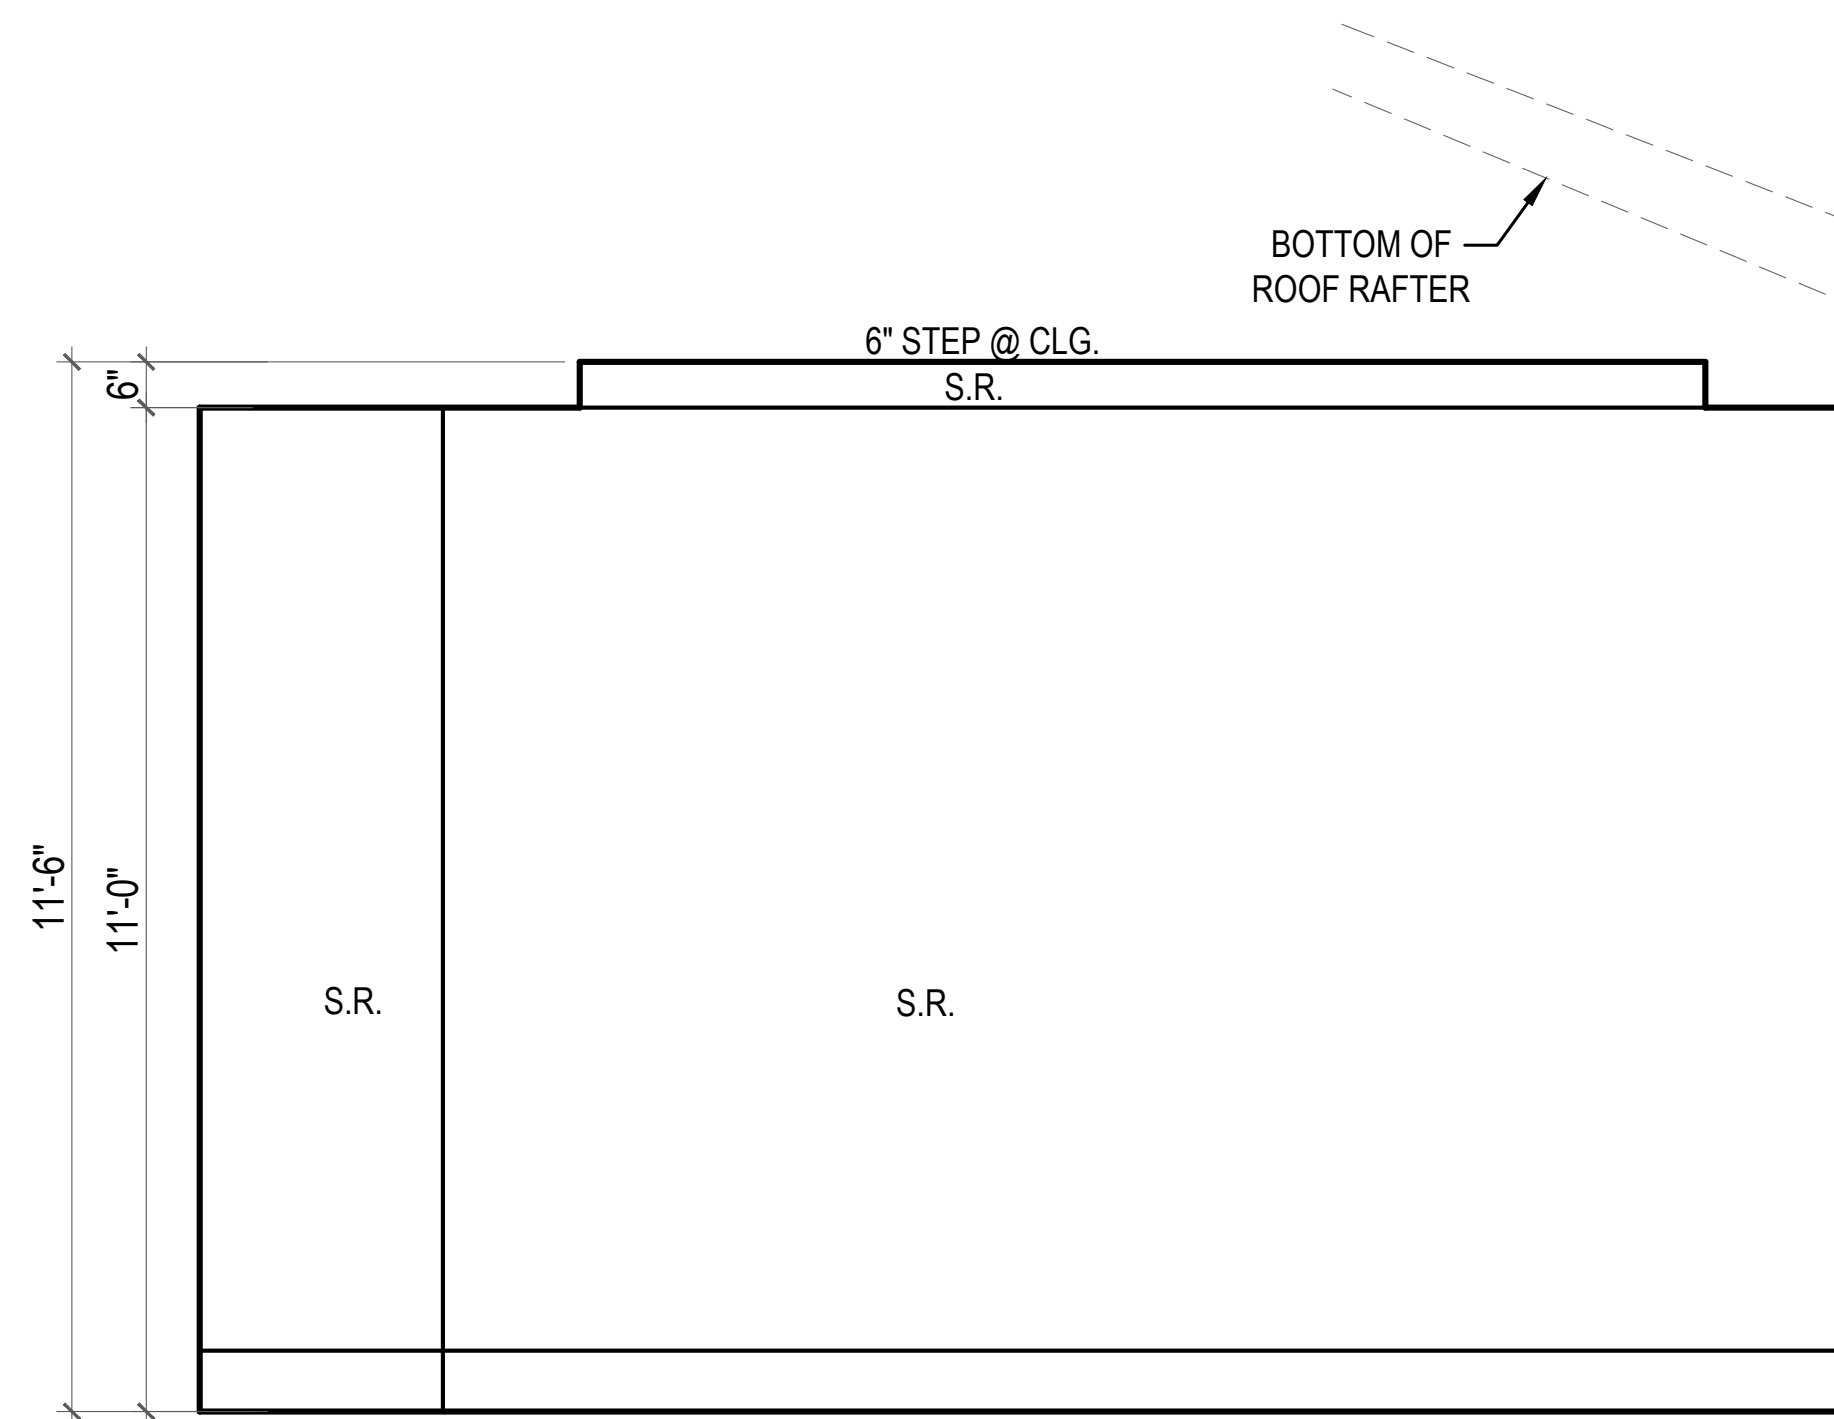


21 STUDY

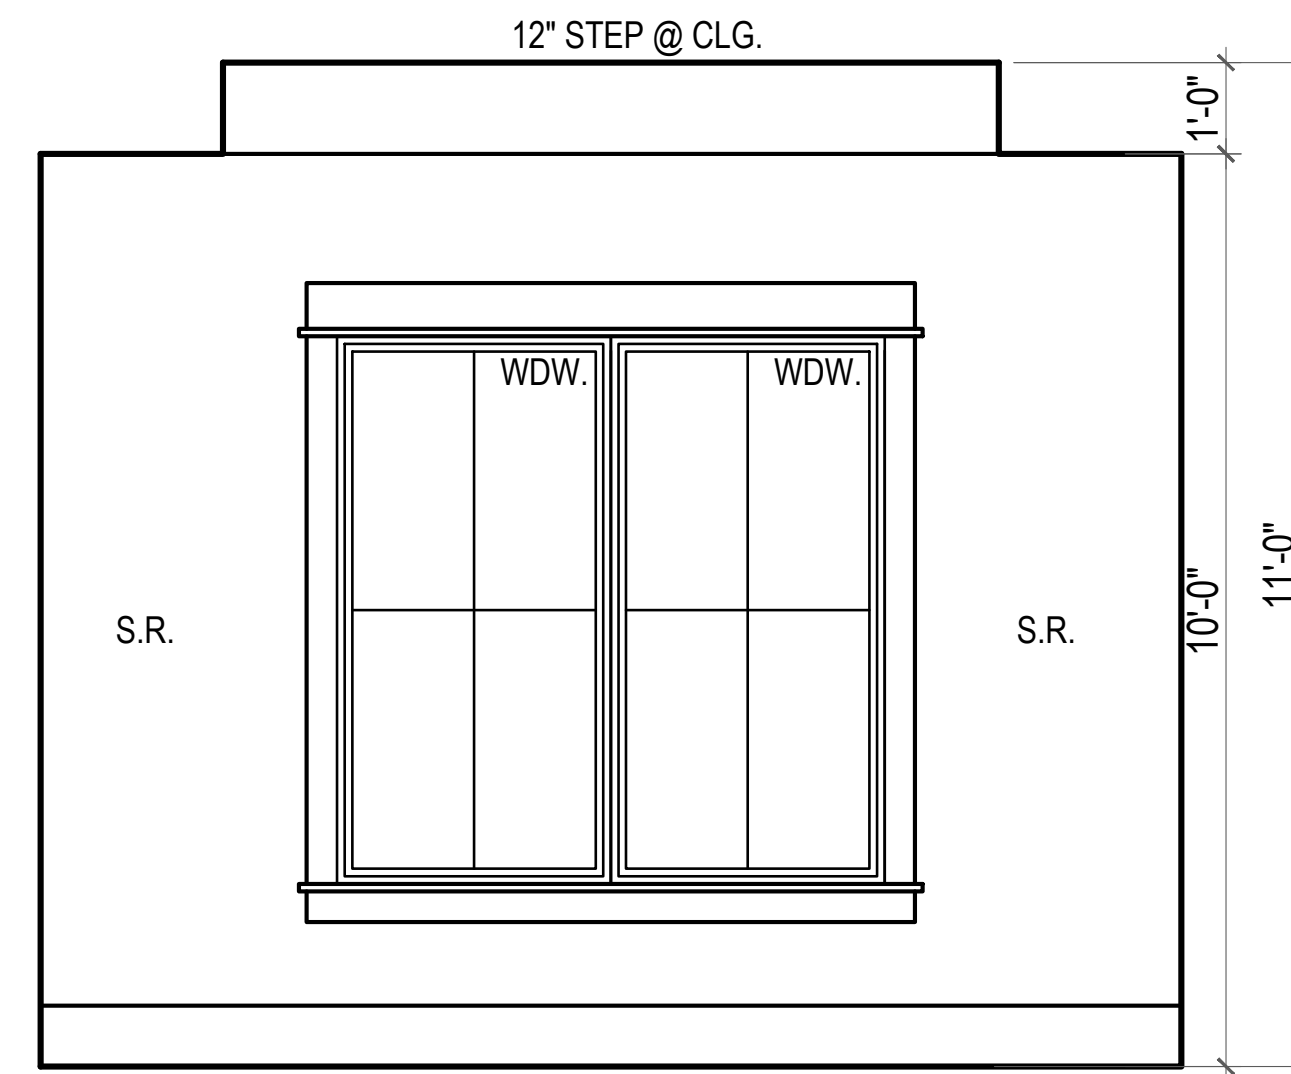


22 BEDROOM 4

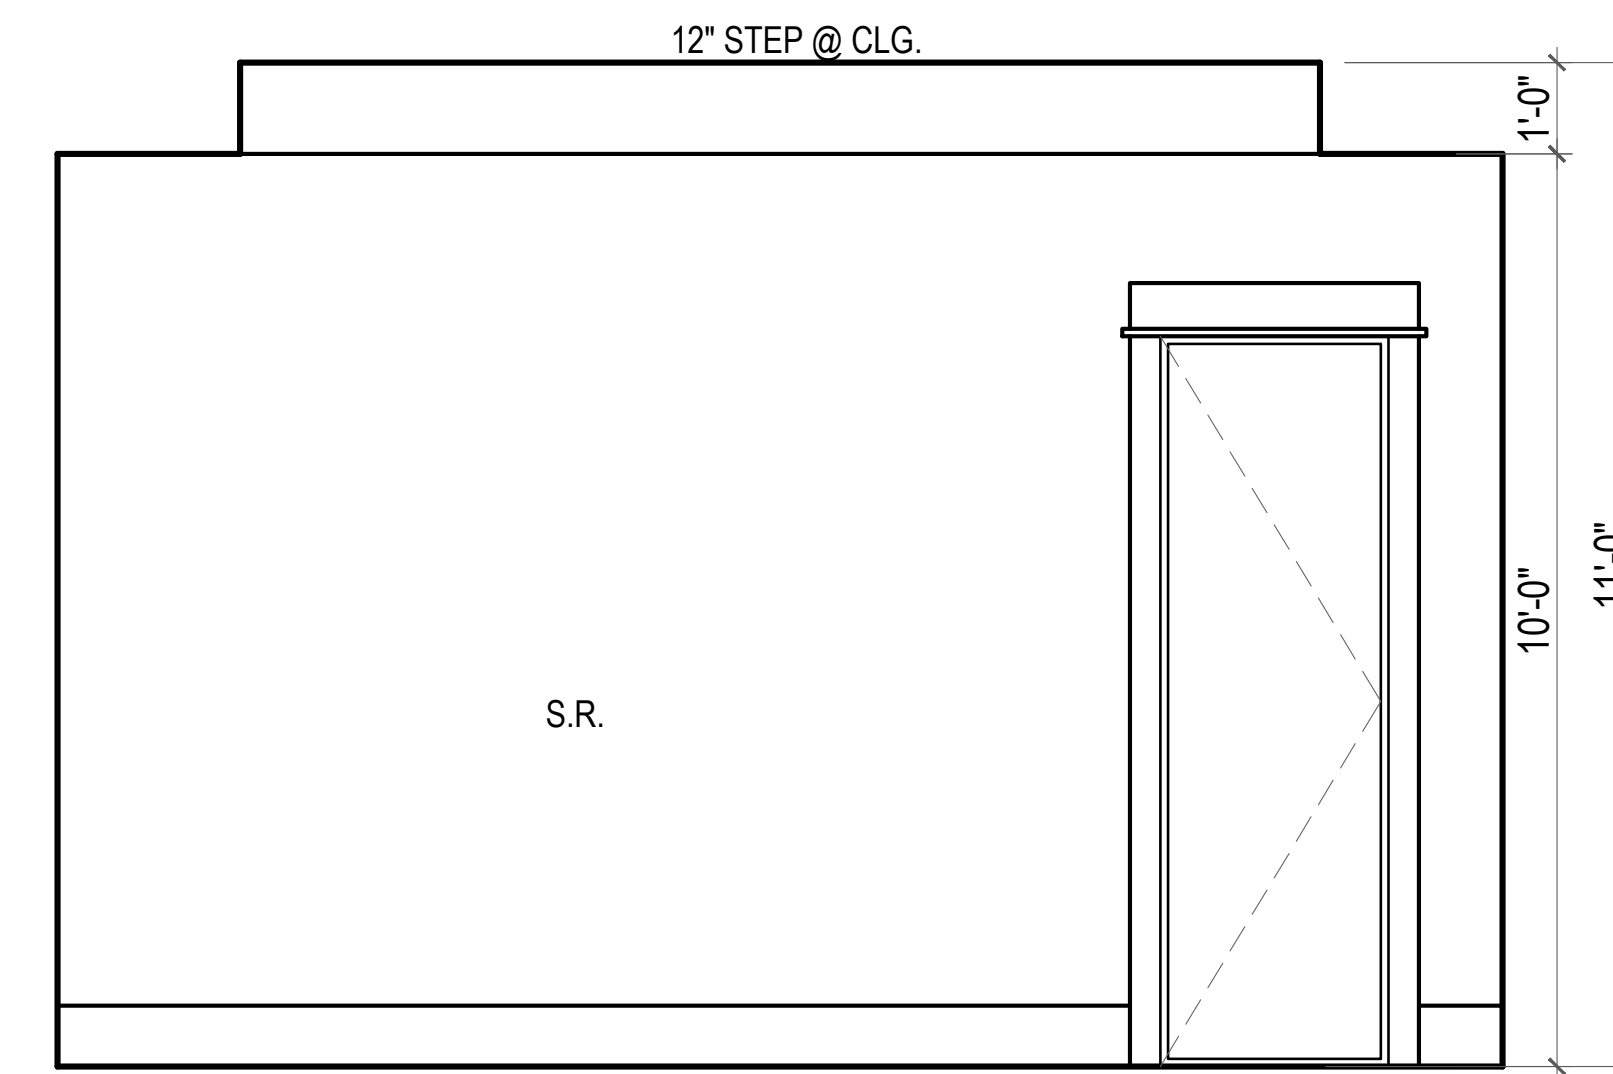


23 BEDROOM 4

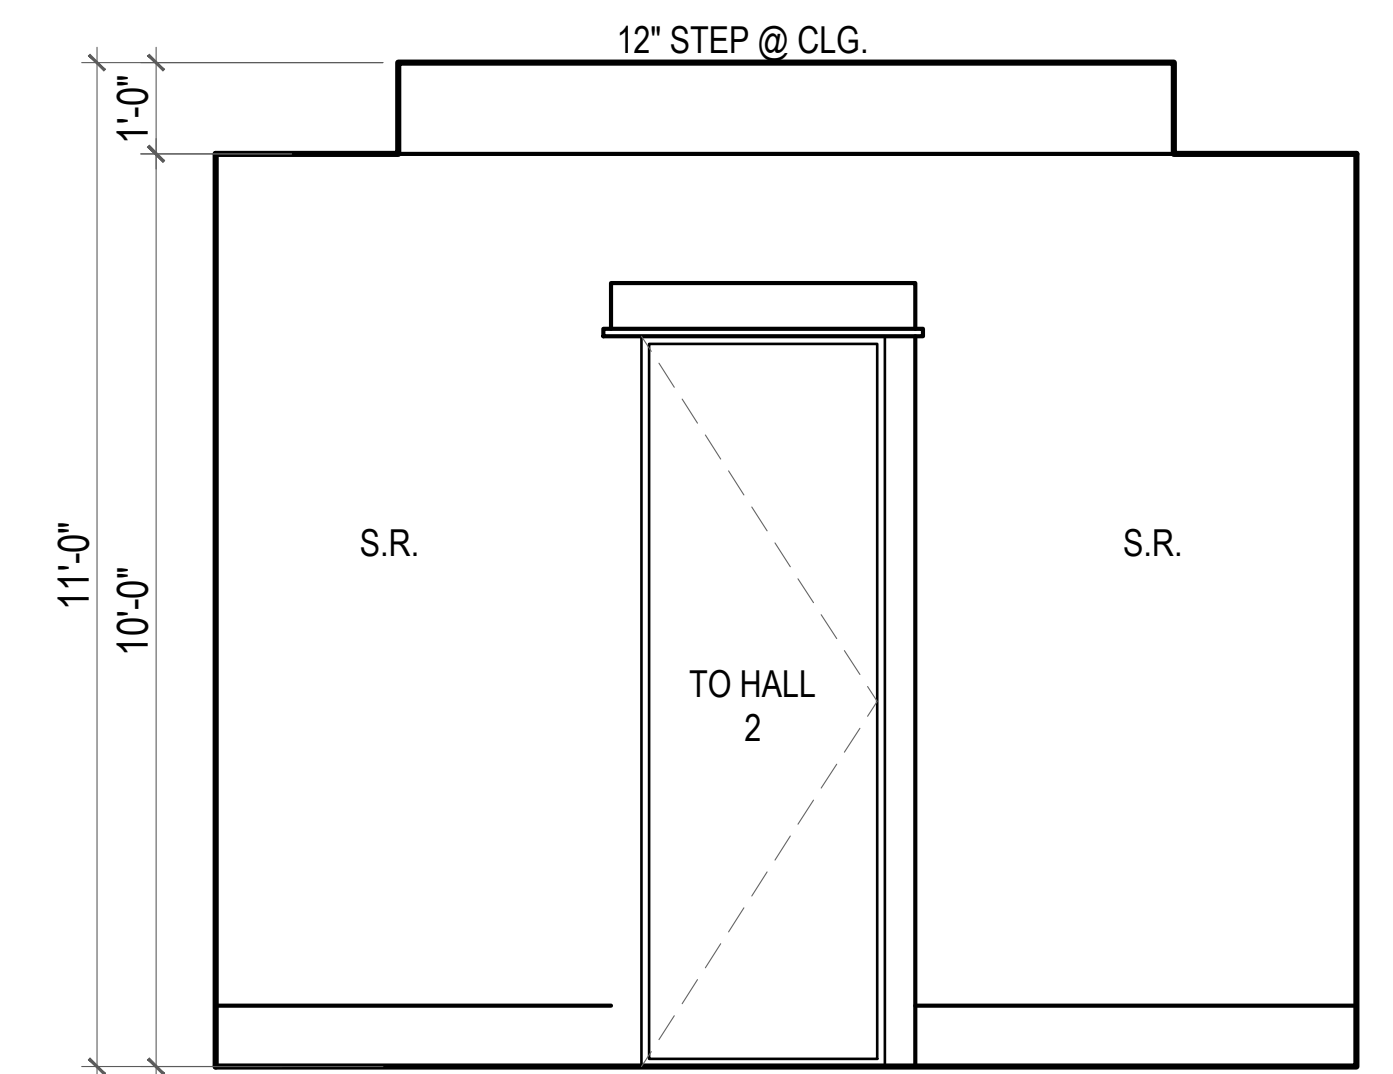


24 BEDROOM 4

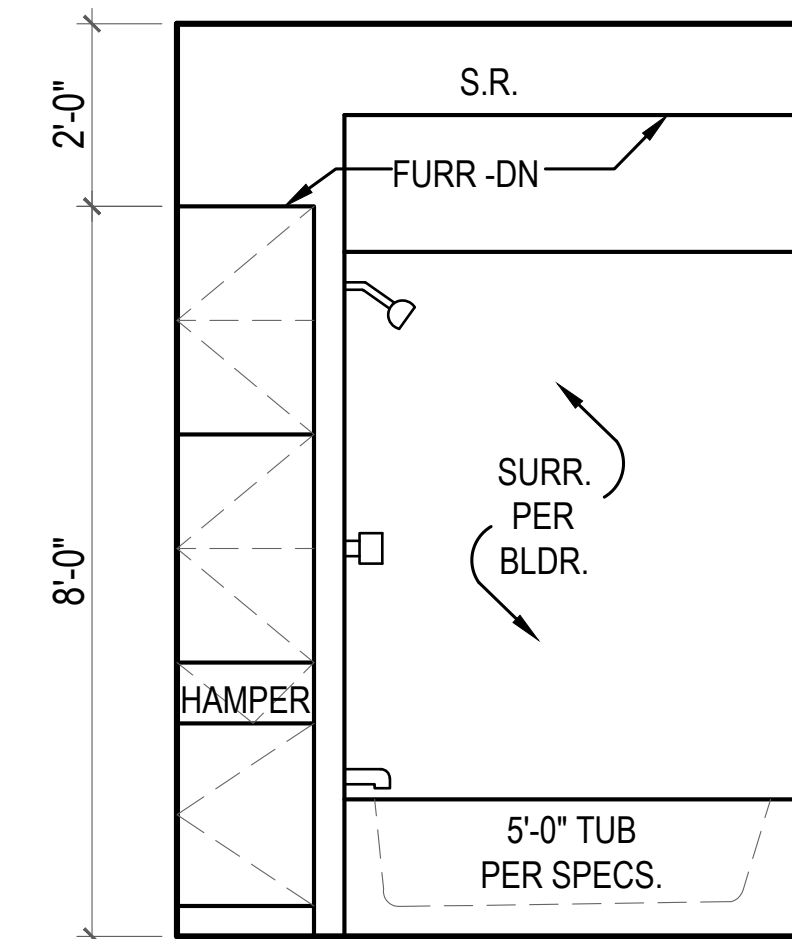


25 BATH 4

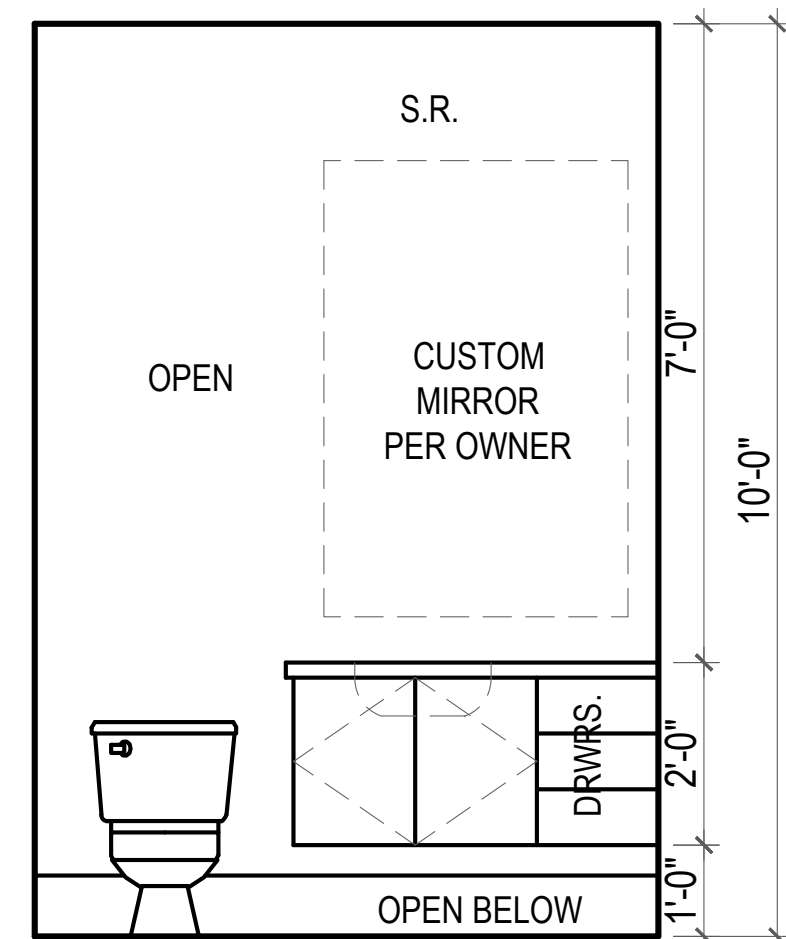


26 BATH 4

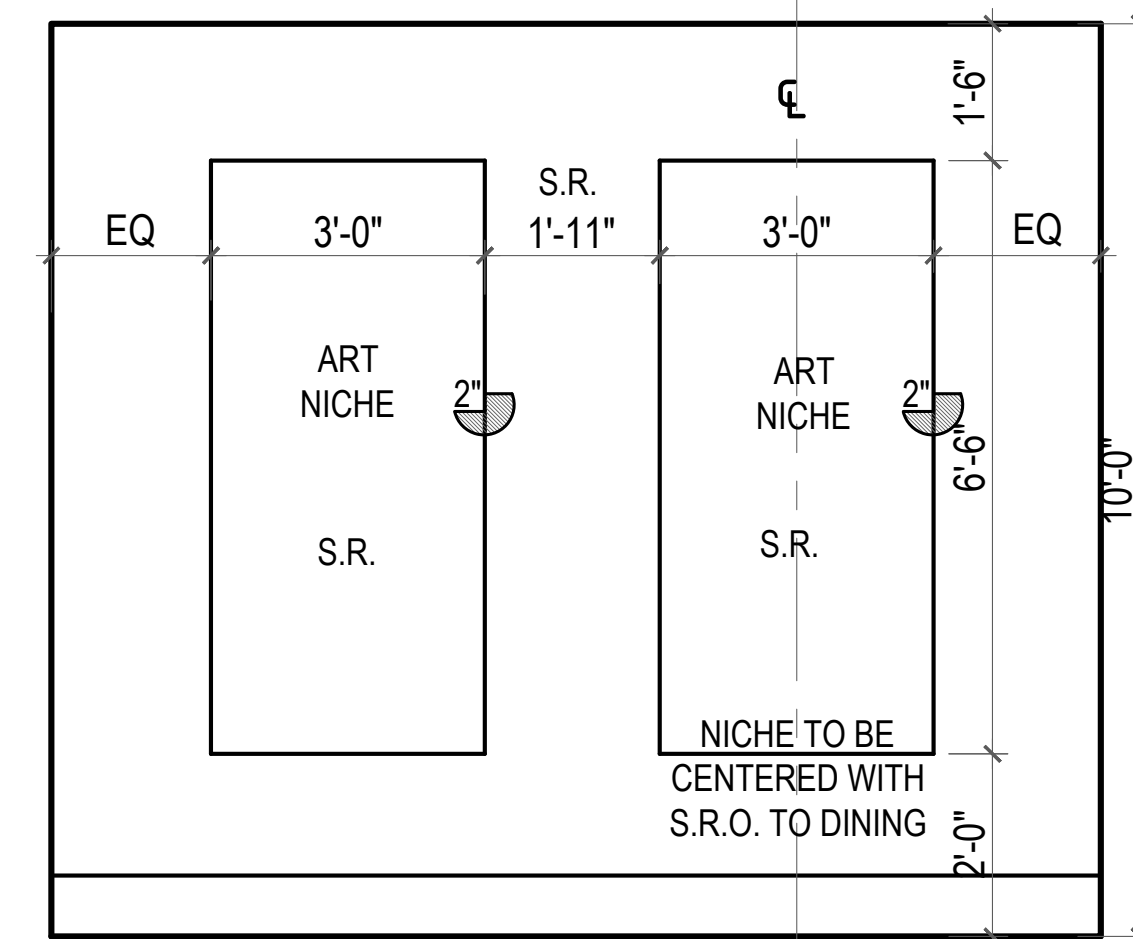


27 MASTER GALLERY

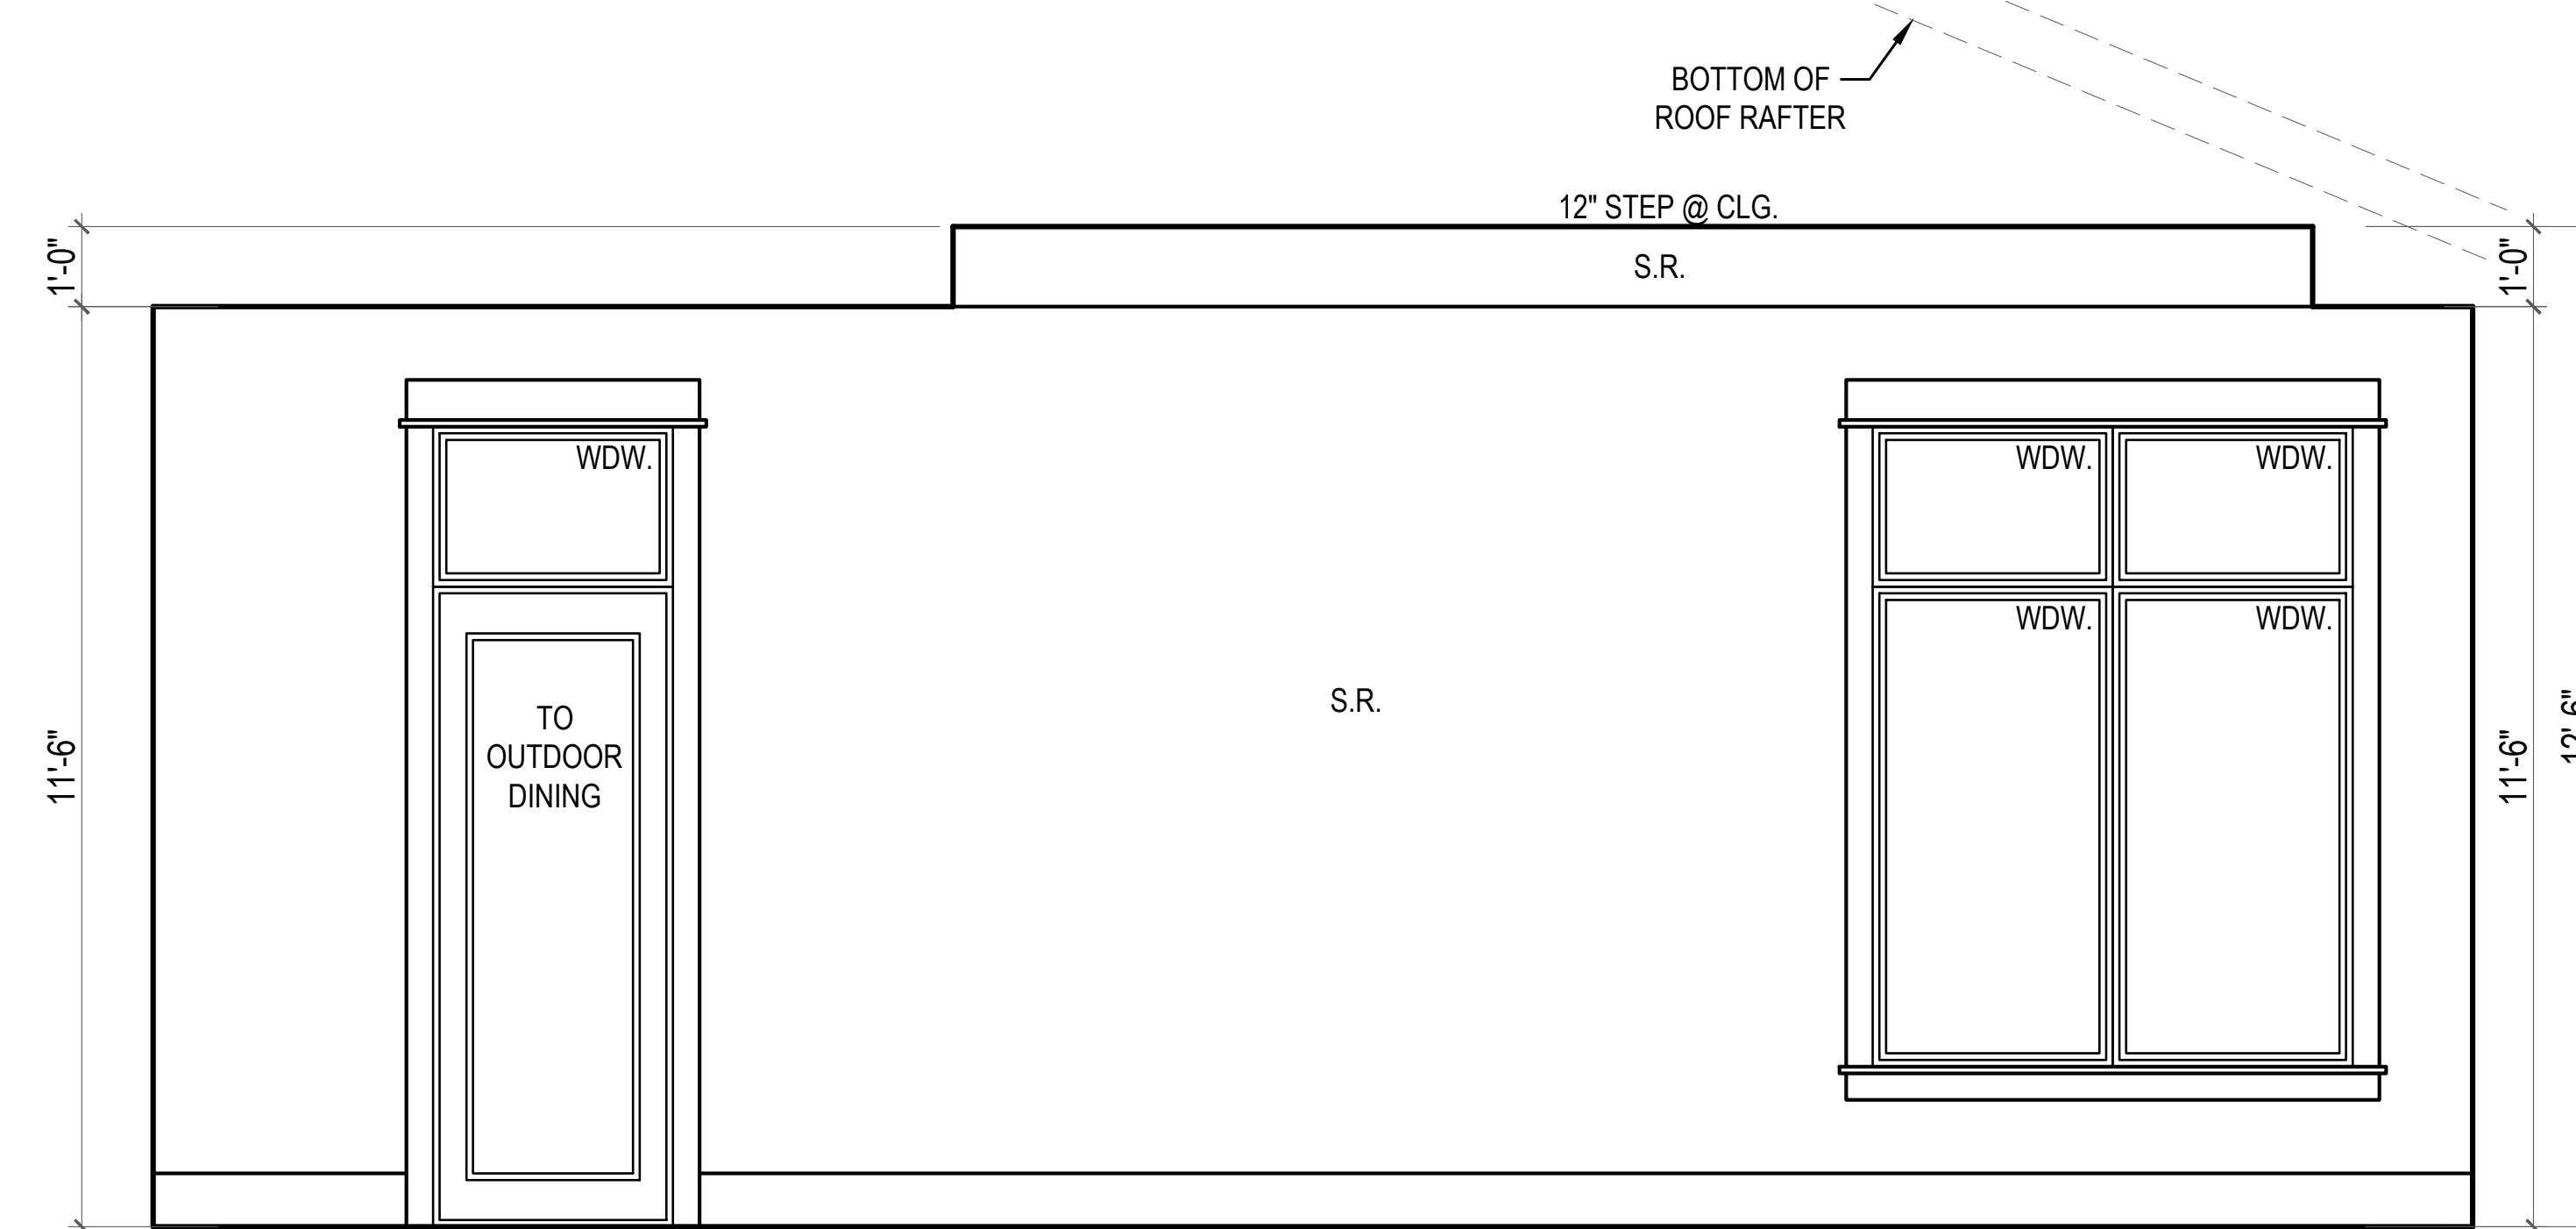


28 MASTER

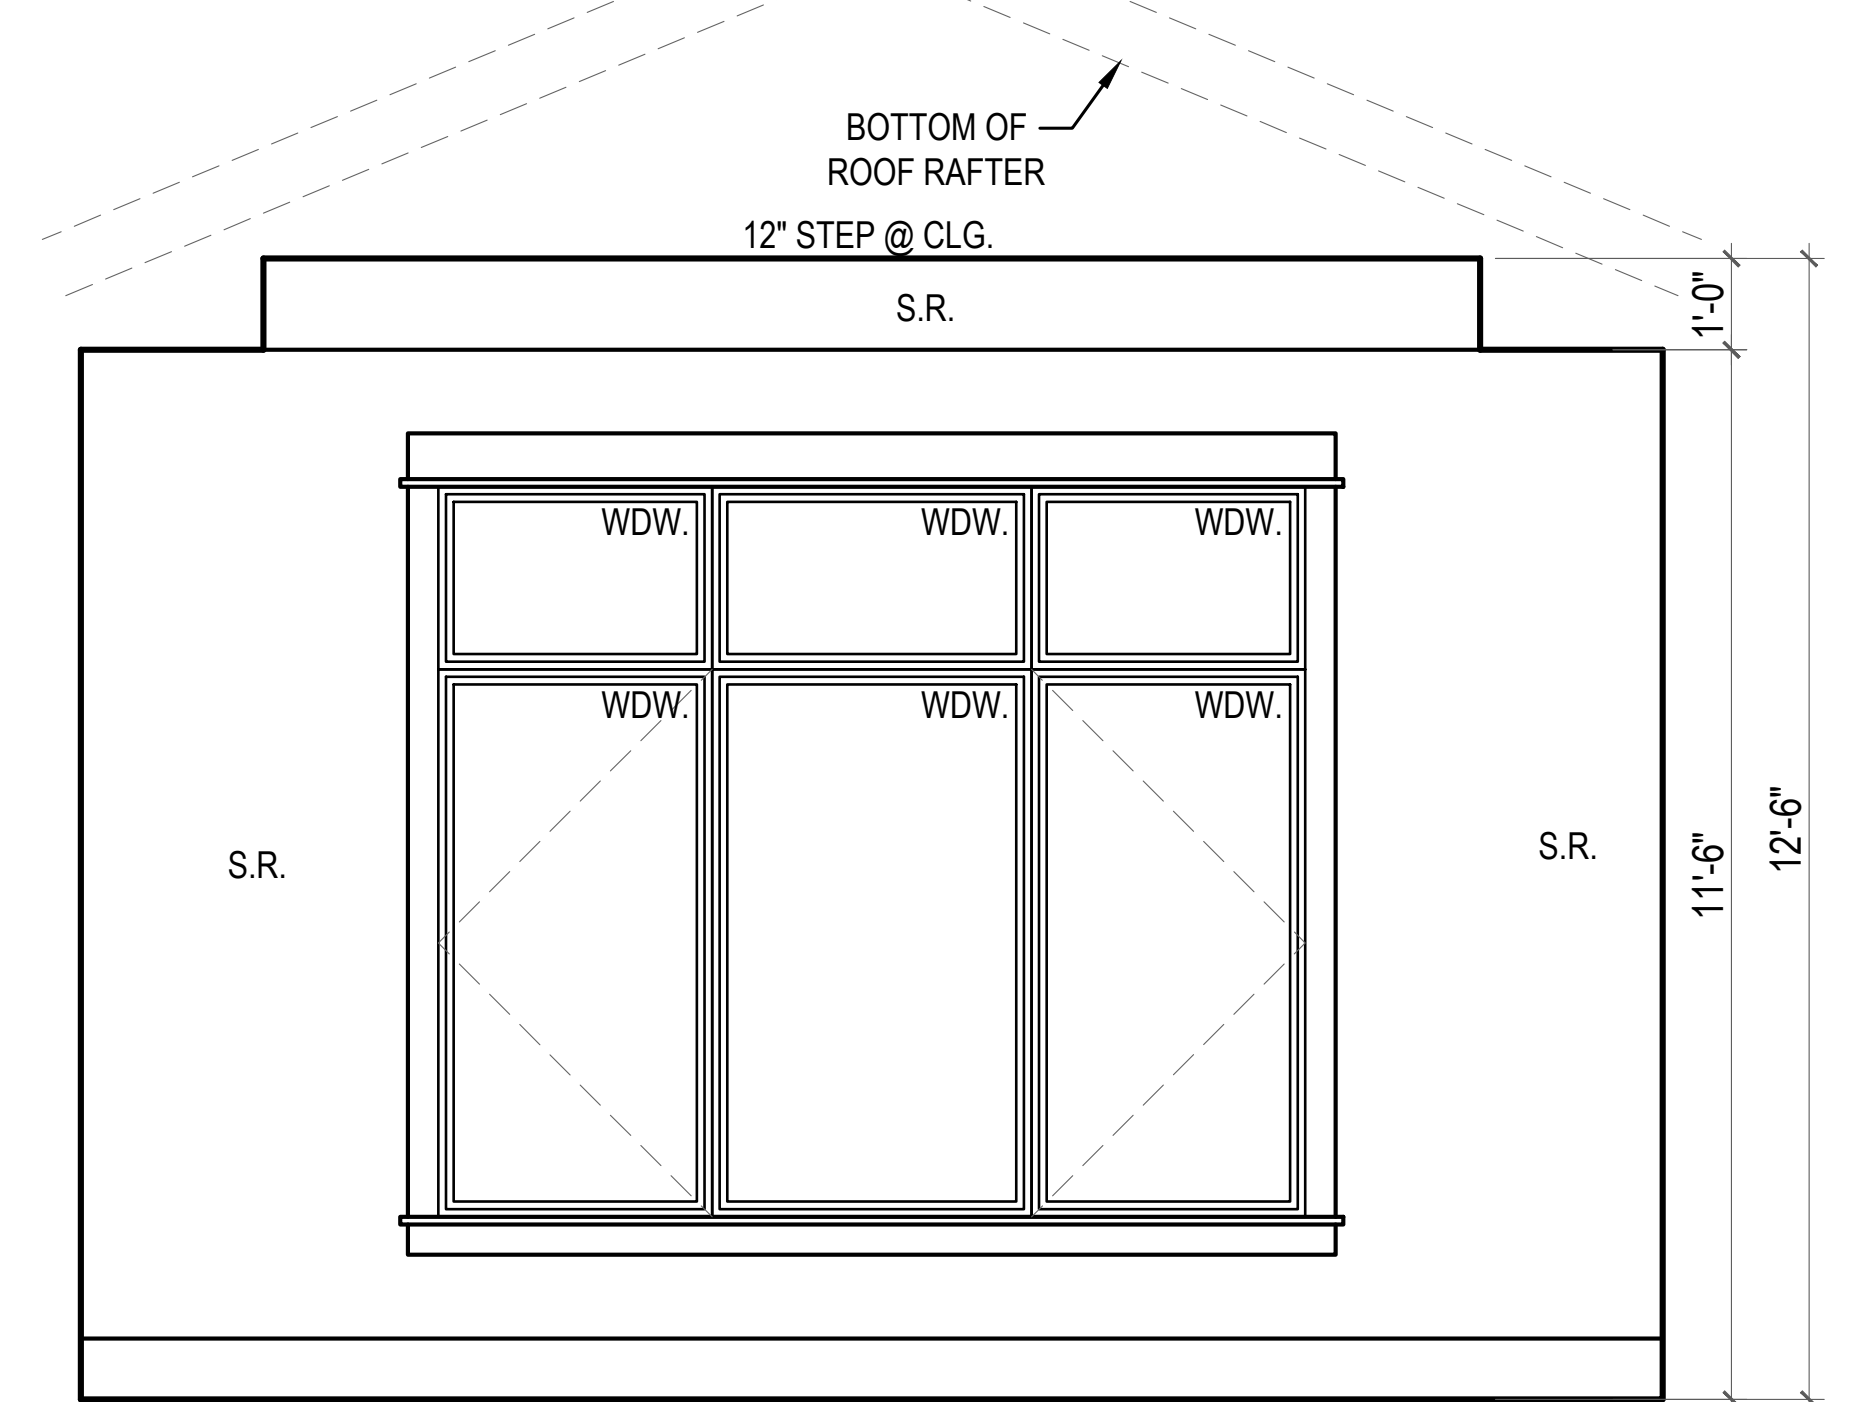


29 MASTER

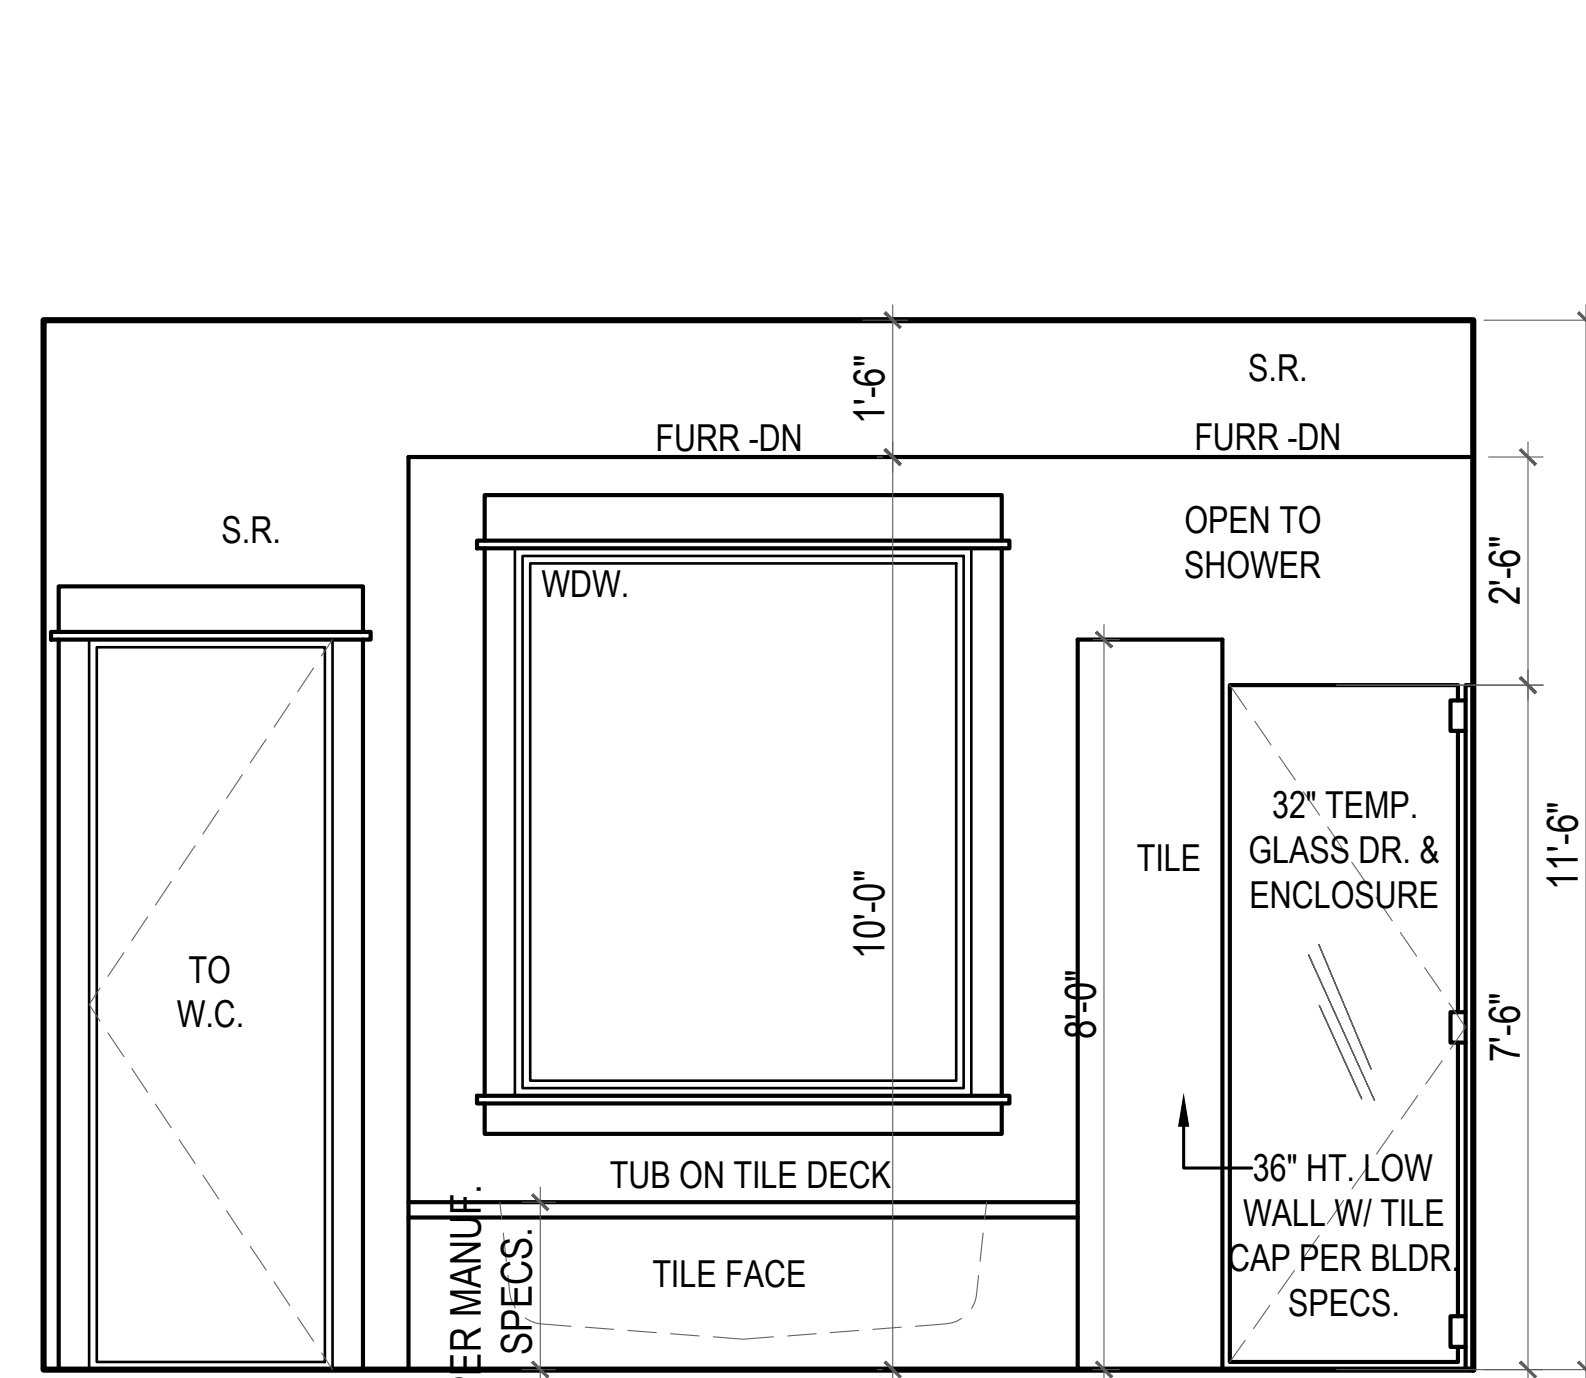


30 MASTER BATH

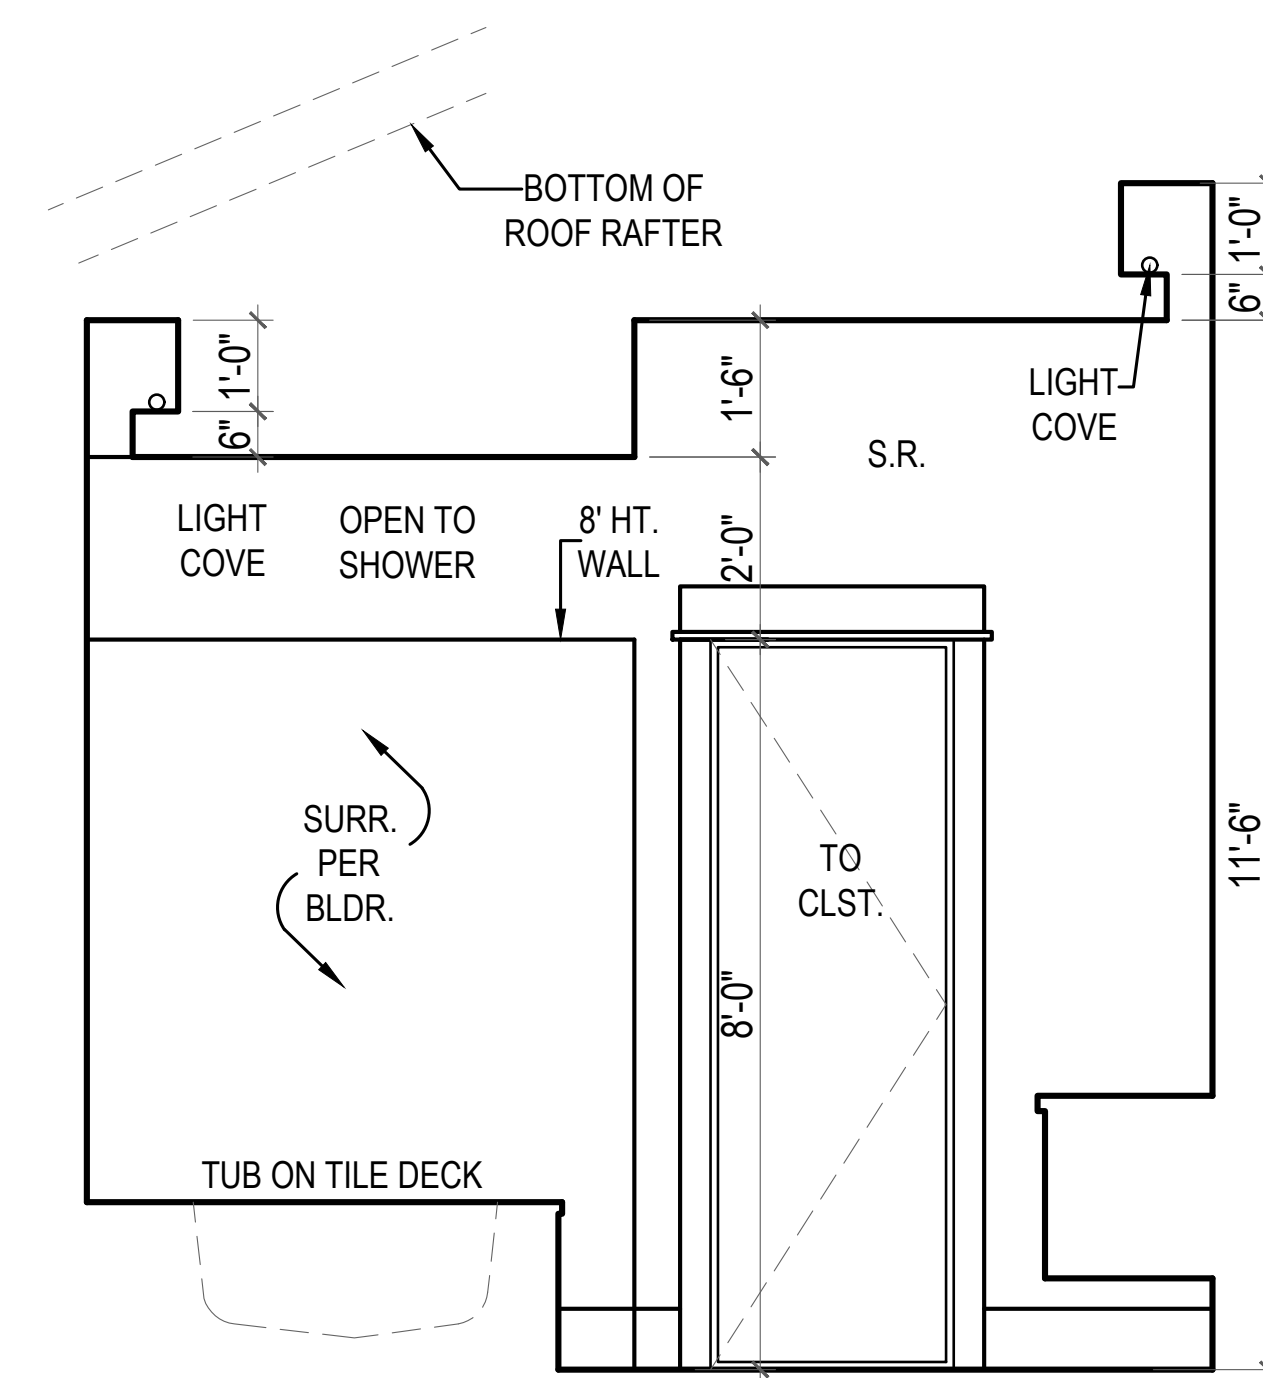

31 MASTER BATH

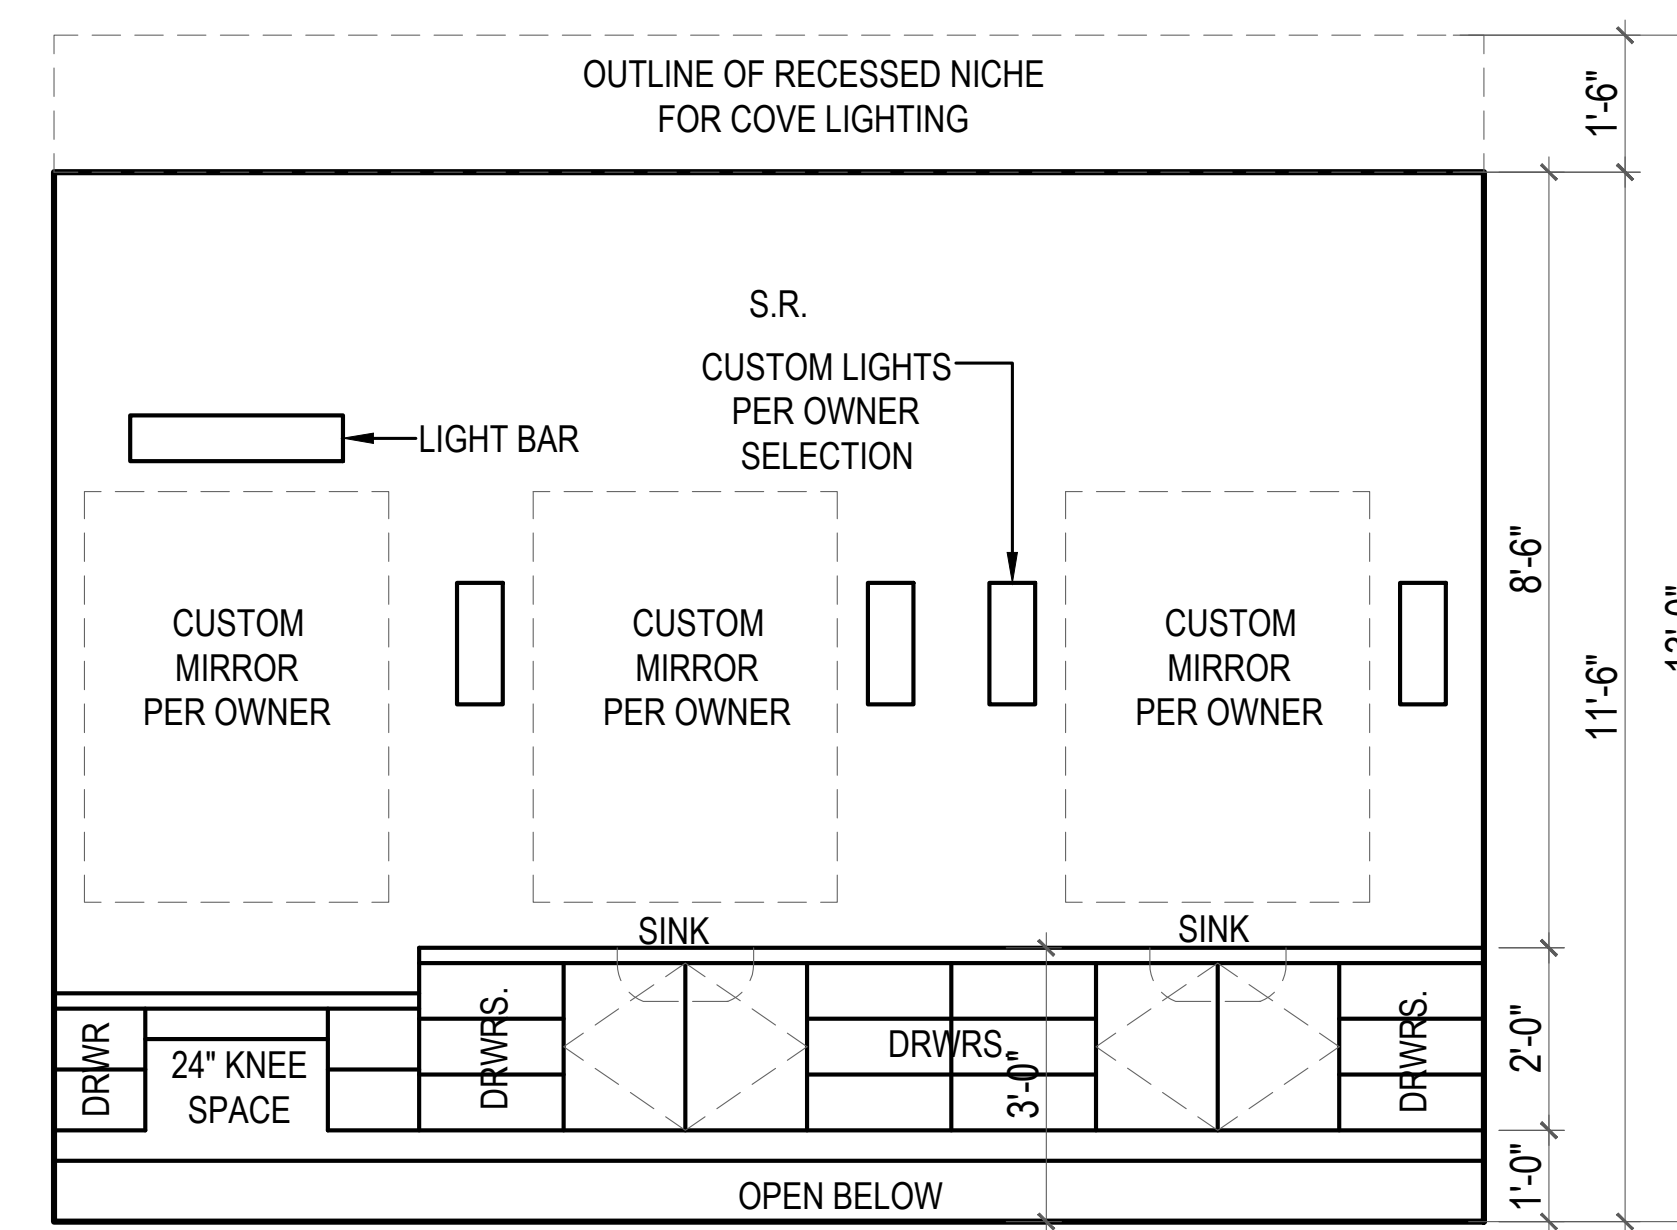





32 MASTER BATH

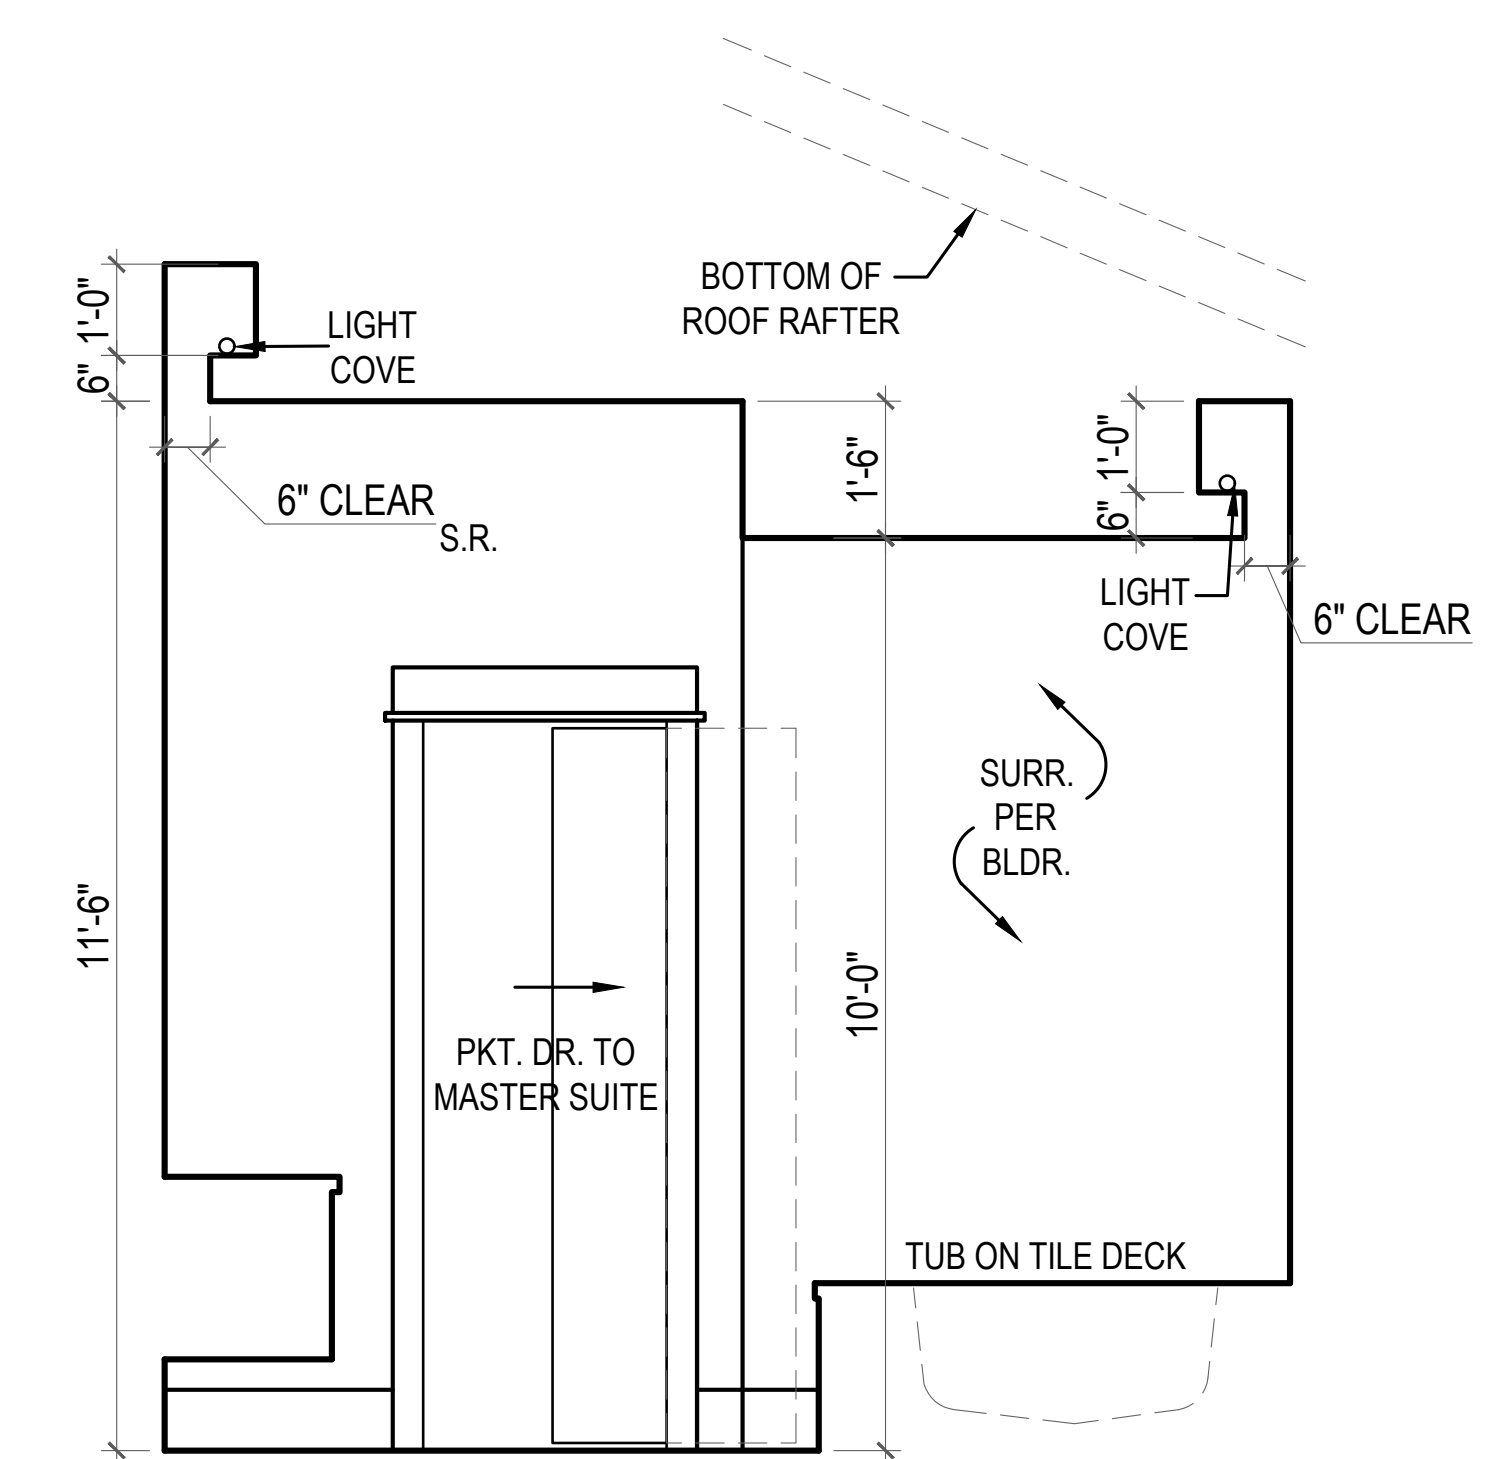


33 MASTER BATH

INTERIOR
ELEVATIONS
SCALE 3/8" = 1'-0"

 

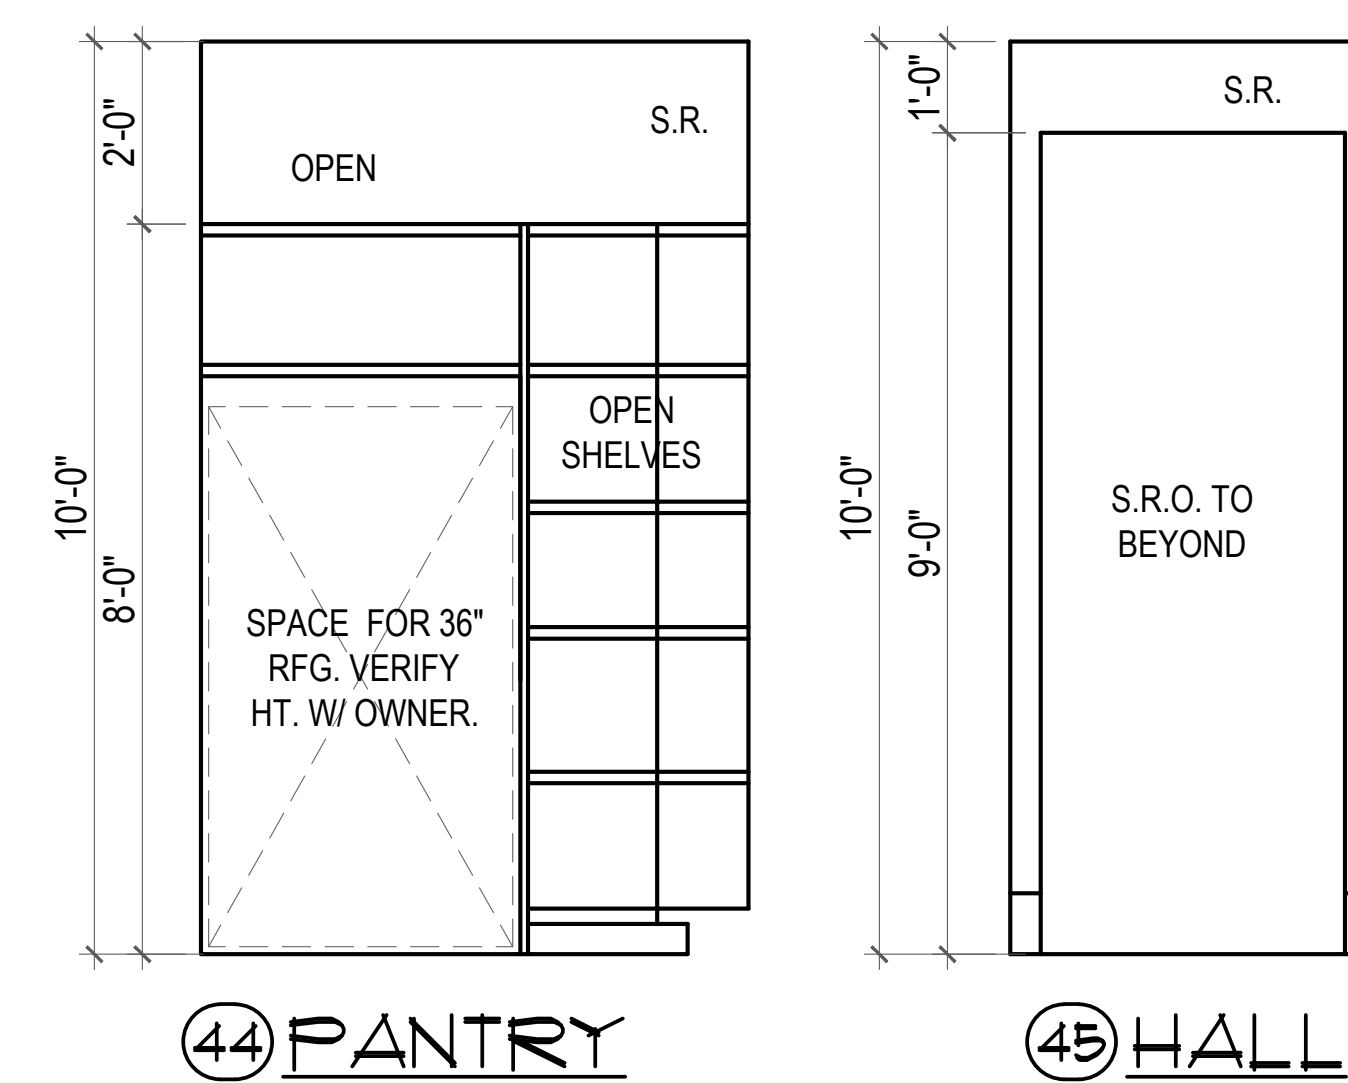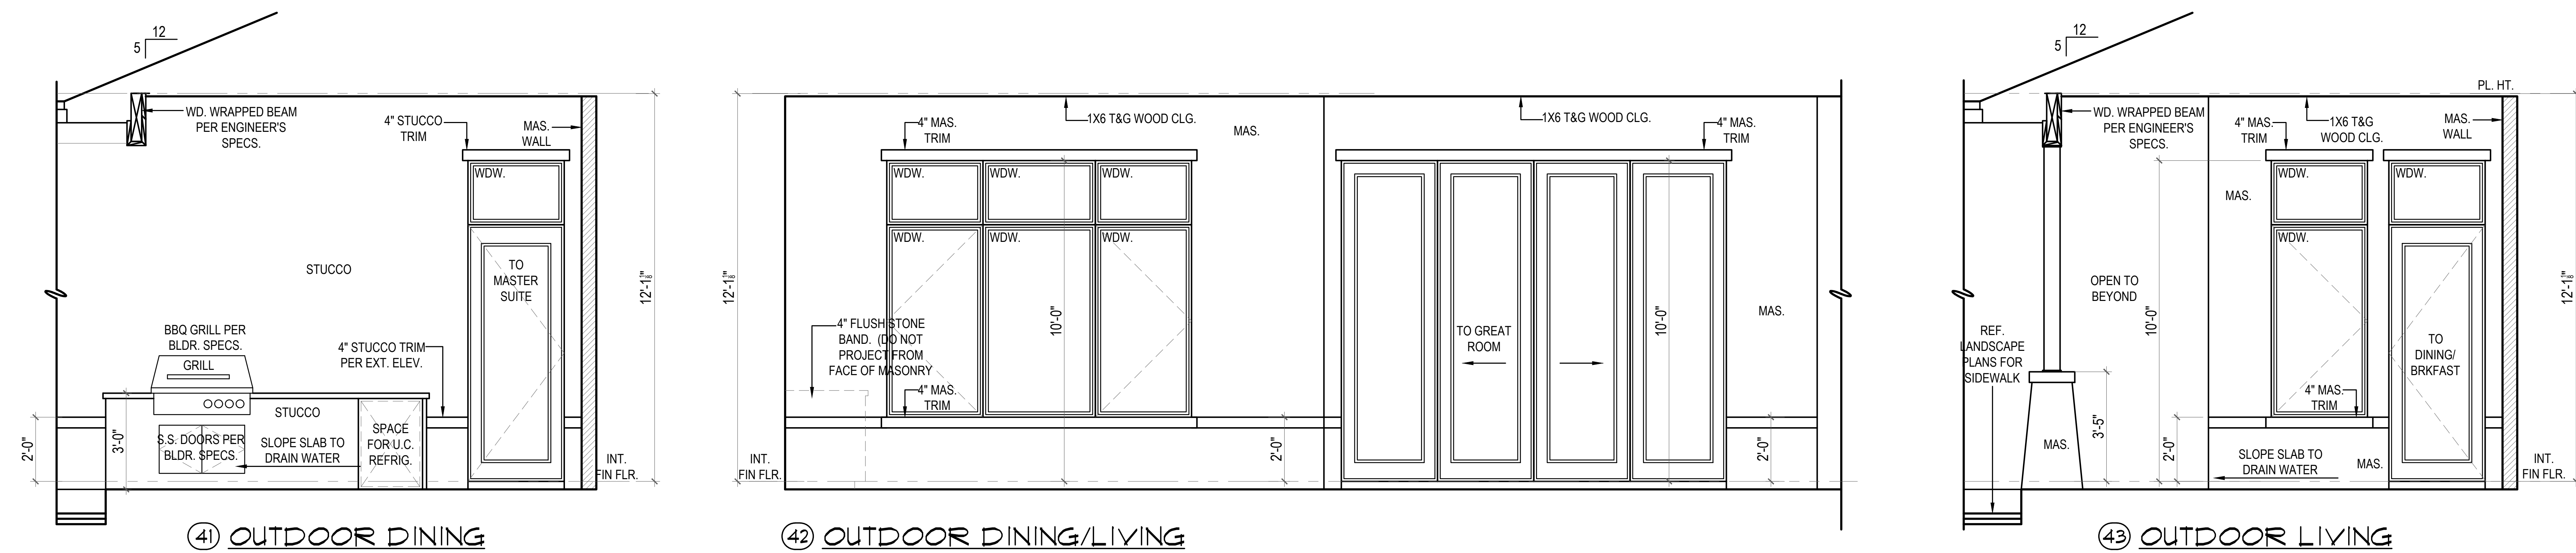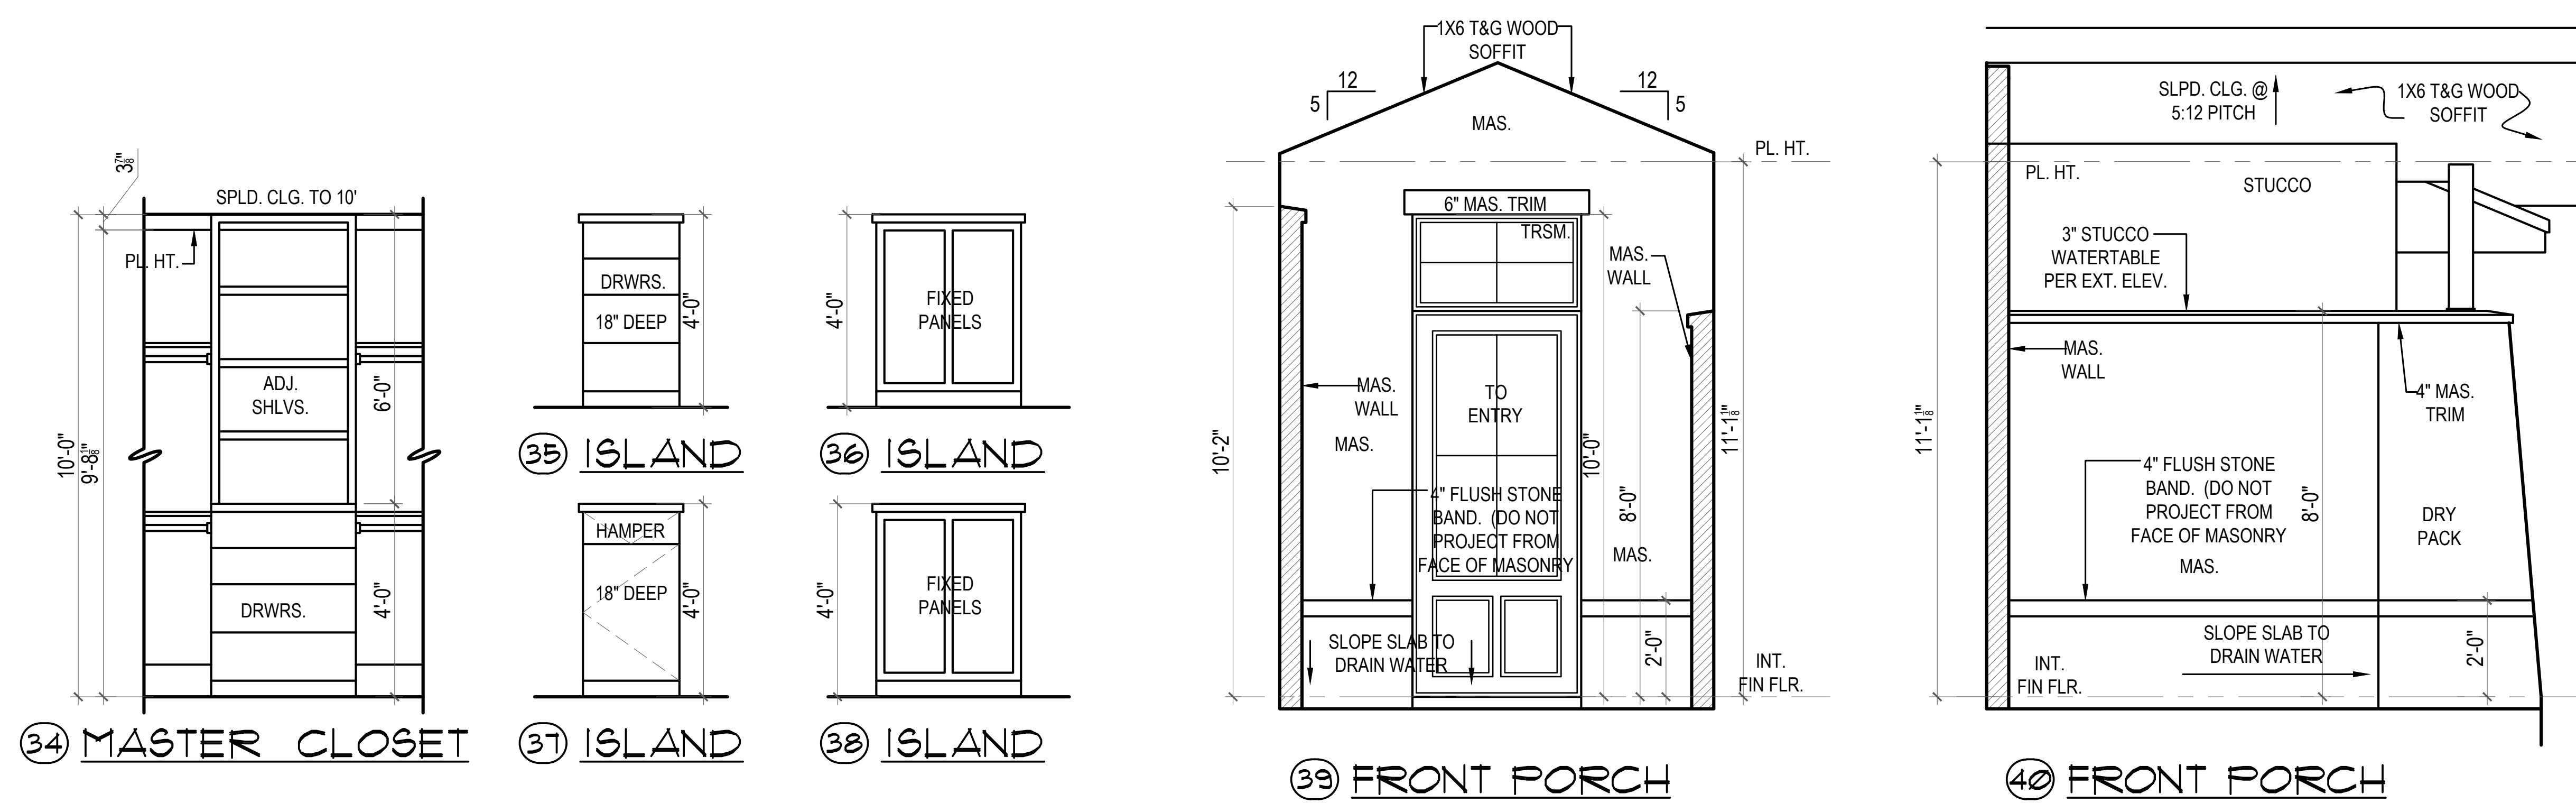

INTERIOR
ELEVATIONS
SCALE 3/8" = 1'-0"

 


SPECIAL ELECTRICAL NOTES

- E1** WATER HEATER IN CLOSET. PROV. FOR PUMPS, GAS, ELEC. WATER HARDWARE, AND FAN & DRAIN LINES AS REQ'D. INSTALL PER CODE & MANUF. SPECS.
- E2** HVAC IN ATTIC. PROVIDE LIGHT, ELEC. CONNECTIONS & UTIL. AS REQ'D.
- E3** COOK TOP. PROV. ALL ELEC. CONNECTIONS AS REQ'D. PER MANUF. SPECS. W/ VENT HOOD ABV. PER INT. DESIGNER. VENT LINER PER SPEC. PROVIDE ELEC. AS REQ'D.
- E4** HANGING LIGHT. VERIFY EXACT LOCATION W/ OWNER.
- E5** FLOOR OUTLET. VERIFY LOCATION WITH OWNER/BLDR.
- E6** PROV. ELEC. CONNECTION FOR TUB MOTOR IF REQ'D. PROVIDE ACCESS PANEL WITHIN REACH OF MOTOR.
- E7** QUAD-OUTLET AT BACK OF CABINET. REFER TO INT. ELEV. OUTLET AT 24" AFF.
- E8** OUTLET UNDER BAR.
- E9** TO ALL UNDER CABINET LIGHTING.
- E10** TV LOCATION. VERIFY HT. W/ BUILDER.
- E11** TO ALL COVE LIGHTS.
- E12** VERIFY LOCATION OF LIGHT BAR MOUNT OVER MIRROR.
- E13** COVE LIGHT ABOVE IN RECESSED NICHE.
- E14** PROVIDE ELEC. AS REQ'D. FOR GOLF CART CHARGING STATION.
- E15** EXTERIOR HANGING LIGHT W/ RIGID DOWN ROD.
- E16** PROVIDE OUTLET NO MORE THAN 6'-5" FROM GRADE PER DEED RESTRICTIONS.
- E17** PROVIDE ELEC. AS REQ'D. FOR HVAC MAINTENANCE EQUIPMENT WITHIN REACH OF CONDENSER UNIT.
- E18** PROVIDE ELEC. AS REQ'D. FOR E.V. CHARGING STATION. VERIFY LOCATION W/ OWNER.

ELECTRICAL LEGEND

- | | |
|--|--|
| SWITCH | HANGING LIGHT |
| PRESSURE SWITCH | CEILING MOUNTED FIXTURE |
| SWITCH - 3 WAY | RECESSED CAN LIGHT |
| SWITCH - 4 WAY | RECESSED CAN LIGHT FOR VAULTED CLG. |
| SWITCH - DIMMER | RECESSED CAN LIGHT DIRECTIONAL |
| SWITCH - GFI | RECESSED CAN LIGHT WATERPROOF |
| SWITCH - WATERPROOF | WALL MOUNT FIXTURE |
| PHONE OUTLET | 4" RECESSED CAN LIGHT |
| FLR. PHONE OUTLET | LOW VOLT. HALOGEN (SPECIALTY LT. TYPE-A) |
| FLOOR OUTLET | SPECIALTY LT. TYPE-B |
| TELEVISION OUTLET | SPECIALTY LT. TYPE-C DIRECTIONAL SPOT. |
| A/V-MEDIA OUTLET (2-COAX 2-CAT 5 PHONE LINE) | FUCK LIGHT |
| PUSHBUTTON FOR GAR. DR. OPENER | FLUOR. LIGHT 2' X 4' |
| JUNCTION BOX | FLUOR. LIGHT 1' X 4' |
| OUTLET - 110V DUPLEX | CABINET LT. - ABV. CAB. |
| OUTLET STRIP BELOW UPPER CABINETS | CABINET LT. - BLW. CAB. |
| OUTLET -DEDICATED CIRCUIT | CABINET LT. - ABV. 4 BLW. CAB. |
| OUTLET - 110V QUADPLEX | COVE LIGHTING IN CEILING |
| OUTLET - 110V WATERPROOF | TRACK LIGHT |
| OUTLET - 220V | FLOOD LIGHT (SHIELDED) |
| SPLIT WIRE FOR SWITCH PLUG SWITCH TOP PLUG ONLY | HEAT LITE |
| OUTLET AT CLG. FOR GARAGE DOOR OPENER | VENT/EXHAUST |
| EXT. DOOR BELL | VENT/LIGHT COMBO |
| CHIMES | VENT/LIGHT/HEAT COMBO |
| THERMOSTAT | CEILING FAN (WITHOUT LIGHT KIT) |
| SMOKE DETECTOR & CARBON-MONOXIDE DETECTOR COMBO. | |
| HEAT DETECTOR | |
| SPEAKER | |
| WALL SPEAKER | |
| ELEC. PANEL | |
| NETWORK PANEL | |
| GAS VALVE | |
| GAS KEY | |
| CLG. FAN W/ LIGHT KIT | |

NOTE TO ELECTRICIAN:
ALL OUTLETS AT KITCHEN, BATHS, UTILITY ROOM, GARAGE, EXTERIOR SPACES AND OTHER "WET" AREAS TO BE GFI.

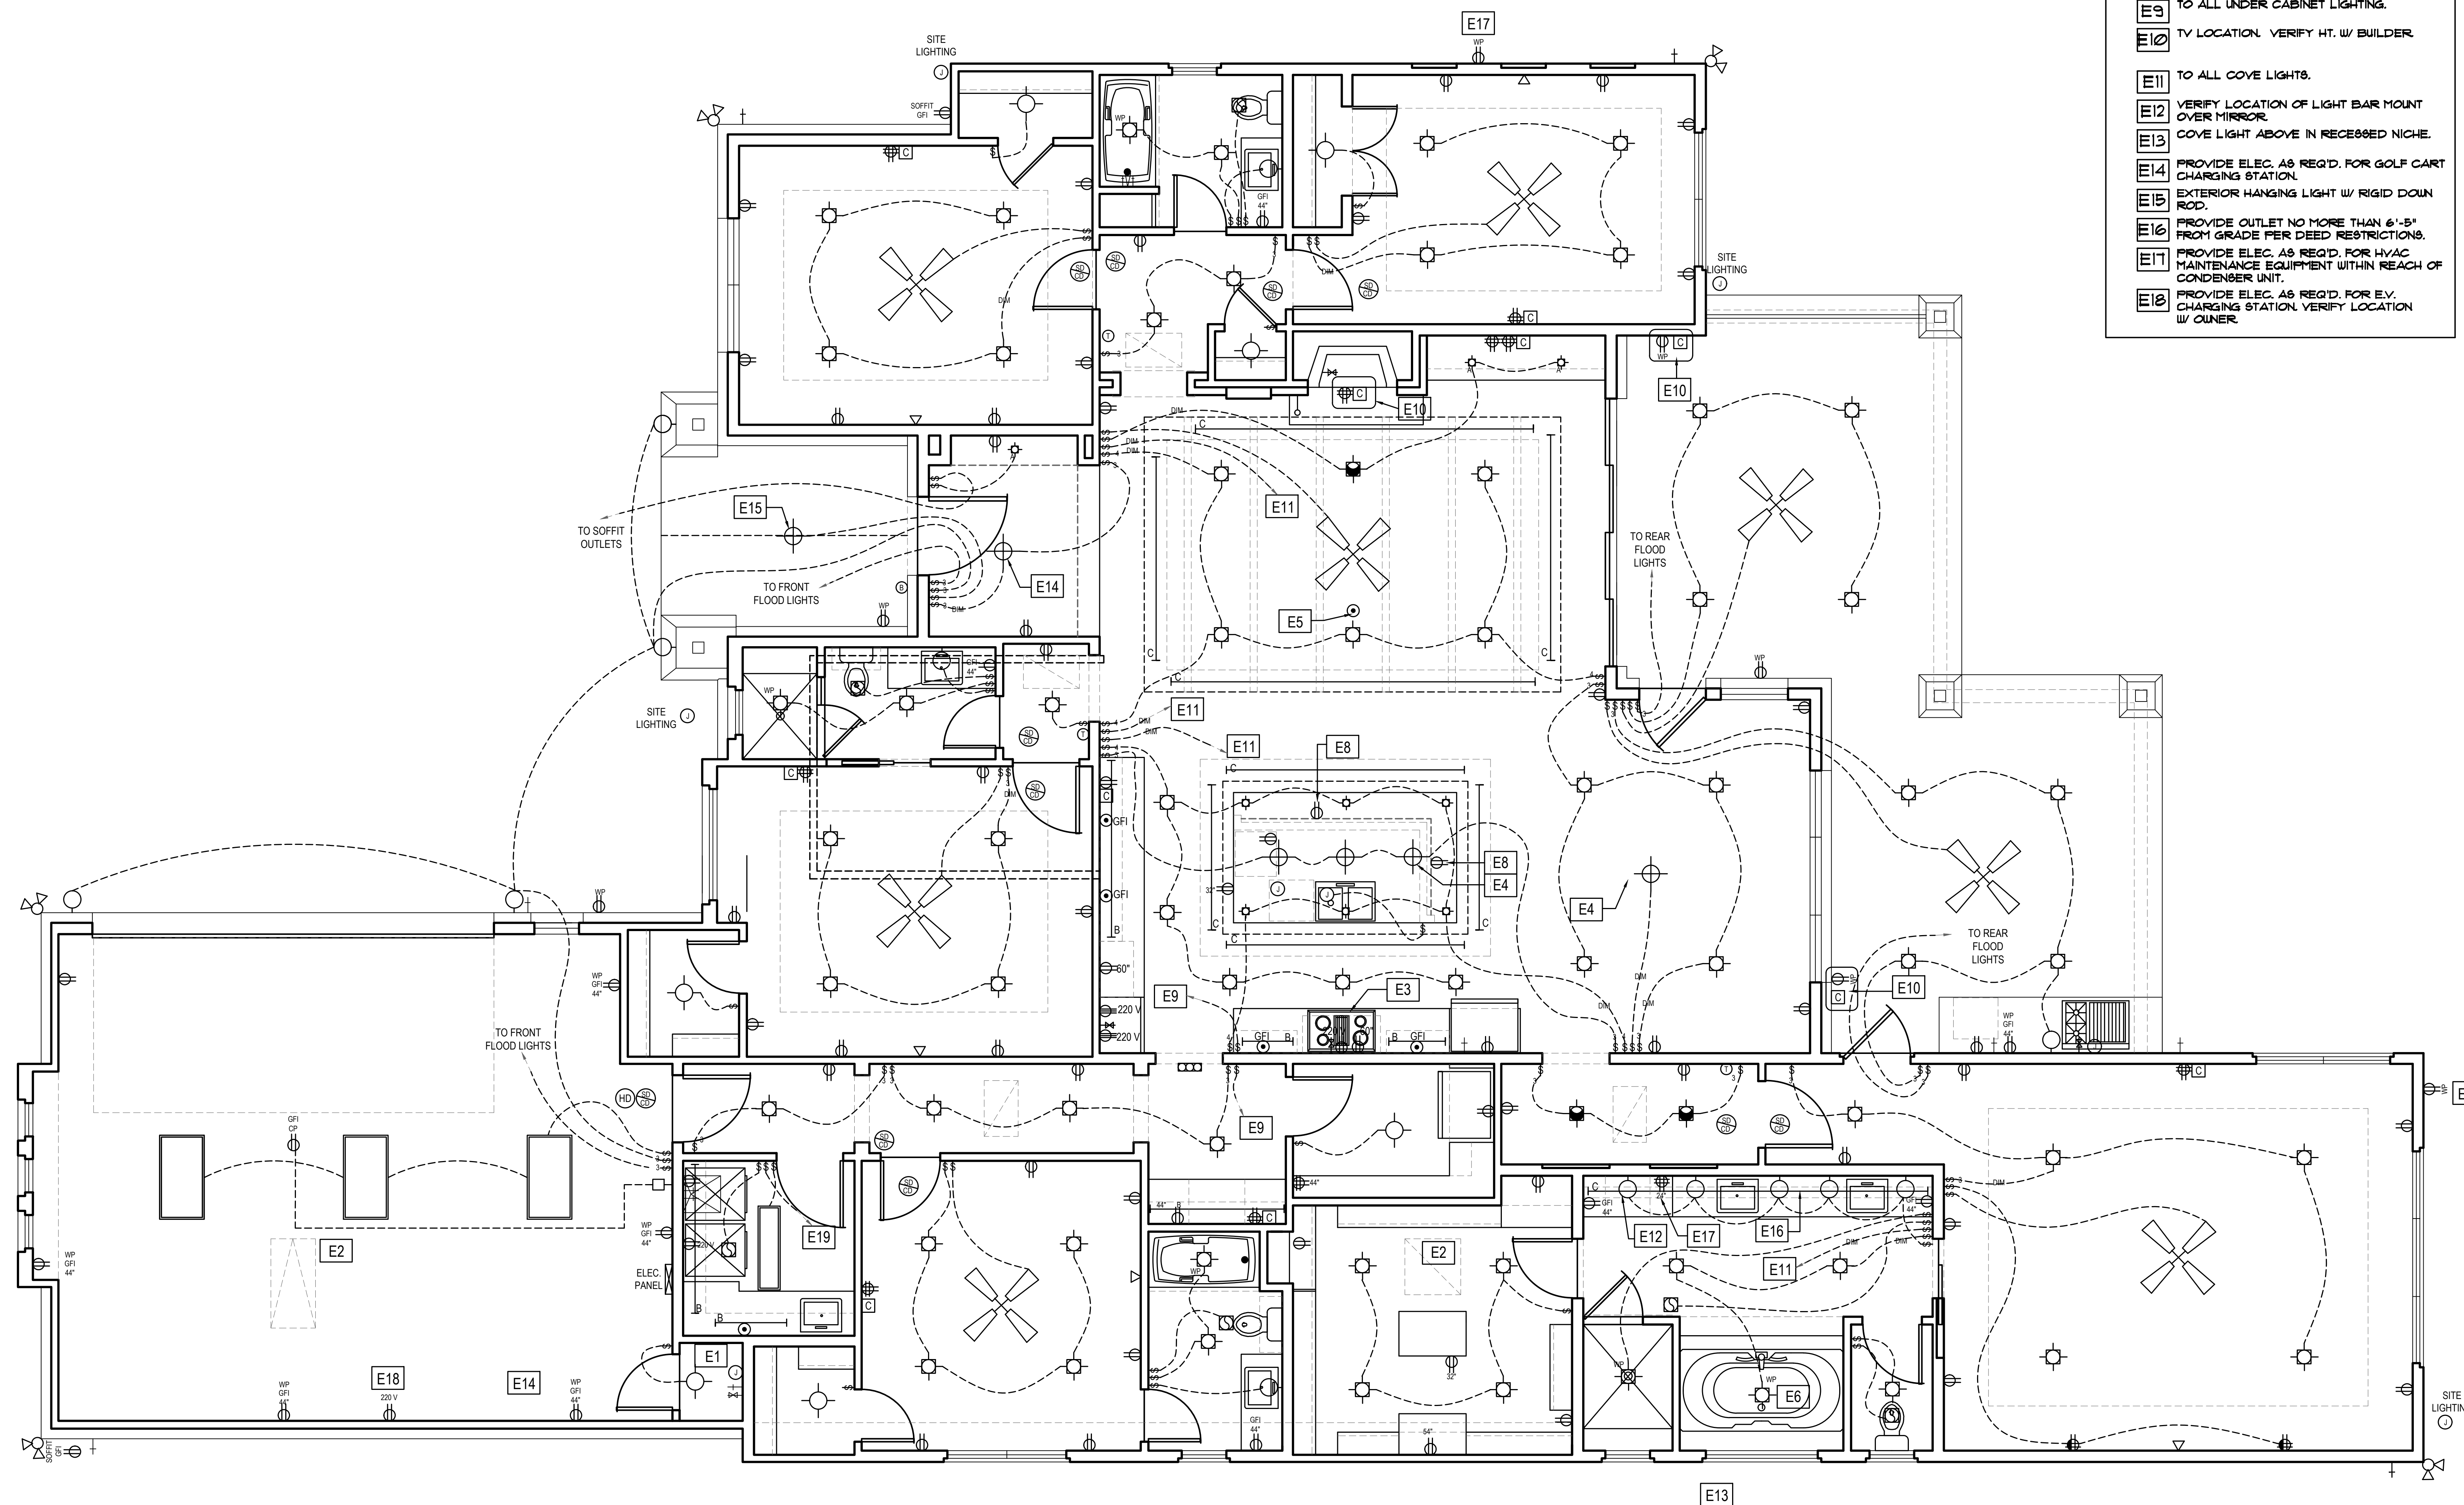

ELECTRICAL PLAN

SCALE 1/4" = 1'-0"

OWNER:
LINDSAY & BLAKE TAYLOR
XXXX XXXXX VIEW LN.
XXXX, TEXAS 71024
T.(XXX) XXX-XXXX

BUILDER:
XXXX XXXXX
XXXXX CUSTOM HOMES
2303 RR620 SOUTH, SUITE 135-212
AUSTIN, TEXAS 78734
T.(XXX) XXX XXXX

ARCHITECT:
KAI GESCHKE
GESCHKE GROUP ARCHITECTURE
11200 RANCH RD. 2222
AUSTIN, TEXAS 78730
T.(512) 502 8484

ENGINEER:
XXXX XXXXXXX
XXXXXX ENGINEERING, LLC
1120 COTTONWOOD CREEK TRAIL
CEDAR PARK, TEXAS 78613
T.(XXX) XXX-XXXX